1.THREE LEAF TELESCOPIC
GATE (6X2.1m) TRACK

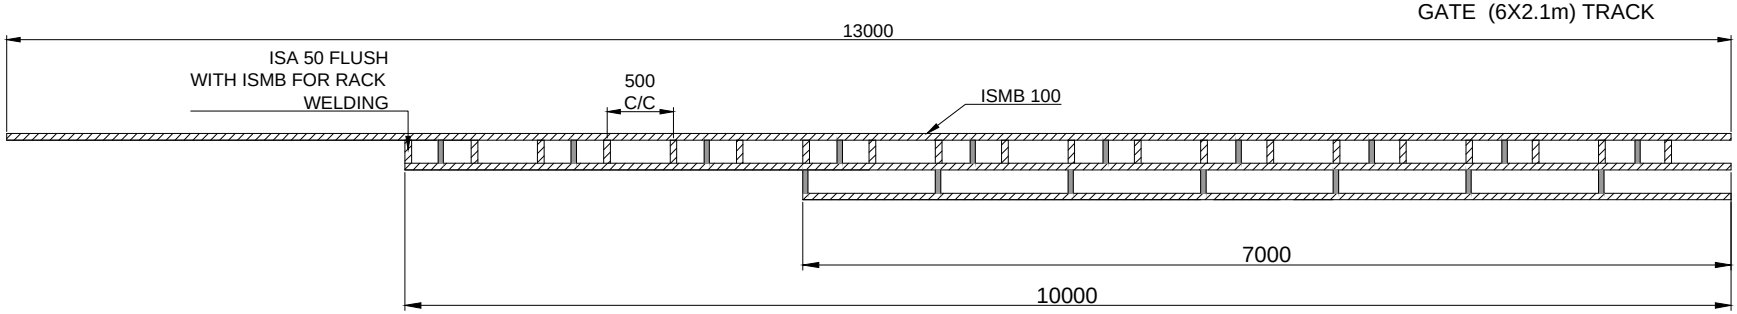

2.THREE LEAF TELESCOPIC
GATE (6X2.1m) TRACK

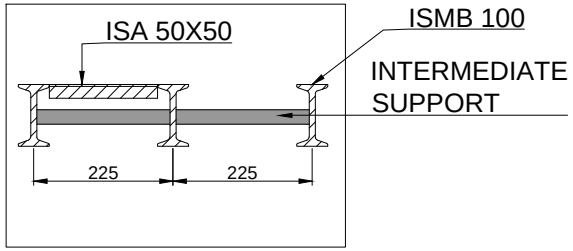

THREE LEAF TELESCOPIC
GATE TRACK

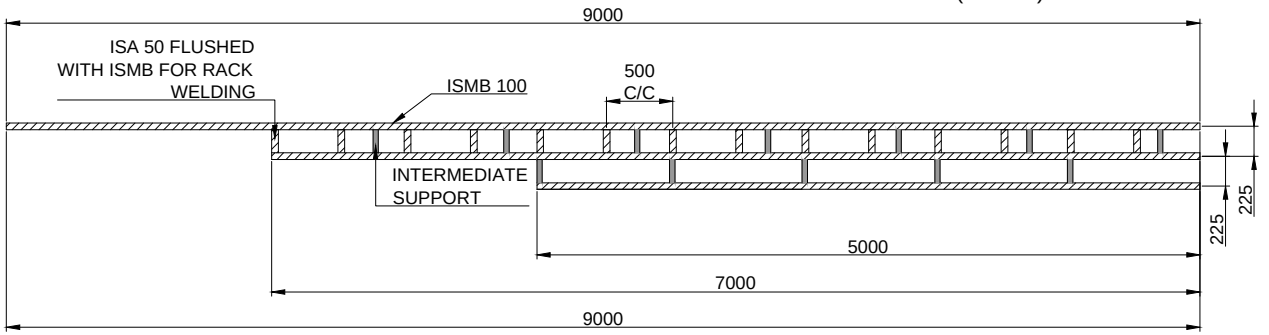

3.TWO LEAF TELESCOPIC
GATE (4X1.8m) TRACK

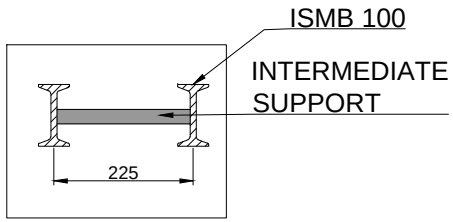

TWO LEAF TELESCOPIC
GATE TRACK

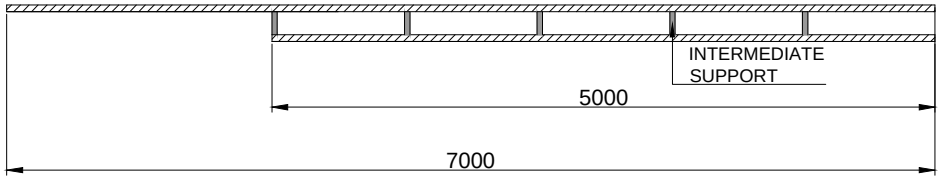

This drawing & design is the property of NIHVA TECHNOLOGIES. Not to be sold or copied to any other concern.

TITLE: TELESCOPIC GATE TRACK			NIHVA TECHNOLOGIES PVT. LTD. PUNE Tel : 020 66304033 Email:- info@nihva.com Website:- www.nihva.com
	NAME	DATE	
DRAWN	OMKAR	26/10/17	CLIENT - LUPIN LIMITED
CHECK	SHEKHAR	26/10/17	PROJECT -
REV.			SITE LOCATION - MIHAN, NAGPUR
APPROVAL	SHEKHAR	26/10/17	DWG. NO. : NIHVA/17-18/0264 REV -0
If any queries contact : projects@nihva.com			SCALE: NTS WT: SHEET: 01 OF 01
ALL DIMENSION ARE IN mm			