



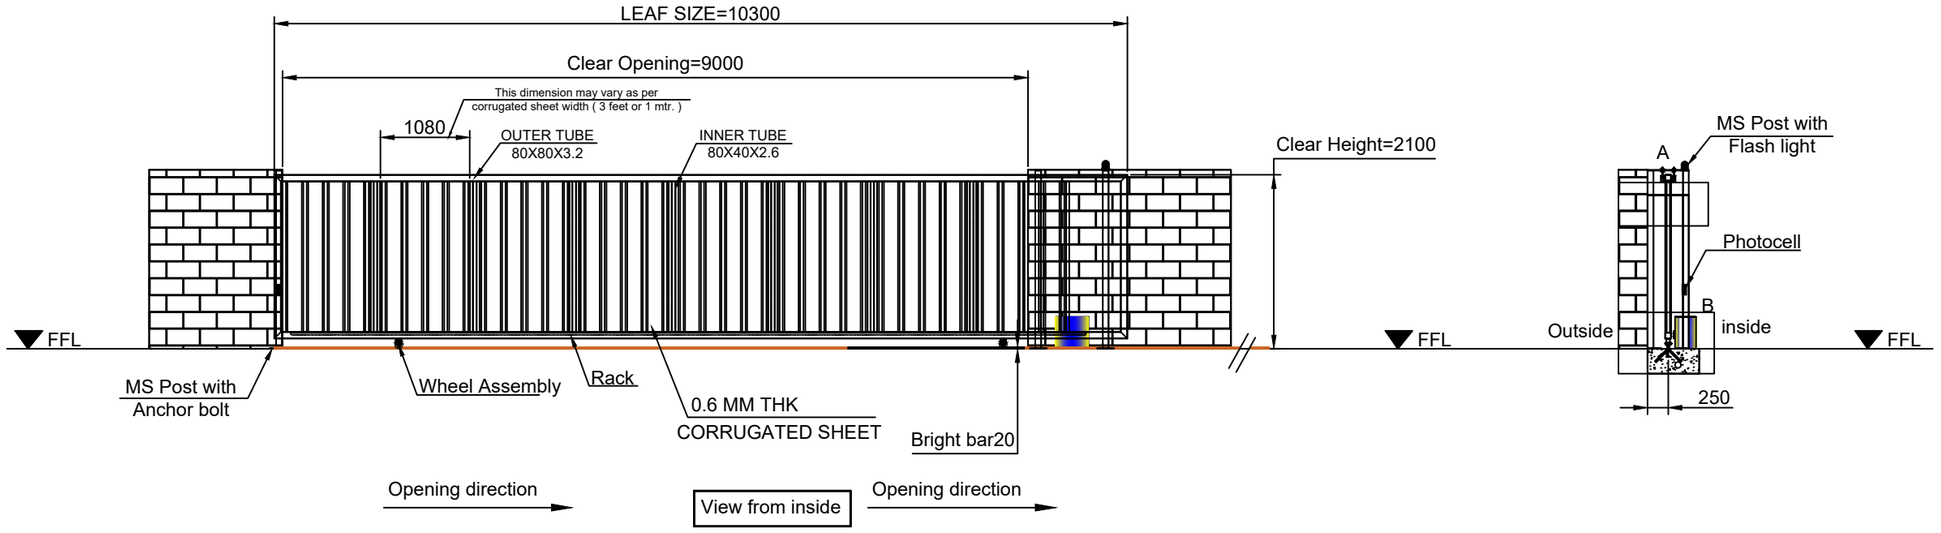


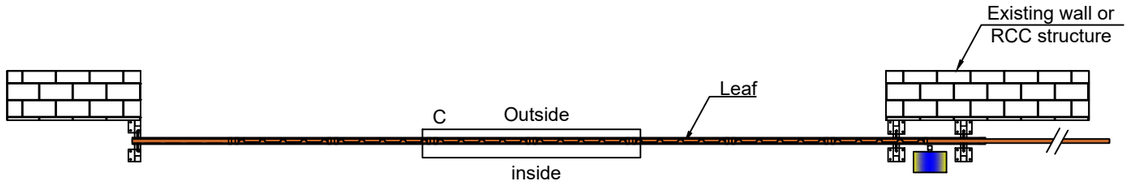

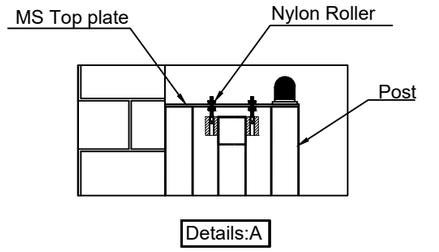

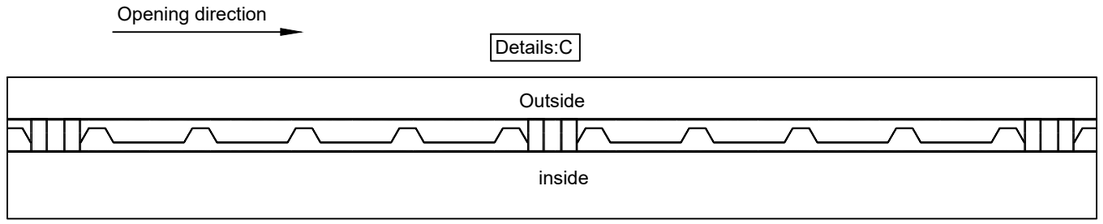

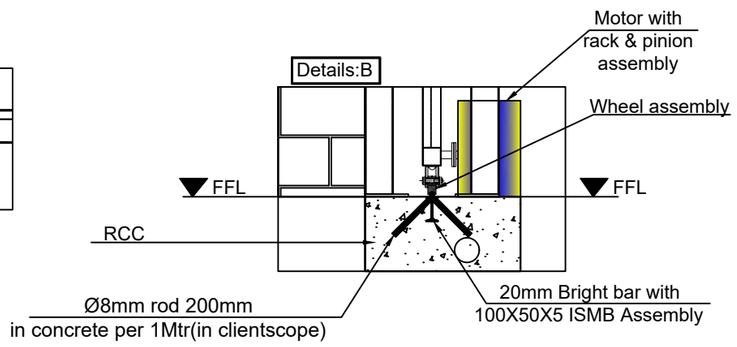

Note:-

1.All Dimension are in MM.
2.All Civil work and if required motor foundation or ms bracket will be in Client scope
3.Civil,Installation and Fabrication Tolerance will be ±20mm
4.Reuired Parking will be 10400 mm
5.Surface Finish(painting): Approved RAL
6.Distance between tubes may vary as per corrugated sheet sizes

Rev No.	Revision	Date	Revised By

This drawing & design is the property of NIHVA TECHNOLOGIES. Not to be sold or copied to any other concern.

TITLE:- Motorized Sliding Gate				NIHVA TECHNOLOGIES PVT. LTD. PUNE Tel : 020 66304033 Email:- info@nihva.com Website:- www.nihva.com		
	NAME	DATE	SIGN			
DRAWN	NIRMALA	02/03/2023		CLIENT - Farmson Pharmaceutical Pvt. Ltd. Gujarat.		
CHECK	A.K	02/03/2023		LOCATION -		
APPRD.	V.T	02/03/2023		PRODUCT - Motorized Sliding Gate		QTY-01
If any queries contact : design@nihva.com				DWG NO:- NIHVA/22-23/CLT/0187		REV-00
ALL DIMENSION ARE IN mm				SCALE: NTS	SCALE:-- 1:1	SHEET: 01 OF 01