

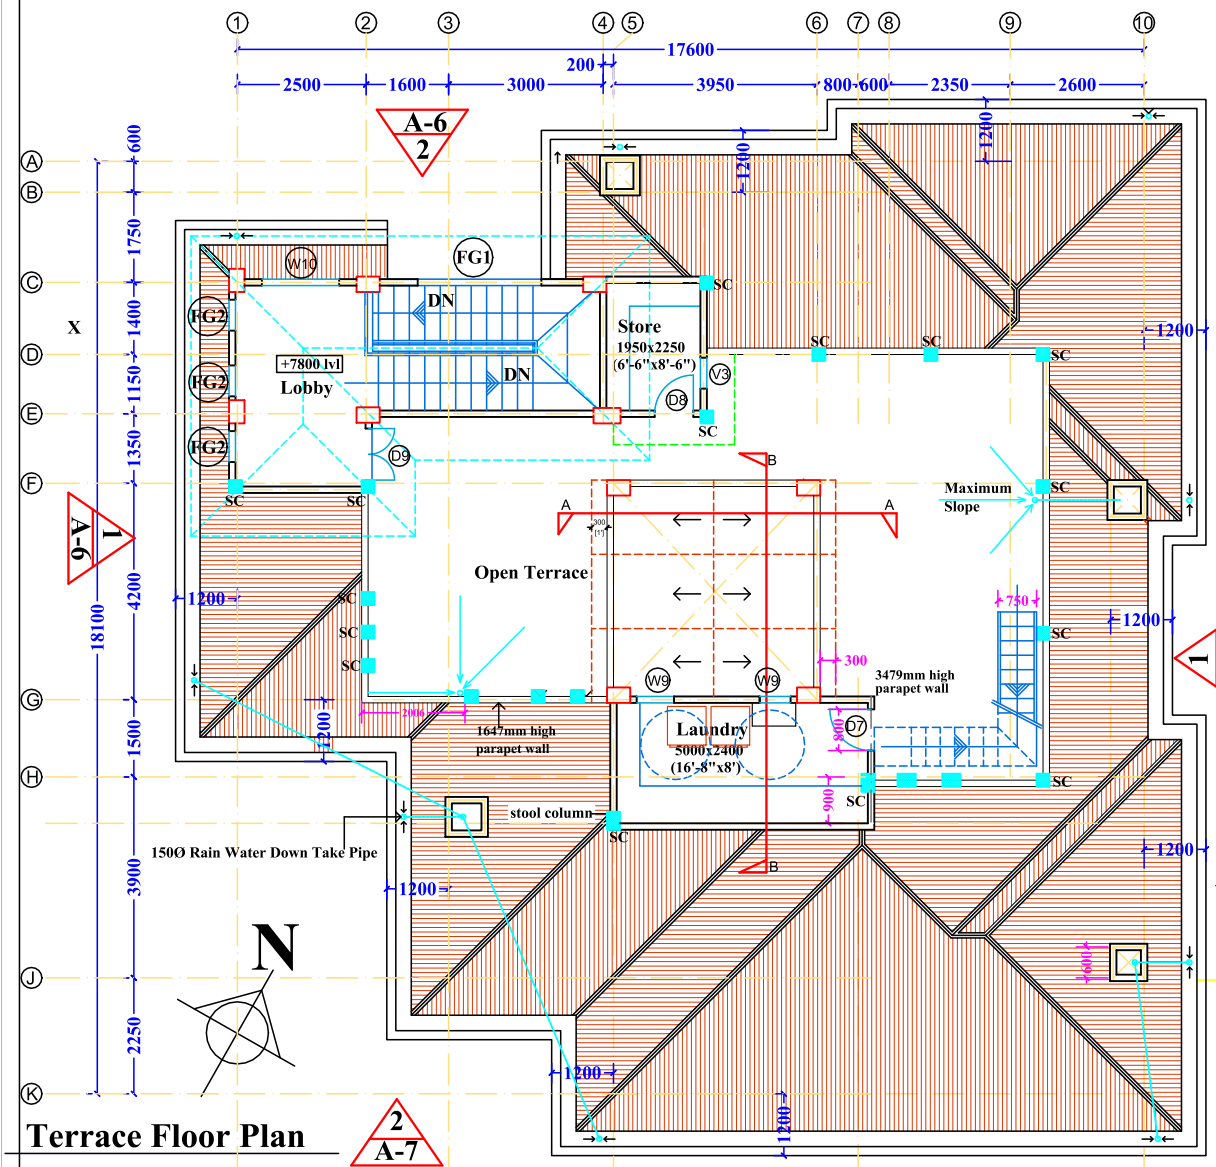


Terrace Floor Plan

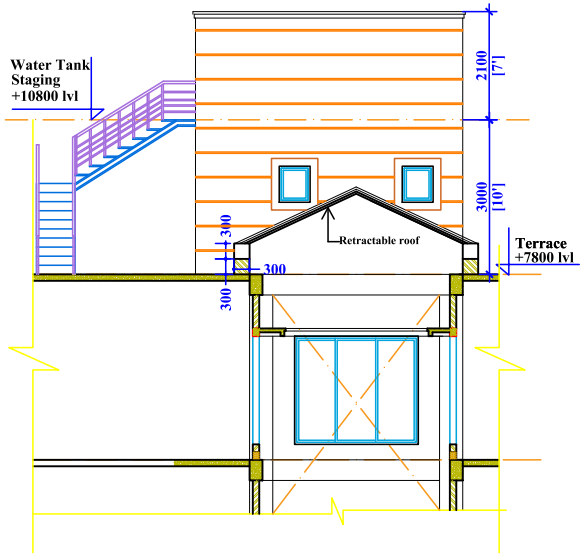

Part Section- AA

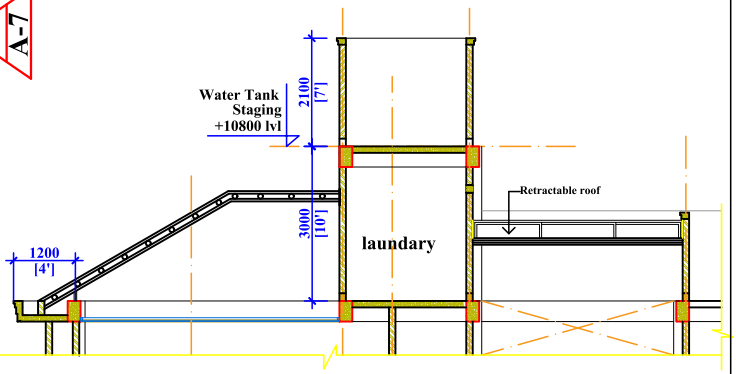

Part Section- BB

NO.	REVISION	DATE	NO.	ISSUED TO	DATE	NO.	ISSUED TO	DATE	NO.	ISSUED TO	DATE	NO.	ISSUED TO
					10/6/22	PDF	Client						

PROJECT:
Mr.Nerendra Kumar Saharia
Bungalow at Dibrugarh.

TITLE: Roof Plan

DLT : Sima Debnath
APPD :
SCALE : NTS
DATE : 10/6/22

DRG NO.
A-5

2K2006

HARPAL SINGH ASSOCIATES
SHANKAR COMPLEX, 4TH FLOOR, OPPOSITE TRENDS
MALL, CHIRISTAN BASTI,G.S. ROAD, GHY-781005,ASSAM
Ph: (0361)2343179,2343180,E-mail ID:hsaghy@gmail.com

THIS DRAWING IS THE PROPERTY OF HARPAL SINGH ASSOCIATES
AND NOT TO BE COPIED OR USED WITHOUT HIS PERMISSION.