




PLAN

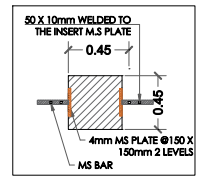


DETAIL 'A'

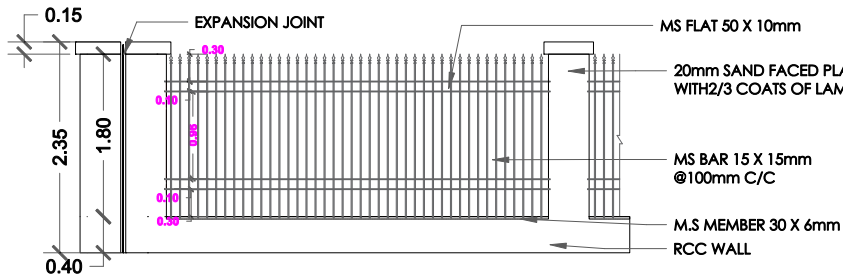

MS GRILL DETAIL 'B'

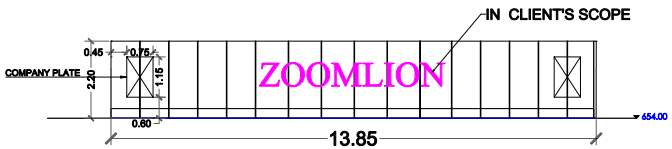


ELEVATION-AA

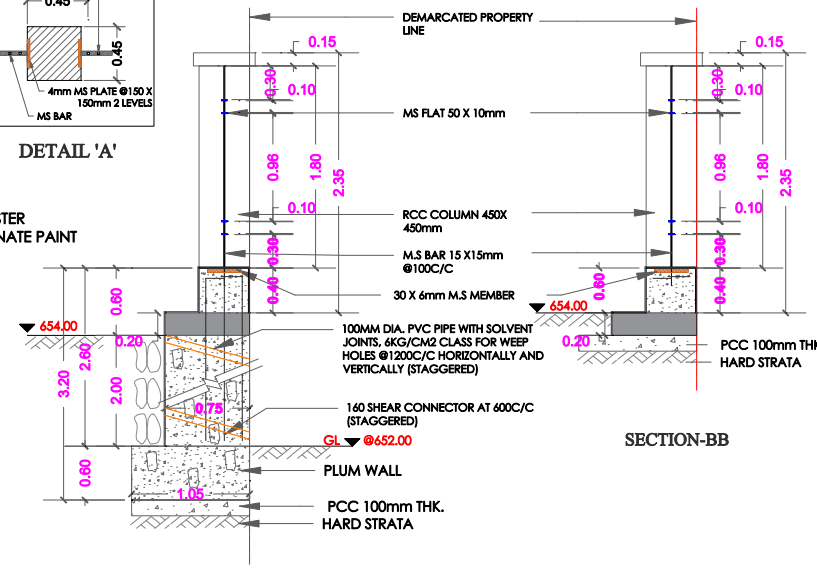

SECTION-AA


SECTION-BB

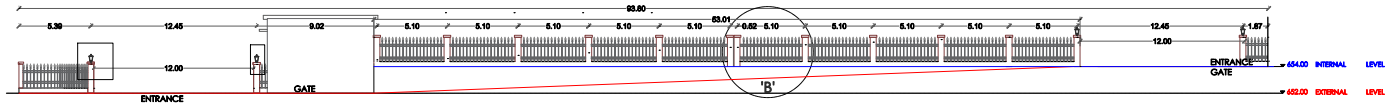

ELEVATION-BB

ELEVATION-CC

ELEVATION-DD

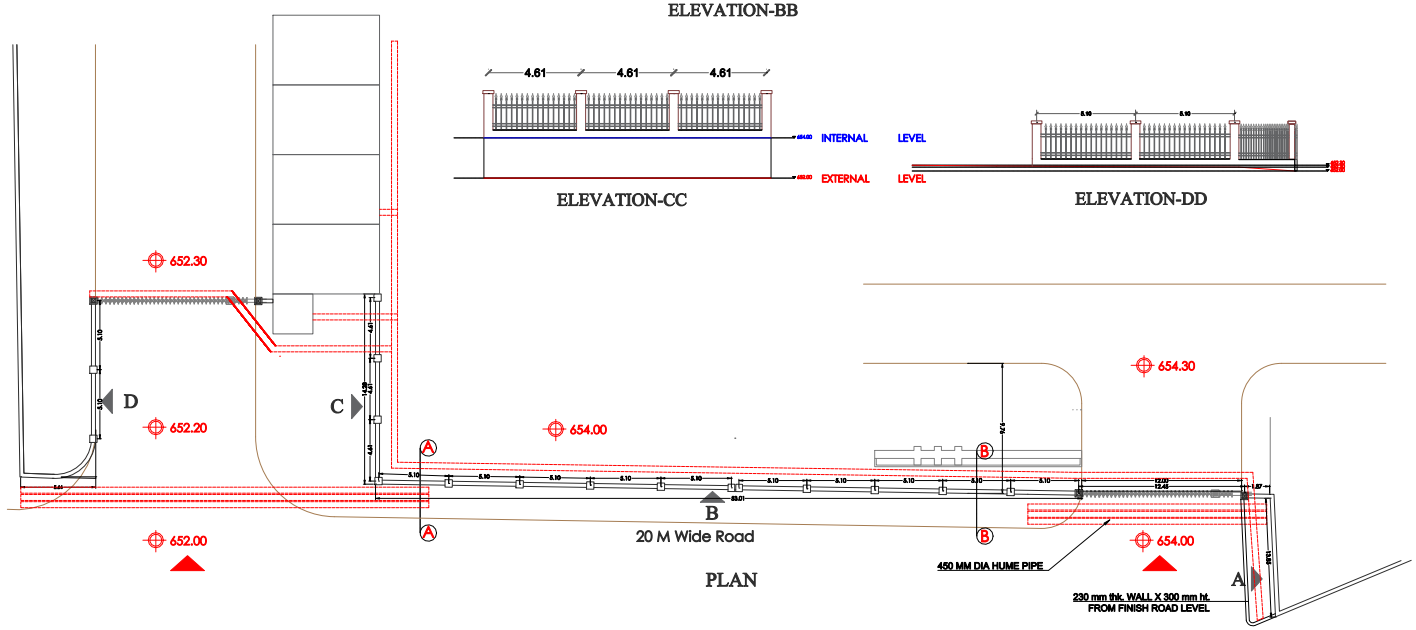


PLAN

ARCHITECTURAL DRAWING

Date	Revision	Note
28.01.2023	R0	Revised as per recommendation of fire officer dated 20.01.2023

LEGENDS:

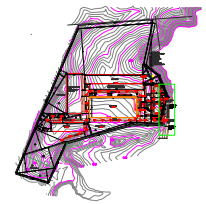

KEY PLAN

GOOD FOR CONSTRUCTION

Note:

1. The drawing shall not be scaled and only written dimensions are to be followed.
2. Any discrepancy shall be brought to the notice of the Architect before execution of work.
3. The drawing shall be read in conjunction with structural drawing.
4. This drawing is the property of Arcaids Architectural Consultants Pvt. Ltd. and shall not be reproduced or used without their written permission.

SHEET TITLE : GENERAL SITE LAYOUT

EAST SIDE COMPOUND WALL DETAILS

CLIENT:

ZOOMLION INDIA INDUSTRIAL PARK PHASS I AT - KHED CITY, TAL.KHED, PUNE. PLOT NO IP 24 , MIDC KHED, PUNE.

CONTRACTOR:

CHINA CONSTRUCTION ENGINEERING BUREAU GROUP CO., LTD

CHINESE DESIGN TEAM :

CHINA CONSTRUCTION ENGINEERING BUREAU GROUP CO., LTD

CONSULTANT :

North	Drawing by:
	MRUNALI
	Checked by:
	AAH
Date	Dwg no.
02.03.2023	ARCZEML/SITE/WD/069
Scale	Job no.
NTS	621

M/S. ARC-AIDS
Architectural Consultants Pvt. Ltd.
Architects, Planners, Valuers, Designers, 305/306, MPJ Chambers, Old Mumbai - Pune Road, Wakdewadi, Khadki, Pune 411003.
Tel. No. 020 4007 9359