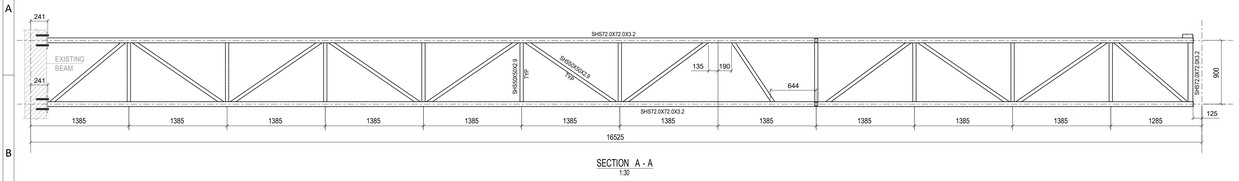
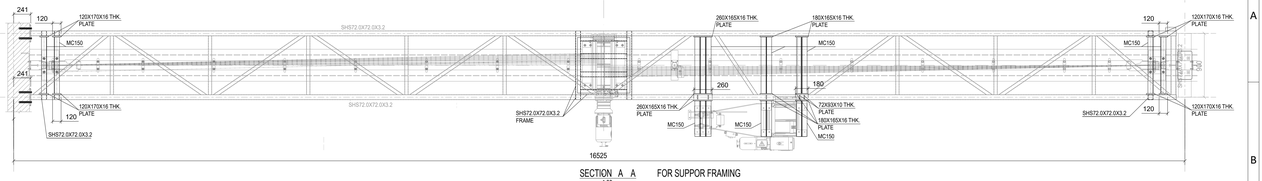
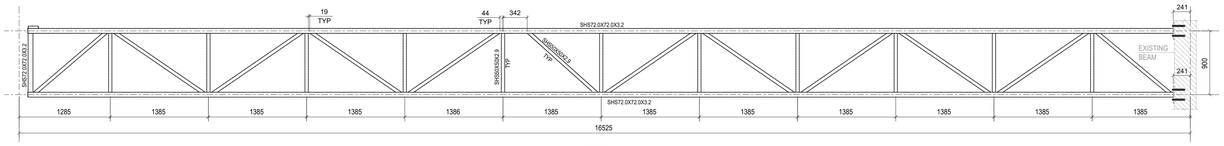
DWG.NO: SALT_1714_STR_01_R0



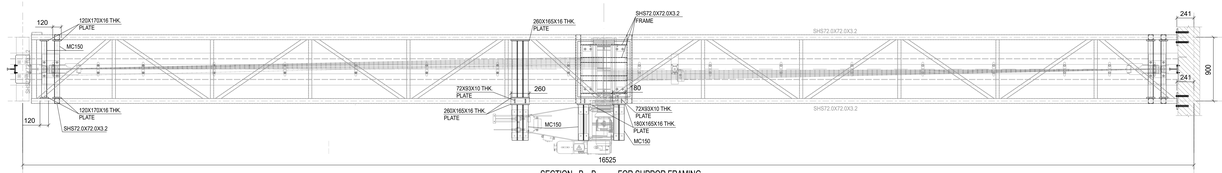

SECTION A - A
1:30



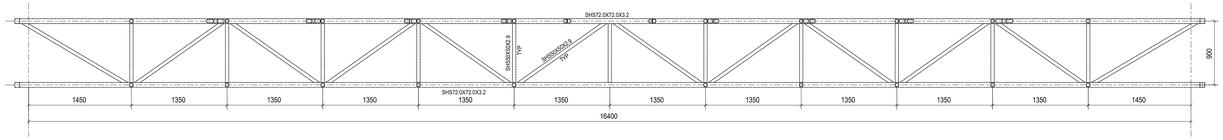

SECTION A A FOR SUPPOR FRAMING
1:30



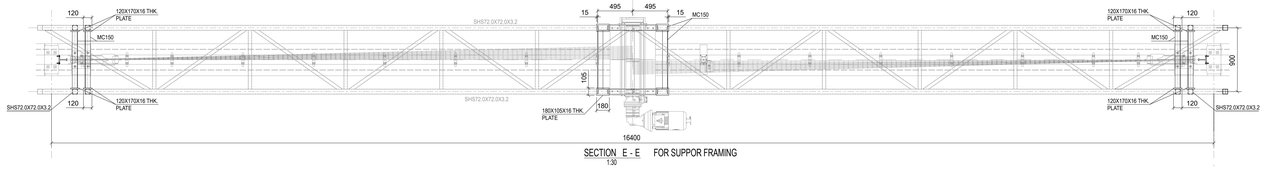

SECTION B - B
1:30



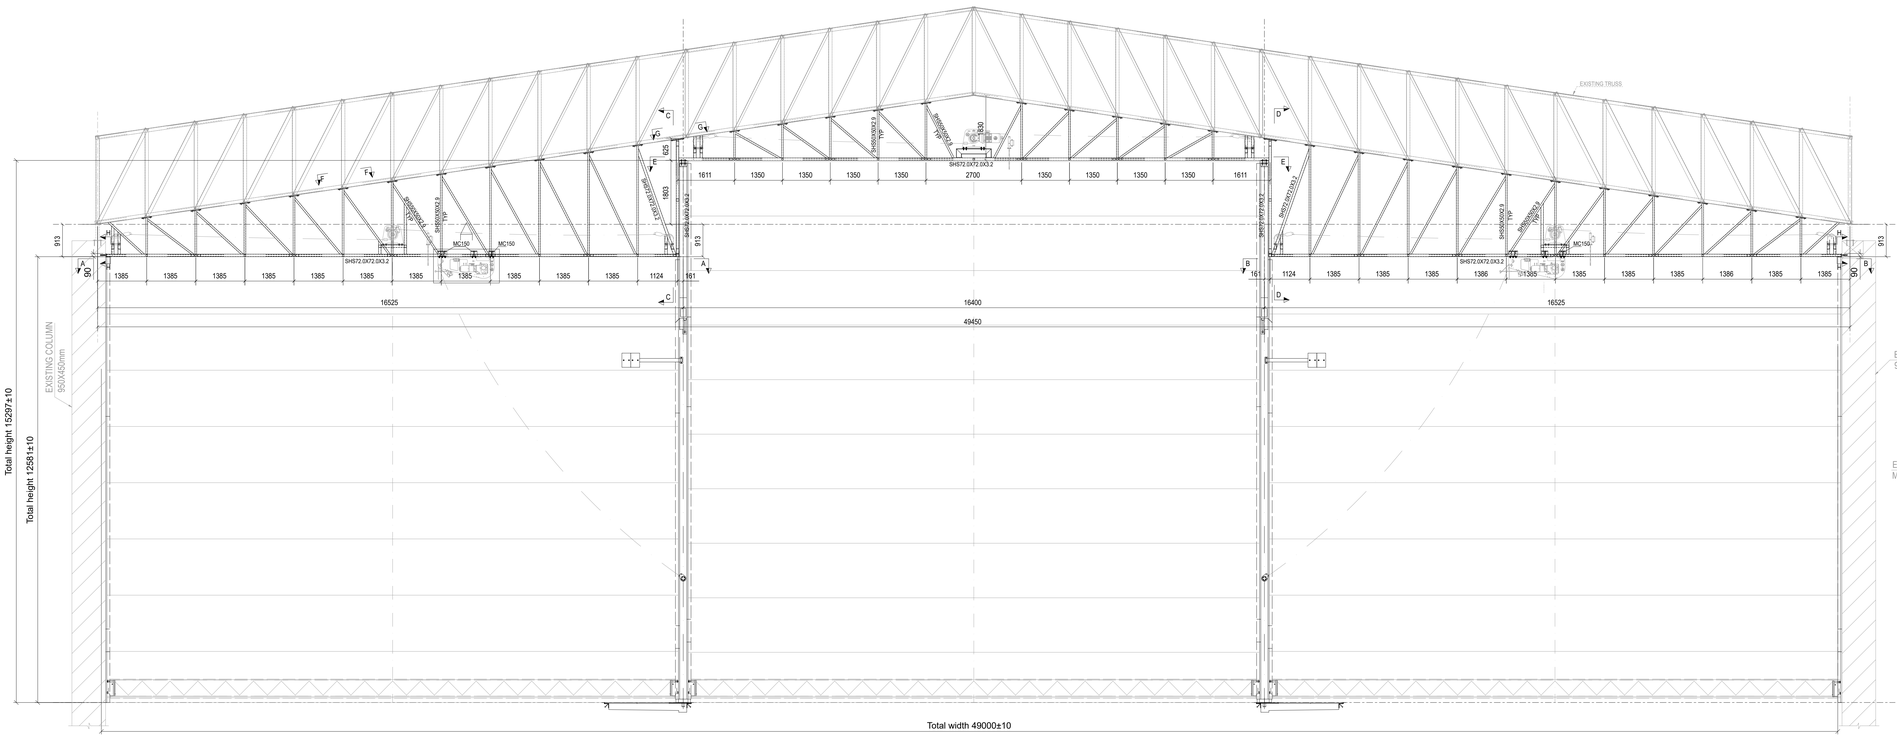

SECTION B - B FOR SUPPOR FRAMING
1:30



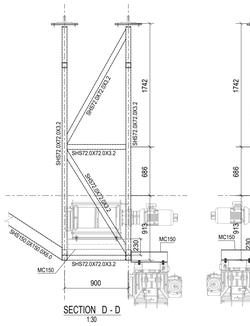

SECTION E - E
1:30



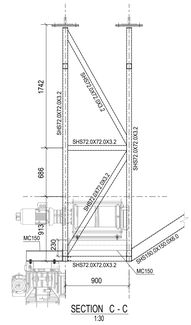

SECTION E - E FOR SUPPOR FRAMING
1:30



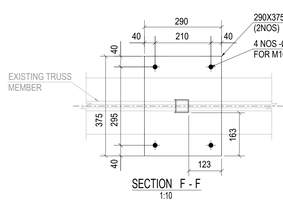

FRONT VIEW



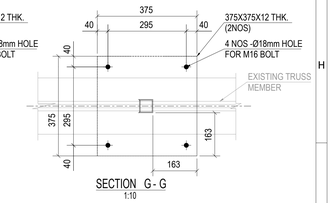

SECTION D - D
1:30



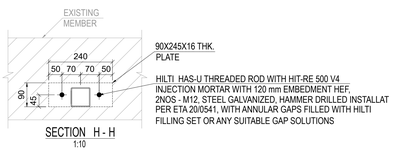

SECTION C - C
1:30



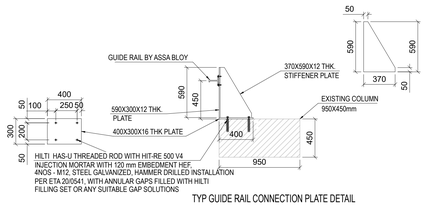

SECTION F - F
1:10




SECTION G - G
1:10




SECTION H - H
1:10




TYP GUIDE RAIL CONNECTION PLATE DETAIL

| REV.NO. | DESCRIPTION. | REV.DATE | DRAWN. | CHKD. | APPD. |
|---|---|---|---|---|---|
| 0 | | | | | |

DWG.TITLE :- STRUCTURAL DRAWING FOR DOOR FRAME

| | |
|---|---|
| PROJECT | |
| CLIENT | Cochin International Airport |
| SALT Design Services | SALT DESIGN SERVICES<br>4-PUSHKAR NIRZAR, SBI COLONY,<br>NEAR ICICI BANK, KOTHRUD, PUNE-411038. |

| | | |
|---|---|---|
| DRAWN :RRK | CHECKED : HAB | SCALE: 1:100 |
| APPROVED : HAB | JOB CODE. : 1714 | DATE: 08.07.2022 |
| DWG.NO: SALT_1714_STR_01_R0 | (SH-1OF1) | REV. - R0<br>SIZE. - A0 |

A1 [841 x 594]