



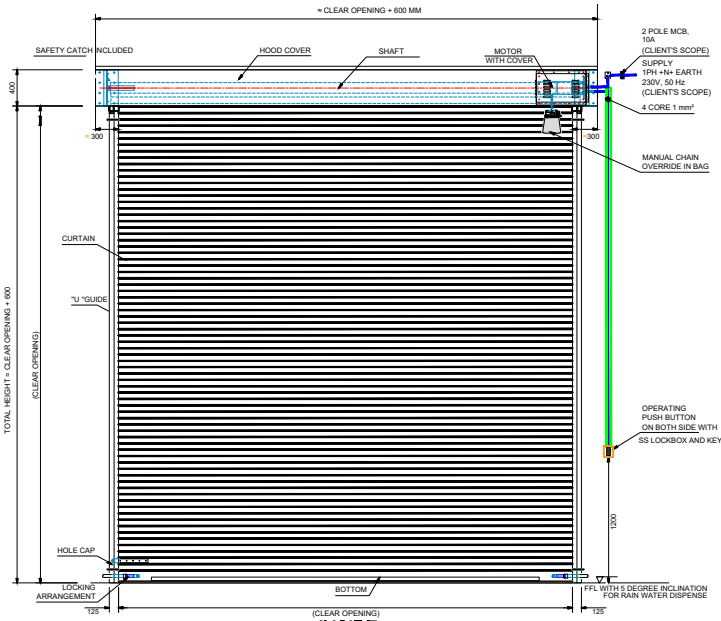

INSIDE

ELEVATION

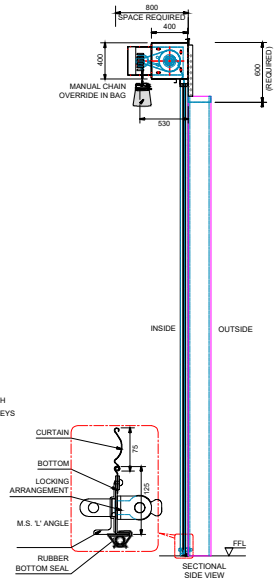

TECHNICAL SPECIFICATION:-

SR.	SPECIFICATION	DETAILS
1.	Description & Drive	Fire Rated Rolling Shutter
2.	Location Area	Inside/Out side
3.	Mounting Surface	Confirm by client
4.	Slat	GI Slat -97 mm Pitch 0.8mm/1.2mm Thick
5.	GI Guide Rails	"G" shaped
6.	Box Cover & Motor Cover	Galvanized steel 0.8 mm thick
7.	Standard Motor	1P/230V/50HZ Motor
8.	Push Botton	3 Way Push Baton on Single Side

SHUTTER SIZES :-

SR.	CLEAR WIDTH	CLEAR HEIGHT	QTY.
01	2000	4000	01
02	5000	5000	01

This drawing & designing is the property of NIHVA TECHNOLOGIES. Not to be sold or copied to any other concern

TITLE :-
MOTORISED ROLLING SHUTTER

NIHVA TECHNOLOGIES PVT. LTD. PUNE
Tel : 020 66304033
Email:- info@nihva.com
Website:- www.nihva.com

	NAME	DATE
DRAWN	B.S.	06/08/2025
CHECK	V.T.	06/08/2025
APPROVAL	V.T.	06/08/2025

CLIENT - INDOSOL

PROJECT -FIRE RATED ROLLING SHUTTER

DWG. NO. : NIHVA-23-24-CLT-102 | REV-00

SCALE: NTS | WT: | SHEET: 01 OF 01

ALL DIMENSION ARE IN mm

If any queries contact : design@nihva.com