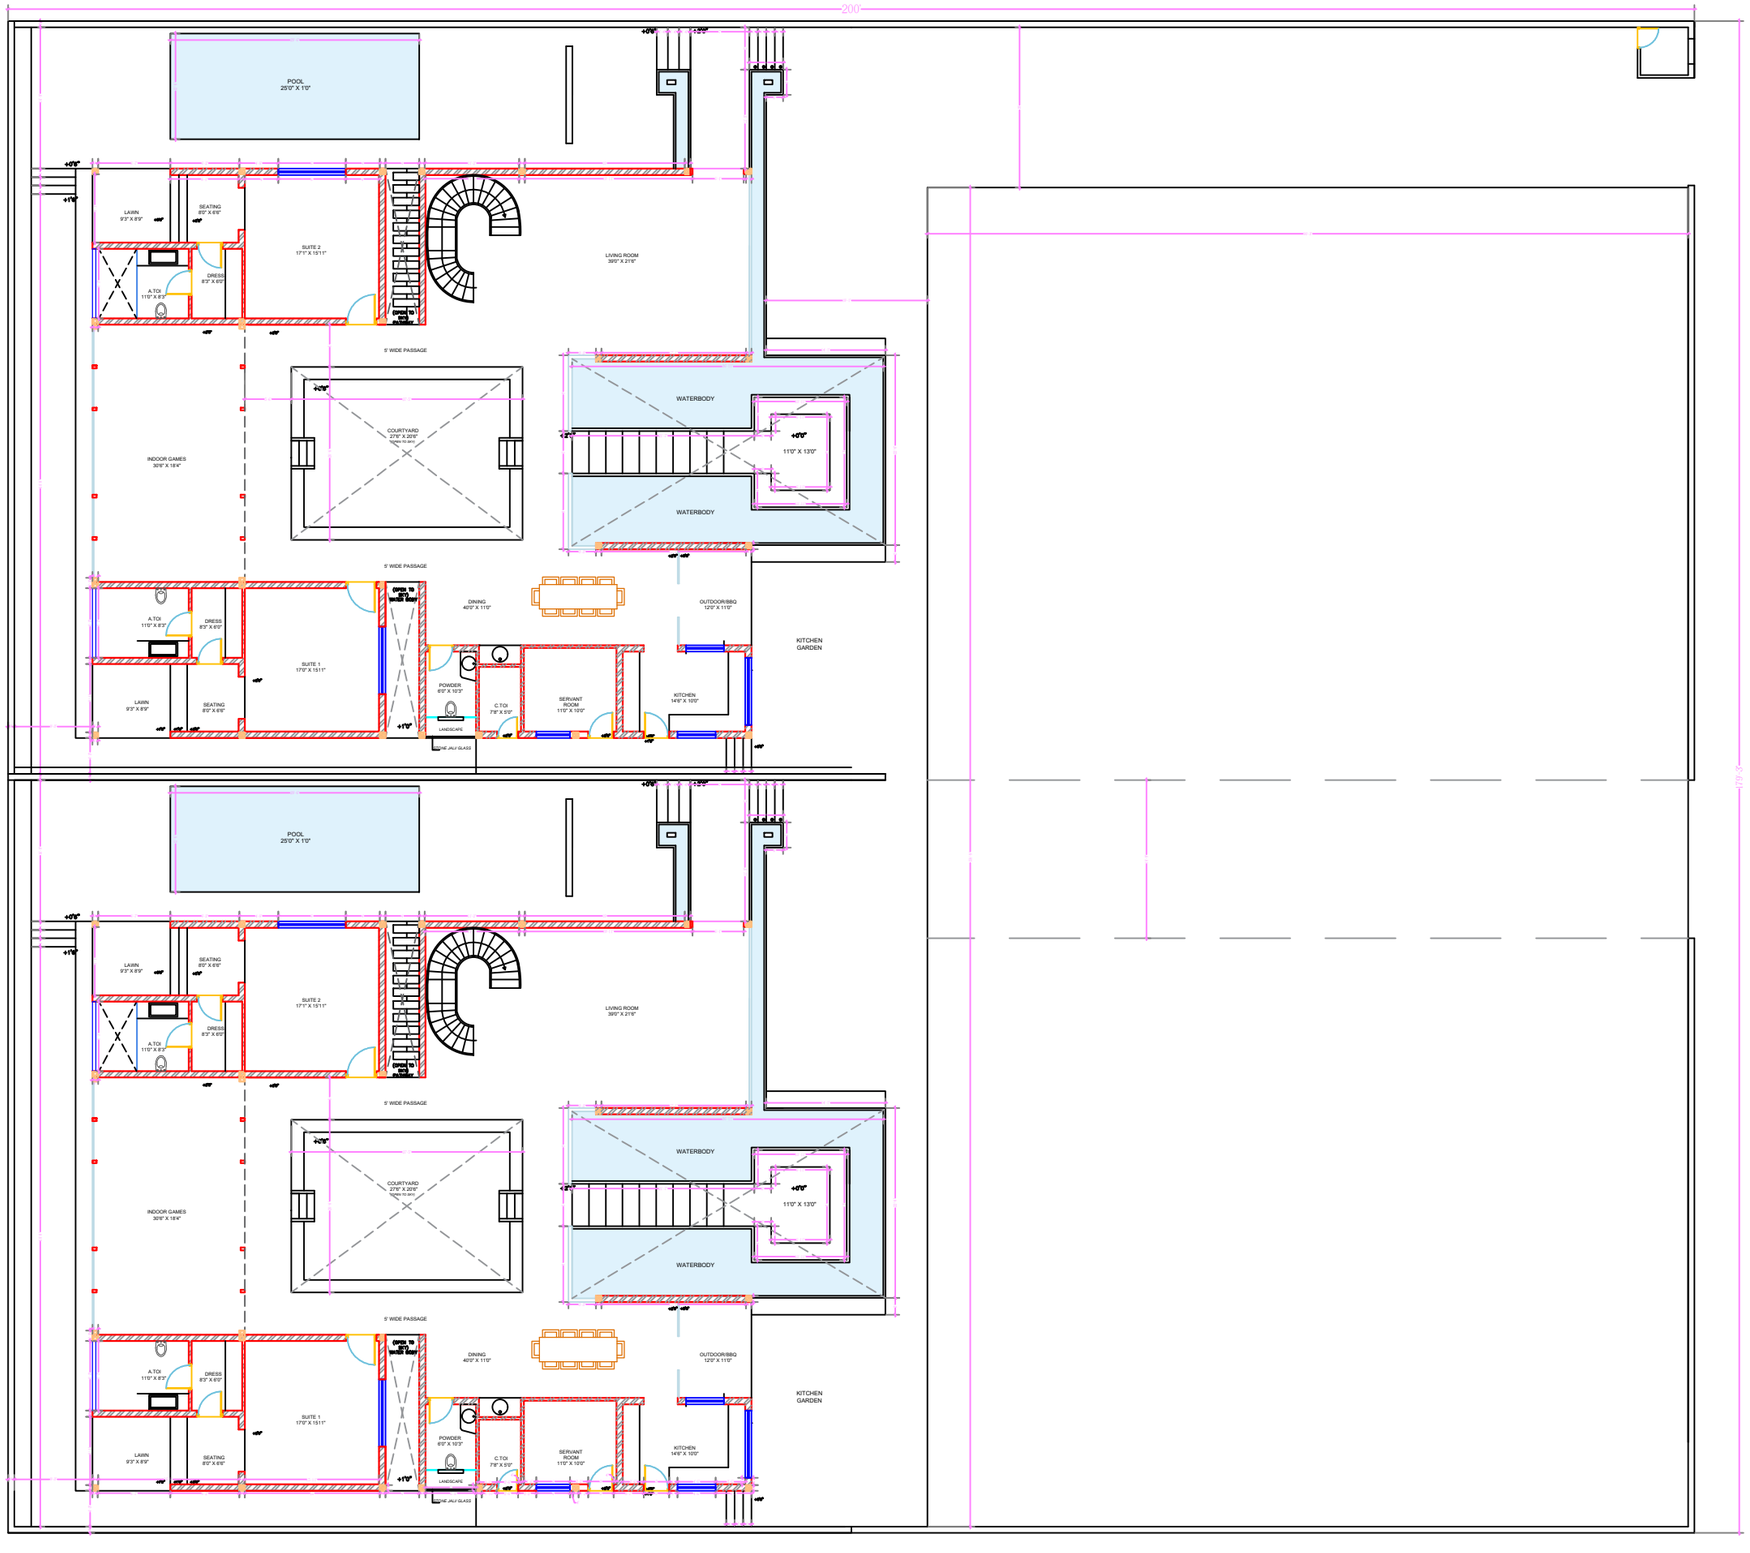


note:

Any unauthorised review, use, disclosure, dissemination, forwarding, printing or copying of this drawing or any action taken in reliance on this drawing is strictly prohibited and may be unlawful.

note:

ALL DIMENSIONS IN FEET AND INCHES

dwg no.:	Drawing Name
01	GROUND FLOOR BRICKWORK

LEGEND

- 9" BRICKWALL
- 4" BRICKWALL
- COLUMN
- WINDOW
- DOOR
- X'X" DIMENSION

dwg no.:

date: 26-03-2023

client:
Mr.Soni and Mr.Malu

designer:
Ar. Vinaybushan Bung
ID. Shubham Bung

project:
Residential

VINAY SHUBHAM ARCHITECTURAL STUDIO