
JACOBS®

DO NOT SCALE

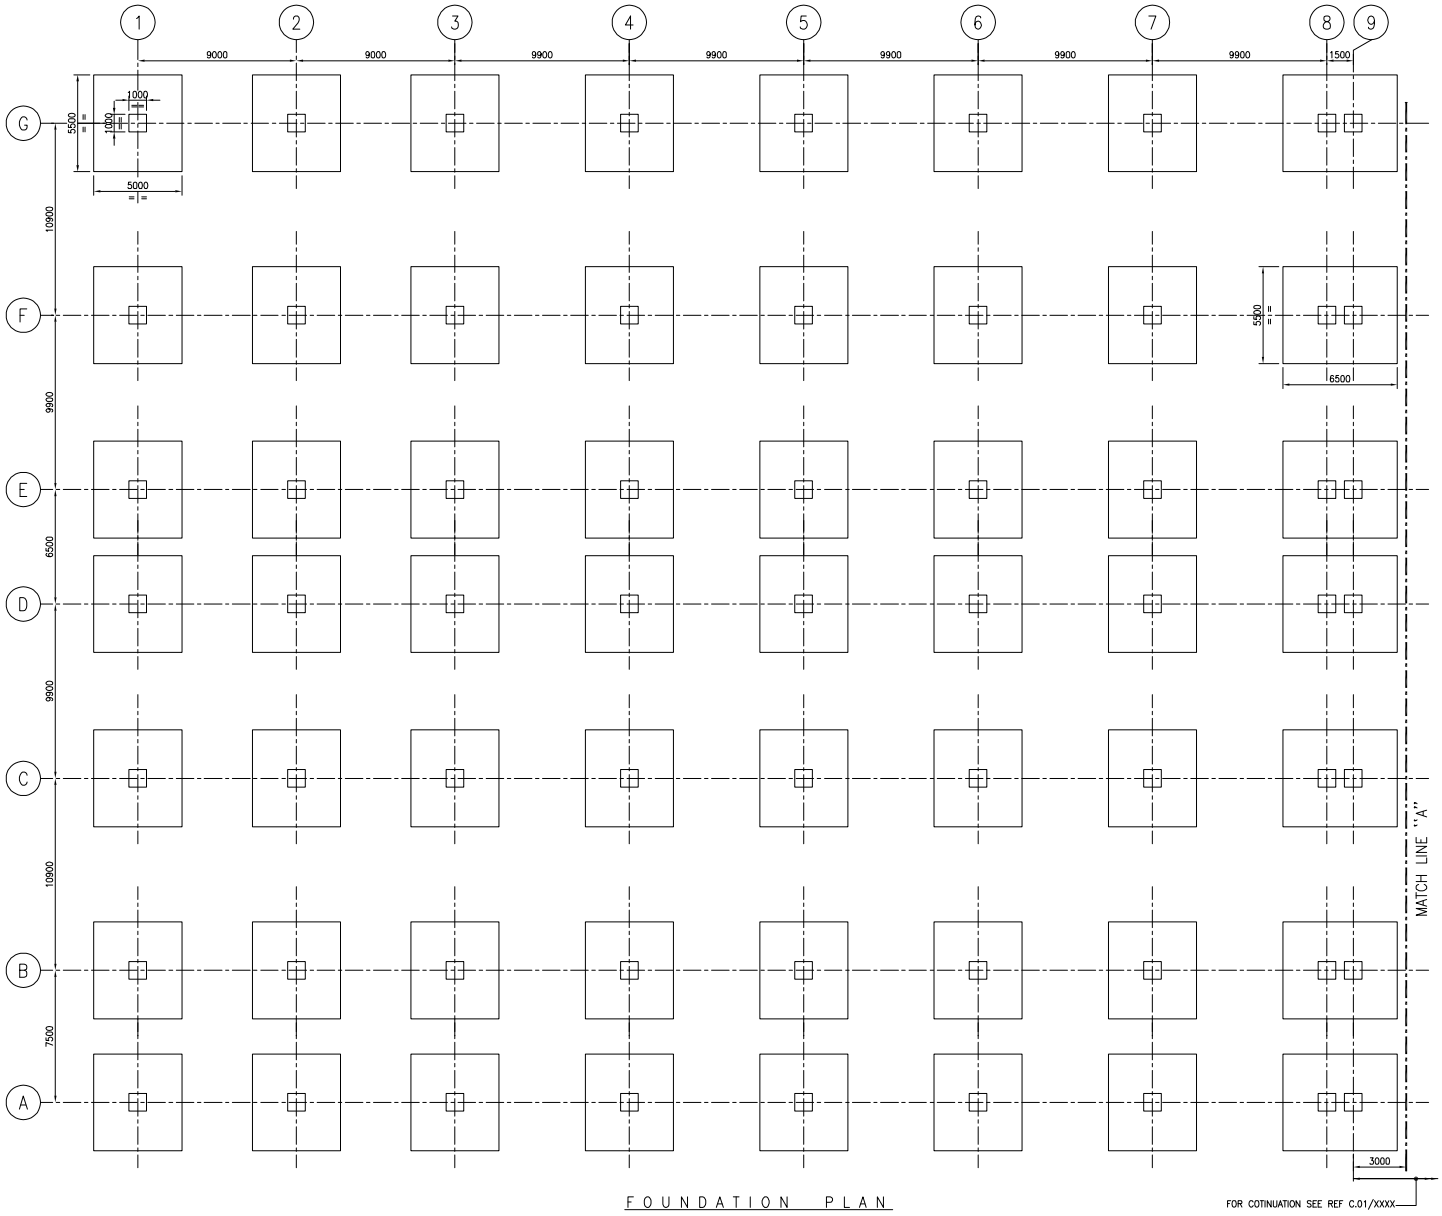

FOUNDATION PLAN

REF NORTH

FOR TENDERING PURPOSE

REV. NO.	REVISION DESCRIPTION	DRAWN	CHK	APPROVED	CLIENT APPR.	DATE
–	–	–	–	–	–	
–	–	–	–	–	–	
–	–	–	–	–	–	
–	–	–	–	–	–	
–	–	–	–	–	–	

CLIENT

ADITYA BIRLA GRASIM

GRASIM CELLULOSIC
(A UNIT OF GRASIM INDUSTRIES LTD.)
VILAYAT, BHARUCH (GUJRAT)

EDEP CONSULTANT

MOVIN
MOVIN ENGINEERING CO., LTD

ADDRESS :-
–
–
–
–
–

THIS DRAWING AND/OR ITS CONTENTS, INFORMATION, AND PRINCIPLES OF DESIGN ARETHE EXCLUSIVE PROPERTY OF GRASIM CELLULOSIC, INDIA AND IS SUBMITTED TO YOU WITH THE AGREEMENT THAT IT IS NOT TO BE REPRODUCED IN ANY MANNER, COPIED, OR MODIFIED, NOR IS IT TO BE RELAYED IN PART OR IN WHOLE TO ANY OTHER FIRM OR INDIVIDUAL FOR ANY OTHER PROJECT EXCEPT BY WRITTEN AGREEMENT WITH GRASIM CELLULOSIC, INDIA.

JACOBS

JACOBS ENGINEERING INDIA PRIVATE LIMITED.
JACOBS HOUSE, RAMKRISHNA MANDIR ROAD,
KONDIVITA, ANDHERI (EAST), MUMBAI – 400059
TEL. +91-22-2681 2000


A MEMBER OF THE JACOBS ENGINEERING GROUP, INC.

GRASIM CELLULOSIC
VSF EXPANSION PROJECT
AUXILLIARY BUILDING
L/O OF FDN BETWEEN GRIDS 1-9 & A-G

PROJ.NO.	DRAWING NO.			REV
44AC6500	44AC6500-000-C.01-0001-A1			A
DATE	FILE NAME	DRAWING SCALE	PLOT SCALE	DRAWN BY
06.06.18	44AC6500000C010001A1A	1:150	1:1	SBK

A1

DO NOT SCALE

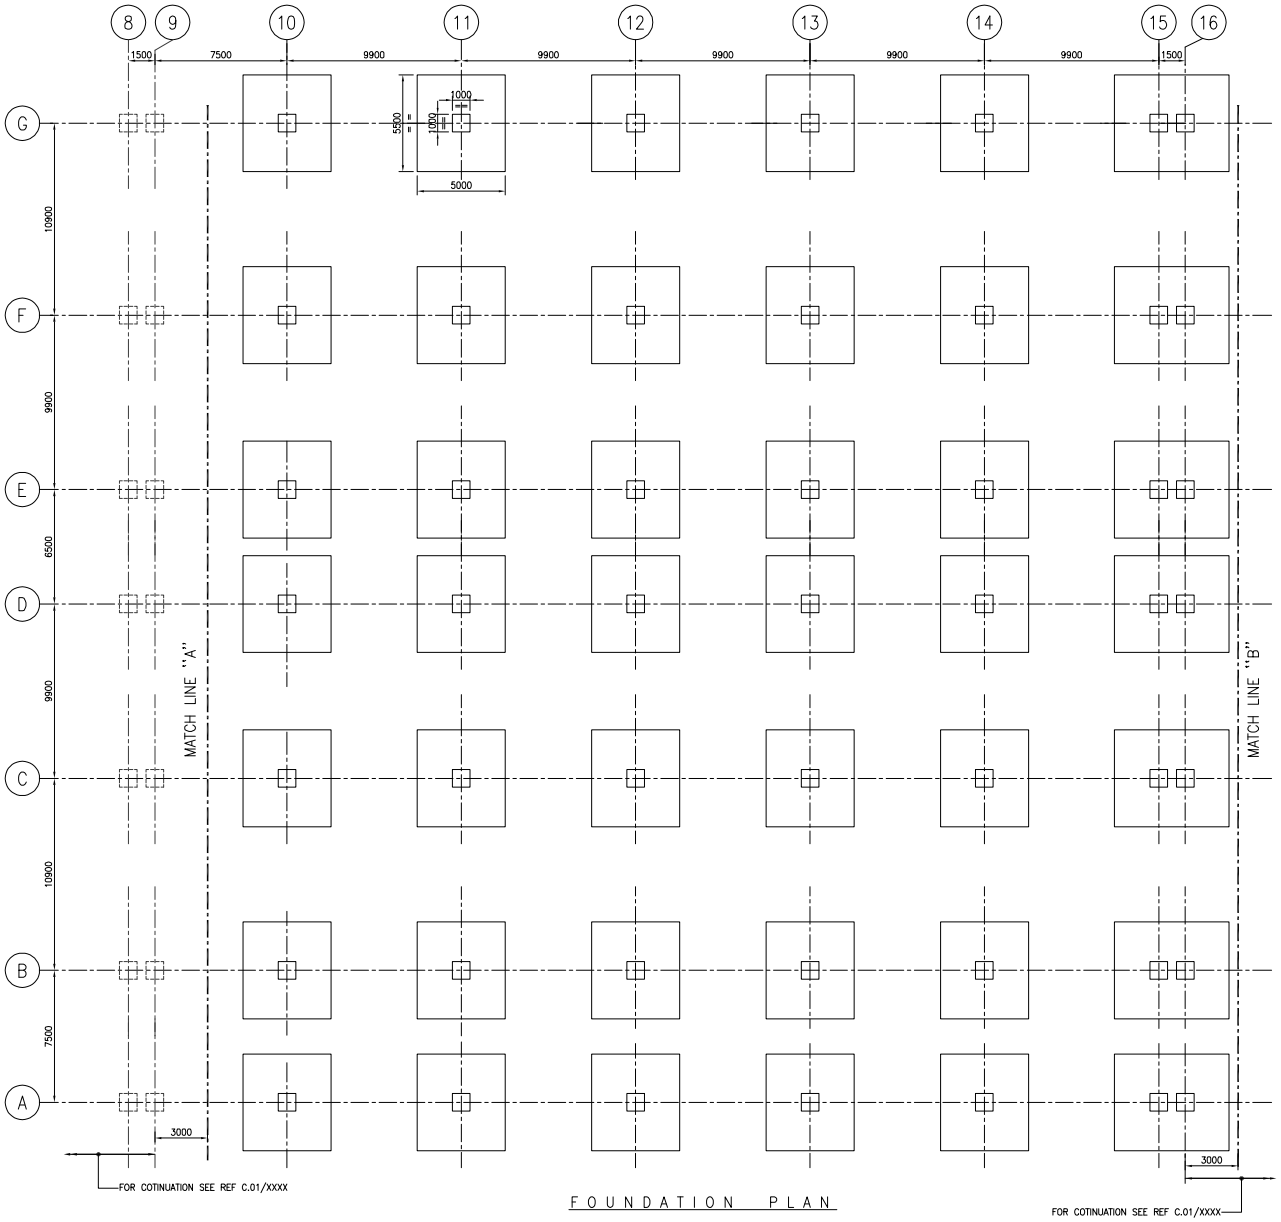

FOUNDATION PLAN

REF NORTH

FOR TENDERING PURPOSE

REV. NO.	REVISION DESCRIPTION	DRAWN	CHK	APPROVED	CLIENT APPR.	DATE
–	–	–	–	–	–	
–	–	–	–	–	–	
–	–	–	–	–	–	
–	–	–	–	–	–	
–	–	–	–	–	–	

CLIENT

ADITYA BIRLA GRASIM

GRASIM CELLULOSIC
(A UNIT OF GRASIM INDUSTRIES LTD.)
VILAYAT, BHARUCH (GUJRAT)

BDEP CONSULTANT

MOVIN
MOVIN ENGINEERING CO., LTD

ADDRESS :-
–
–
–
–

THIS DRAWING AND/OR ITS CONTENTS, INFORMATION, AND PRINCIPLES OF DESIGN ARETHE EXCLUSIVE PROPERTY OF GRASIM CELLULOSIC, INDIA AND IS SUBMITTED TO YOU WITH THE AGREEMENT THAT IT IS NOT TO BE REPRODUCED IN ANY MANNER, COPIED, OR MODIFIED, NOR IS IT TO BE RELAYED IN PART OR IN WHOLE TO ANY OTHER FIRM OR INDIVIDUAL FOR ANY OTHER PROJECT EXCEPT BY WRITTEN AGREEMENT WITH GRASIM CELLULOSIC, INDIA.

JACOBS

JACOBS ENGINEERING INDIA PRIVATE LIMITED.
JACOBS HOUSE, RAMKRISHNA MANDIR ROAD,
KONDIVITA, ANDHERI (EAST), MUMBAI – 400059
TEL. +91-22-2681 2000


A MEMBER OF THE JACOBS ENGINEERING GROUP, INC.

GRASIM CELLULOSIC
VSF EXPANSION PROJECT
AUXILLIARY BUILDING
L/O OF FDN BETWEEN GRIDS 10-16 & A-G

PROJ.NO.	DRAWING NO.		REV
44AC6500	44AC6500-000-C.01-0002-A1		A
DATE	FILE NAME	DRAWING SCALE / PLOT SCALE	DRAWN BY
06.06.18	44AC6500000C010002A1A	1:150 / 1:1	SBK

A1

DO NOT SCALE

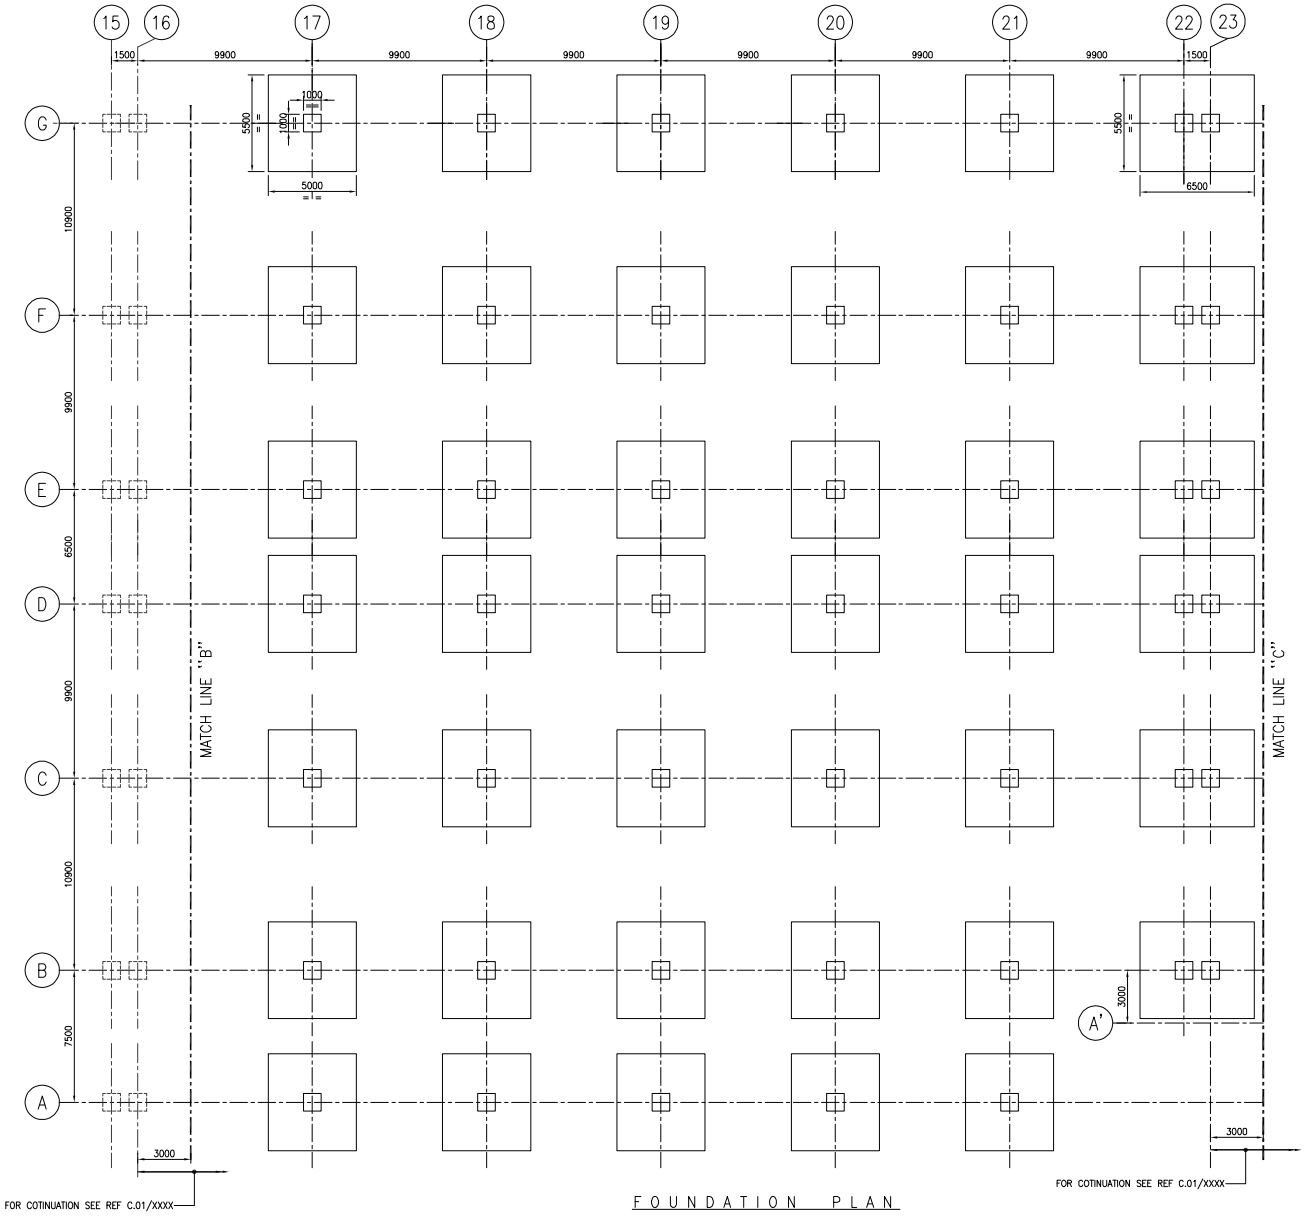

FOUNDATION PLAN

REF NORTH

FOR TENDERING PURPOSE

REV. NO.	REVISION DESCRIPTION	DRAWN	CHK	APPROVED	CLIENT APPR.	DATE
–	–	–	–	–	–	
–	–	–	–	–	–	
–	–	–	–	–	–	
–	–	–	–	–	–	
–	–	–	–	–	–	

CLIENT

ADITYA BIRLA GRASIM

GRASIM CELLULOSIC
(A UNIT OF GRASIM INDUSTRIES LTD.)
VILAYAT, BHARUCH (GUJRAT)

BDEP CONSULTANT

MOVIN
MOVIN ENGINEERING CO., LTD

ADDRESS :-
–
–
–
–

THIS DRAWING AND/OR ITS CONTENTS, INFORMATION, AND PRINCIPLES OF DESIGN ARETHE EXCLUSIVE PROPERTY OF GRASIM CELLULOSIC, INDIA AND IS SUBMITTED TO YOU WITH THE AGREEMENT THAT IT IS NOT TO BE REPRODUCED IN ANY MANNER, COPIED, OR MODIFIED, NOR IS IT TO BE RELAYED IN PART OR IN WHOLE TO ANY OTHER FIRM OR INDIVIDUAL FOR ANY OTHER PROJECT EXCEPT BY WRITTEN AGREEMENT WITH GRASIM CELLULOSIC, INDIA.

JACOBS

JACOBS ENGINEERING INDIA PRIVATE LIMITED.
JACOBS HOUSE, RAMKRISHNA MANDIR ROAD,
KONDIVITA, ANDHERI (EAST), MUMBAI – 400059
TEL. +91-22-2681 2000


A MEMBER OF THE JACOBS ENGINEERING GROUP, INC.

GRASIM CELLULOSIC
VSF EXPANSION PROJECT
AUXILLIARY BUILDING
L/O OF FDN BETWEEN GRIDS 17-23 & A-G

PROJ.NO.	DRAWING NO.		REV
44AC6500	44AC6500-000-C.01-0003-A1		A
DATE	FILE NAME	DRAWING SCALE / PLOT SCALE	DRAWN BY
06.06.18	44AC6500000C010003A1A	1:150 / 1:1	SBK

A1

DO NOT SCALE

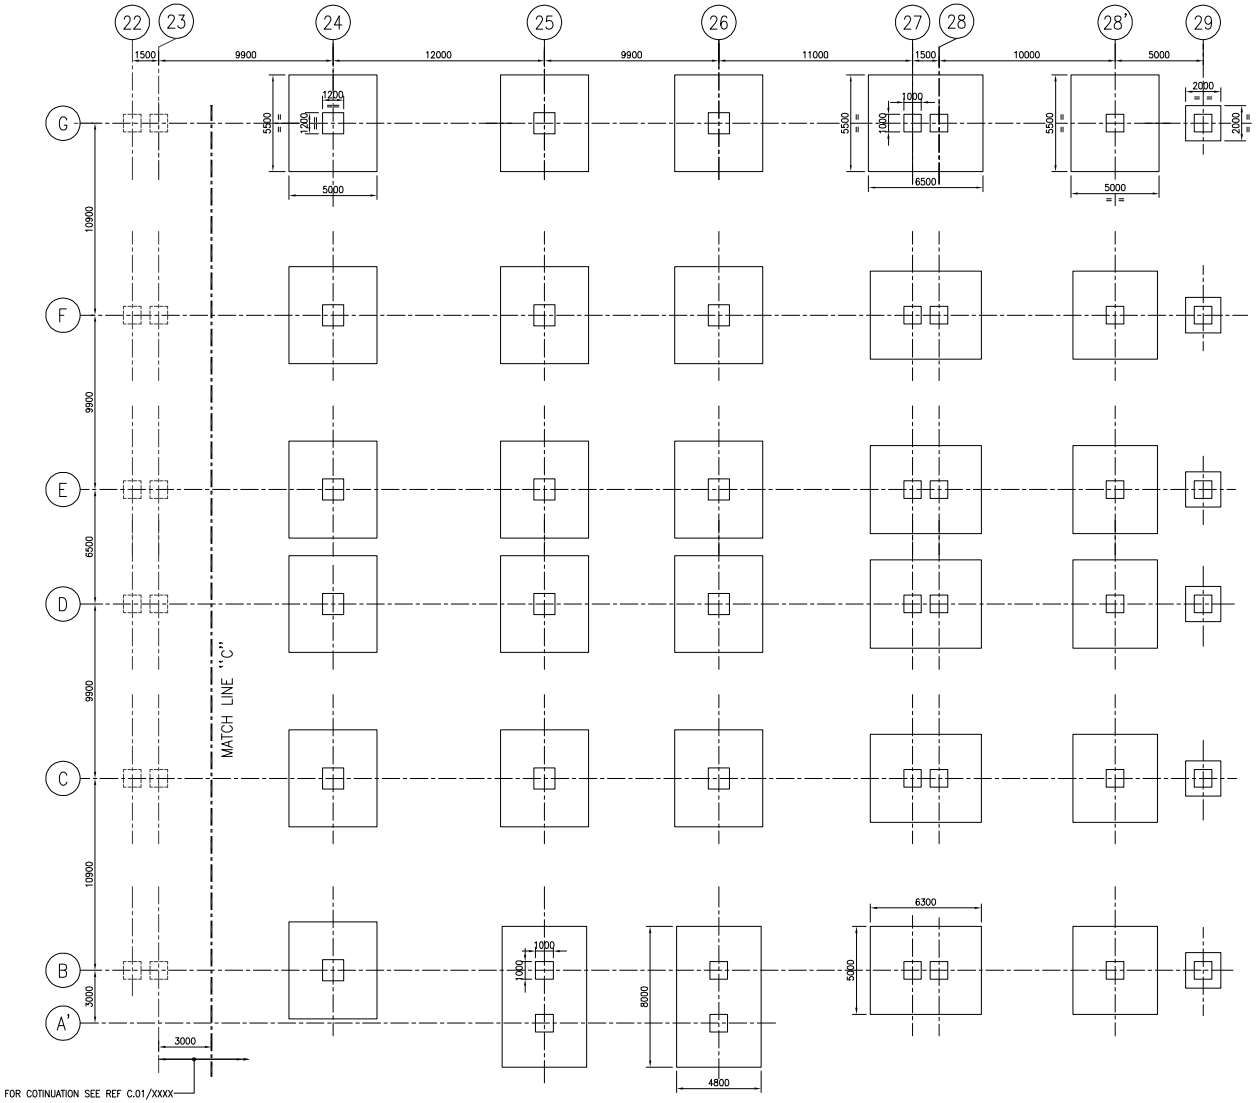

FOUNDATION PLAN

REF NORTH

FOR TENDERING PURPOSE

REV. NO.	REVISION DESCRIPTION	DRAWN	CHK	APPROVED	CLIENT APPR.	DATE
–	–	–	–	–	–	
–	–	–	–	–	–	
–	–	–	–	–	–	
–	–	–	–	–	–	
–	–	–	–	–	–	

CLIENT

ADITYA BIRLA GRASIM

GRASIM CELLULOSIC
(A UNIT OF GRASIM INDUSTRIES LTD.)
VILAYAT, BHARUCH (GUJRAT)

BDEP CONSULTANT

MOVIN
MOVIN ENGINEERING CO., LTD

ADDRESS :-
–
–
–
–

THIS DRAWING AND/OR ITS CONTENTS, INFORMATION, AND PRINCIPLES OF DESIGN ARETHE EXCLUSIVE PROPERTY OF GRASIM CELLULOSIC, INDIA AND IS SUBMITTED TO YOU WITH THE AGREEMENT THAT IT IS NOT TO BE REPRODUCED IN ANY MANNER, COPIED, OR MODIFIED, NOR IS IT TO BE RELAYED IN PART OR IN WHOLE TO ANY OTHER FIRM OR INDIVIDUAL FOR ANY OTHER PROJECT EXCEPT BY WRITTEN AGREEMENT WITH GRASIM CELLULOSIC, INDIA.

JACOBS


JACOBS ENGINEERING INDIA PRIVATE LIMITED.
JACOBS HOUSE, RAMKRISHNA MANDIR ROAD,
KONDIVITA, ANDHERI (EAST), MUMBAI – 400059
TEL. +91-22-2681 2000

A MEMBER OF THE JACOBS ENGINEERING GROUP, INC.


GRASIM CELLULOSIC
VSF EXPANSION PROJECT
AUXILLIARY BUILDING
L/O OF FDN BETWEEN GRIDS 24-29 & A'-G

PROJ.NO.	DRAWING NO.		REV
44AC6500	44AC6500-000-C.01-0004-A1		A
DATE	FILE NAME	DRAWING SCALE / PLOT SCALE	DRAWN BY
06.06.18	44AC6500000C010004A1A	1:150 / 1:1	SBK

A1

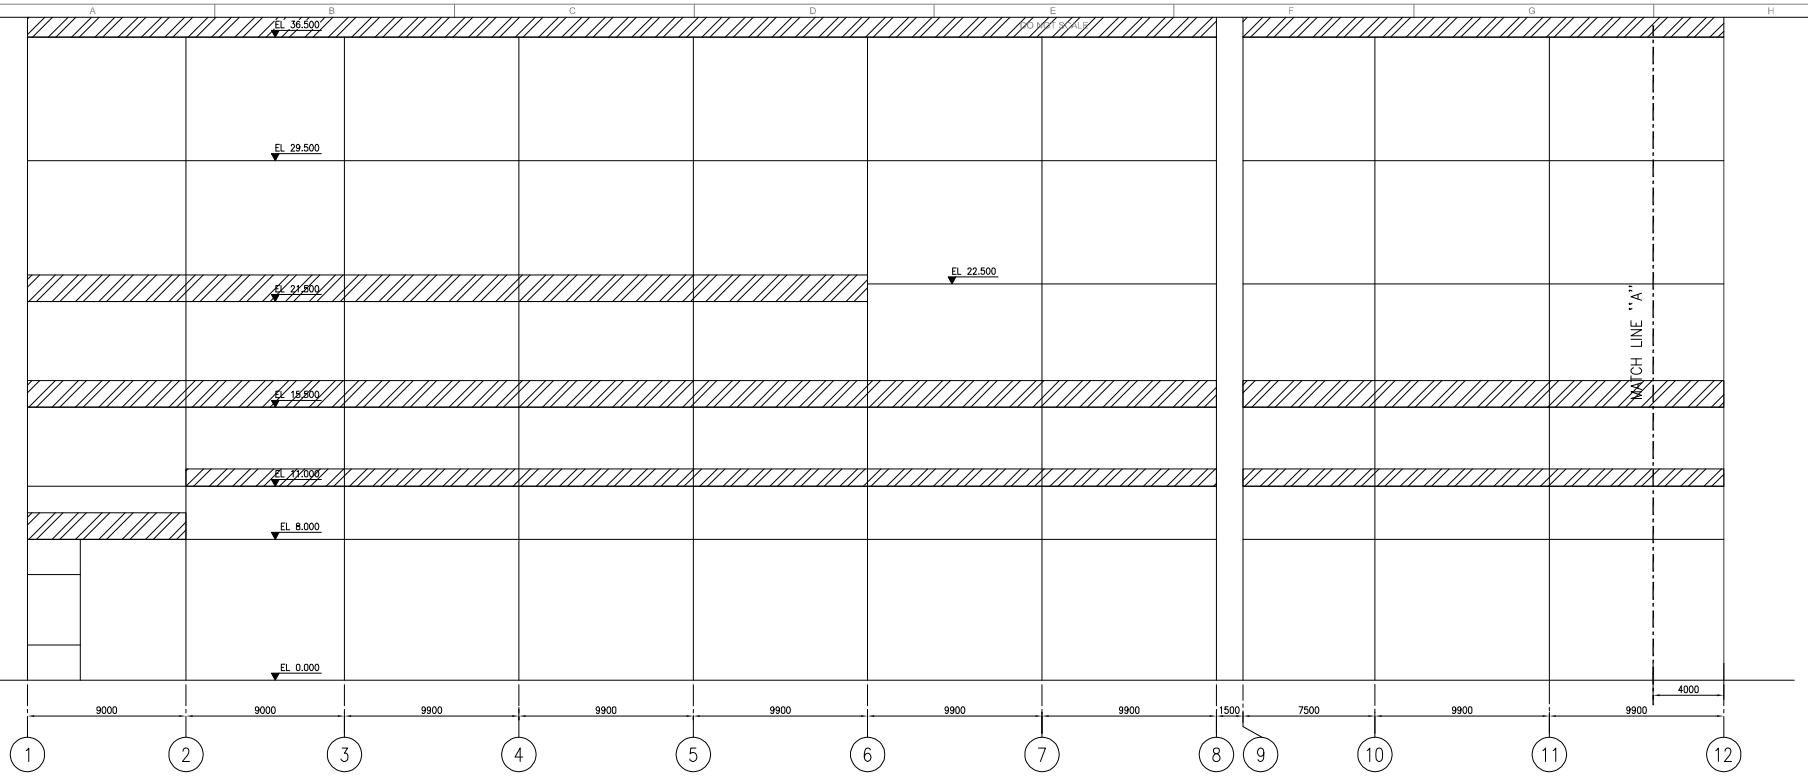

ON GRID A

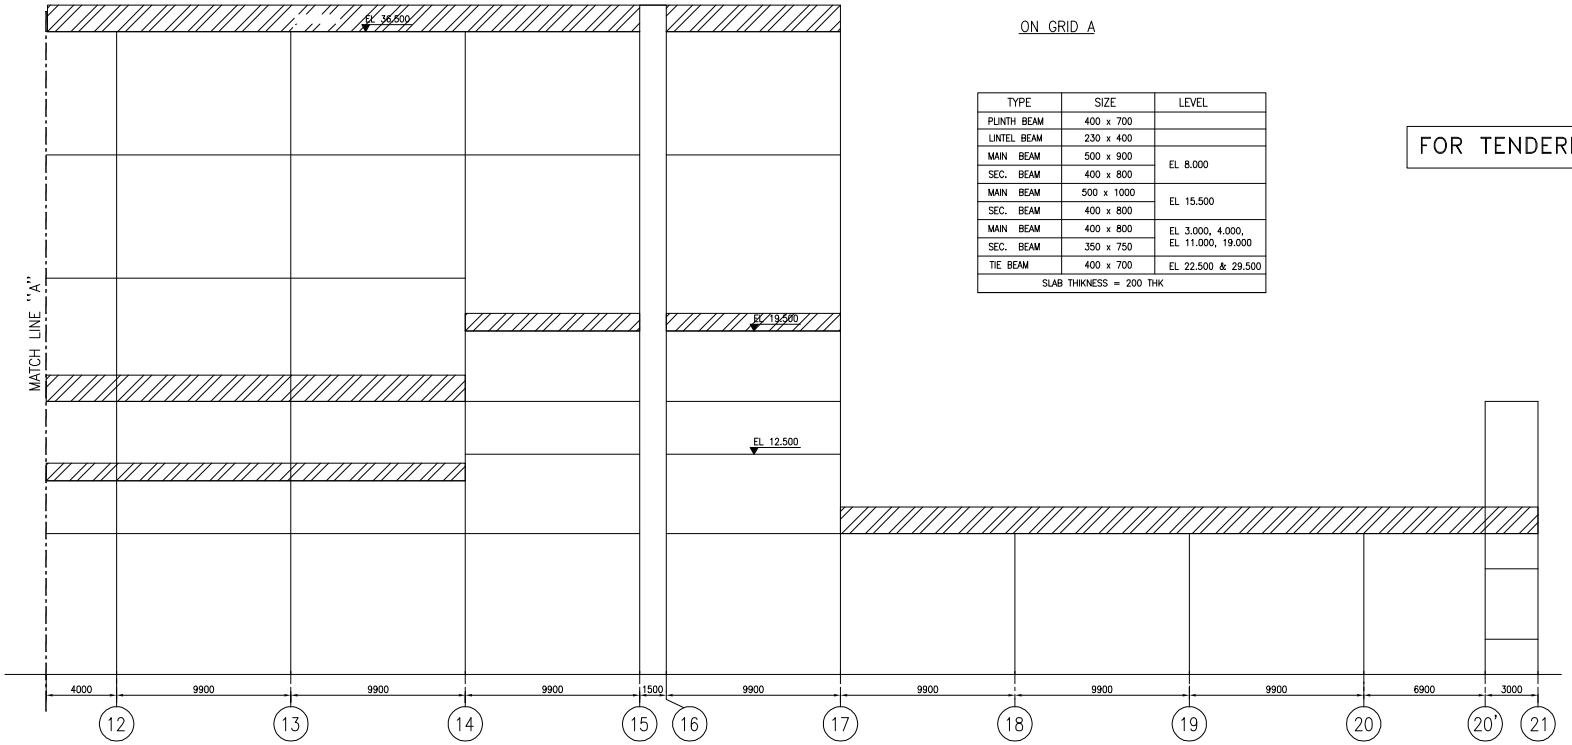

TYPE	SIZE	LEVEL
PLINTH BEAM	400 x 700	
LINTEL BEAM	230 x 400	
MAIN BEAM	500 x 900	EL 8.000
SEC. BEAM	400 x 800	
MAIN BEAM	500 x 1000	EL 15.500
SEC. BEAM	400 x 800	
MAIN BEAM	400 x 800	EL 3.000, 4.000, EL 11.000, 19.000
SEC. BEAM	350 x 750	
TIE BEAM	400 x 700	EL 22.500 & 29.500
SLAB THIKNESS = 200 THK		

FOR TENDERING PURPOSE

REV. NO.	REVISION DESCRIPTION	DRAWN	CHK	APPROVED	CLIENT APPR.	DATE
–	–	–	–	–	–	–
–	–	–	–	–	–	–
–	–	–	–	–	–	–
–	–	–	–	–	–	–
–	–	–	–	–	–	–

CLIENT

ADITYA BIRLA GRASIM

GRASIM CELLULOSIC
(A UNIT OF GRASIM INDUSTRIES LTD.)
VILAYAT, BHARUCH (GUJRAT)

BDEP CONSULTANT:

MOVIN
MOVIN ENGINEERING CO., LTD

ADDRESS :-
–
–
–
–
–

THIS DRAWING AND/OR ITS CONTENTS, INFORMATION, AND PRINCIPLES OF DESIGN ARETHE EXCLUSIVE PROPERTY OF GRASIM CELLULOSIC, INDIA AND IS SUBMITTED TO YOU WITH THE AGREEMENT THAT IT IS NOT TO BE REPRODUCED IN ANY MANNER, COPIED, OR MODIFIED, NOR IS IT TO BE RELAYED IN PART OR IN WHOLE TO ANY OTHER FIRM OR INDIVIDUAL FOR ANY OTHER PROJECT EXCEPT BY WRITTEN AGREEMENT WITH GRASIM CELLULOSIC, INDIA.

JACOBS

JACOBS ENGINEERING INDIA PRIVATE LIMITED.
JACOBS HOUSE, RAMKRISHNA MANDIR ROAD,
KONDIVITA, ANDHERI (EAST), MUMBAI – 400059
TEL. +91-22-2681 2000


A MEMBER OF THE JACOBS ENGINEERING GROUP, INC.

GRASIM CELLULOSIC
VSF EXPANSION PROJECT
AUXILLIARY AREA
ELEVATION ON GRID A


PROJ.NO.	DRAWING NO.		REV
44AC6500	44AC6500-000-C.01-XXXX-A1		A
DATE	FILE NAME	DRAWING SCALE / PLOT SCALE	DRAWN BY
29.05.18	44AC6500000C01XXXXA1A	1:150 / 1:1	SBK

A1

DO NOT SCALE

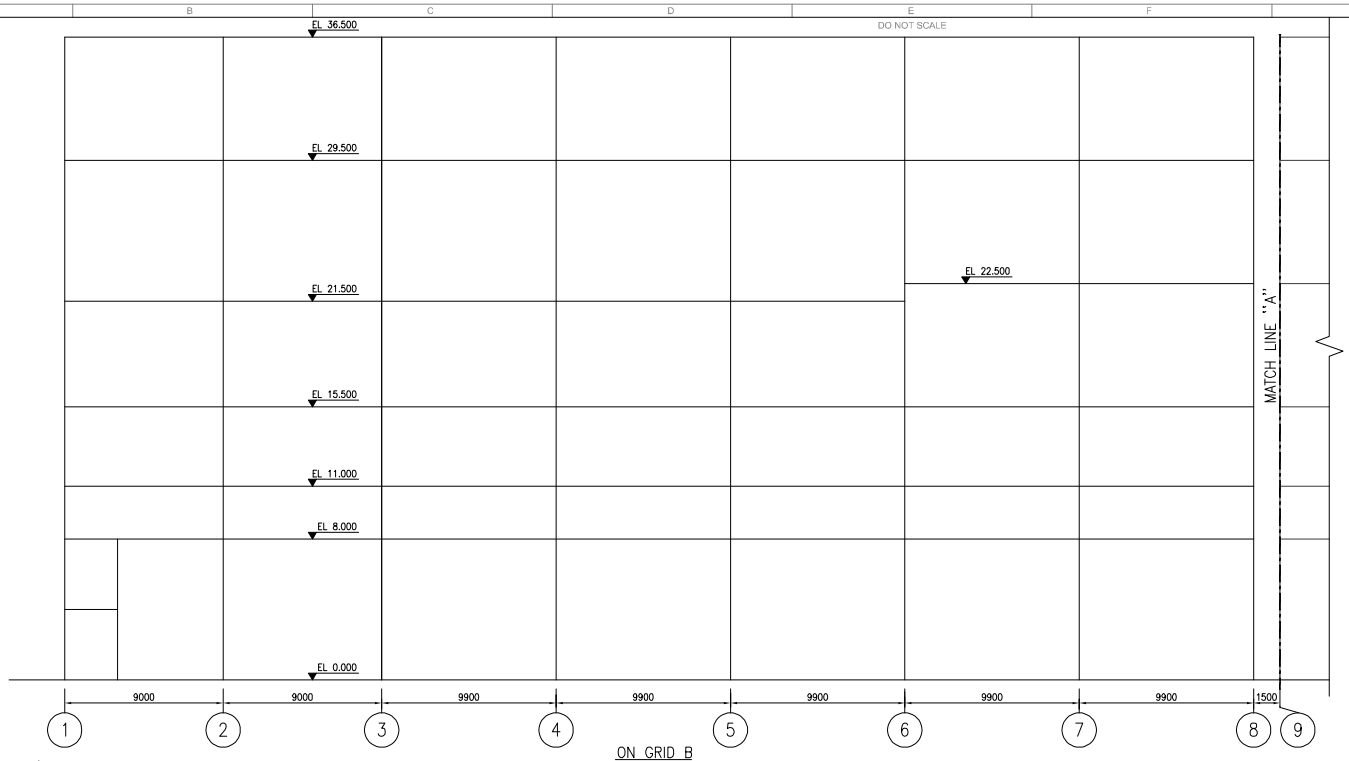

ON GRID B

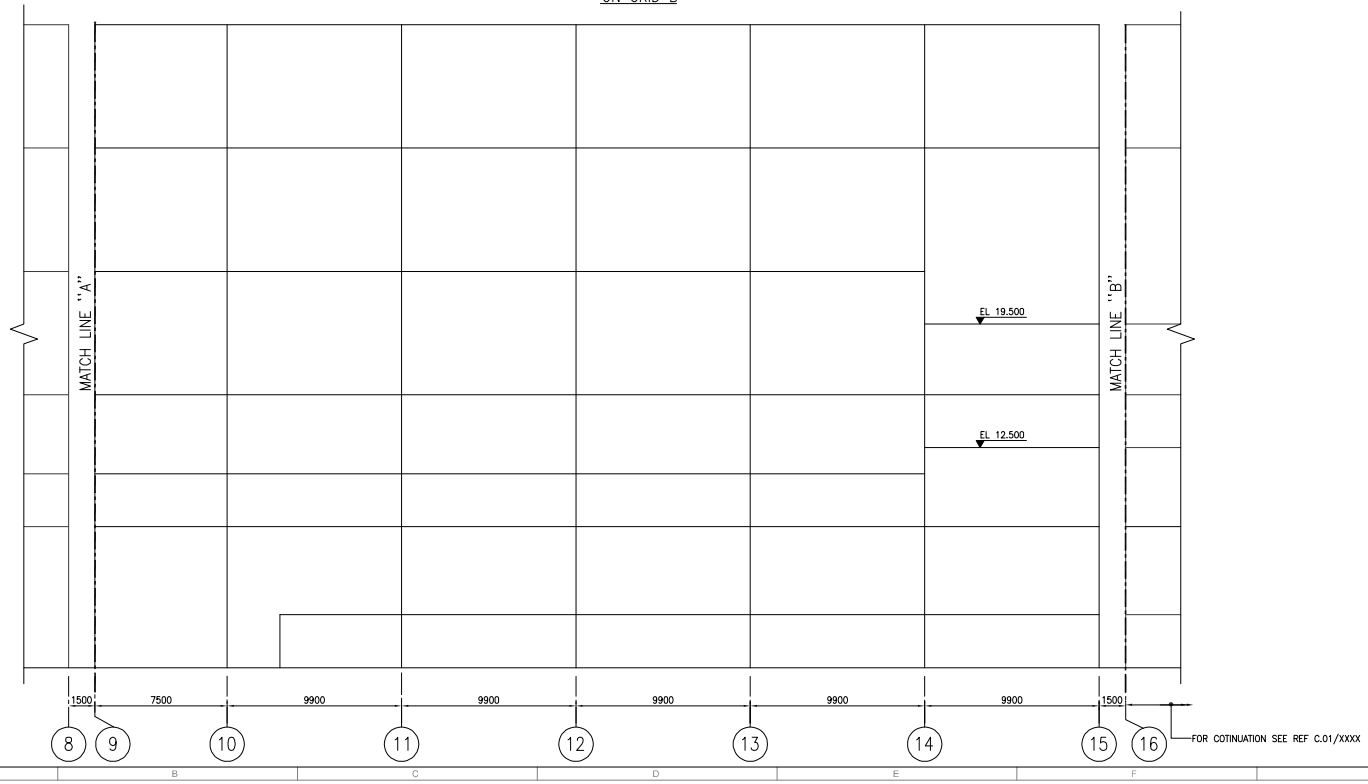

FOR TENDERING PURPOSE

REV. NO.	REVISION DESCRIPTION	DRAWN	CHK	APPROVED	CLIENT APPR.	DATE
–	–	–	–	–	–	–
–	–	–	–	–	–	–
–	–	–	–	–	–	–
–	–	–	–	–	–	–
–	–	–	–	–	–	–

CLIENT

ADITYA BIRLA GRASIM

GRASIM CELLULOSIC
(A UNIT OF GRASIM INDUSTRIES LTD.)
VILAYAT, BHARUCH (GUJRAT)

EDEP CONSULTANT:

MOVIN
MOVIN ENGINEERING CO., LTD

ADDRESS :-
–
–
–
–

THIS DRAWING AND/OR ITS CONTENTS, INFORMATION, AND PRINCIPLES OF DESIGN ARETHE EXCLUSIVE PROPERTY OF GRASIM CELLULOSIC, INDIA AND IS SUBMITTED TO YOU WITH THE AGREEMENT THAT IT IS NOT TO BE REPRODUCED IN ANY MANNER, COPIED, OR MODIFIED, NOR IS IT TO BE RELAYED IN PART OR IN WHOLE TO ANY OTHER FIRM OR INDIVIDUAL FOR ANY OTHER PROJECT EXCEPT BY WRITTEN AGREEMENT WITH GRASIM CELLULOSIC, INDIA.

JACOBS


JACOBS ENGINEERING INDIA PRIVATE LIMITED.
JACOBS HOUSE, RAMKRISHNA MANDIR ROAD,
KONDIVITA, ANDHERI (EAST), MUMBAI – 400059
TEL. +91-22-2681 2000


A MEMBER OF THE JACOBS ENGINEERING GROUP, INC.

GRASIM CELLULOSIC
VSF EXPANSION PROJECT
AUXILLIARY AREA
ELEVATION ON GRID B

PROJ.NO.	DRAWING NO.		REV
44AC6500	44AC6500-000-C.01-XXXX-A1		A
DATE	FILE NAME	DRAWING SCALE / PLOT SCALE	DRAWN BY
29.05.18	44AC6500000C01XXXXA1A	1:150 / 1:1	SBK

A1

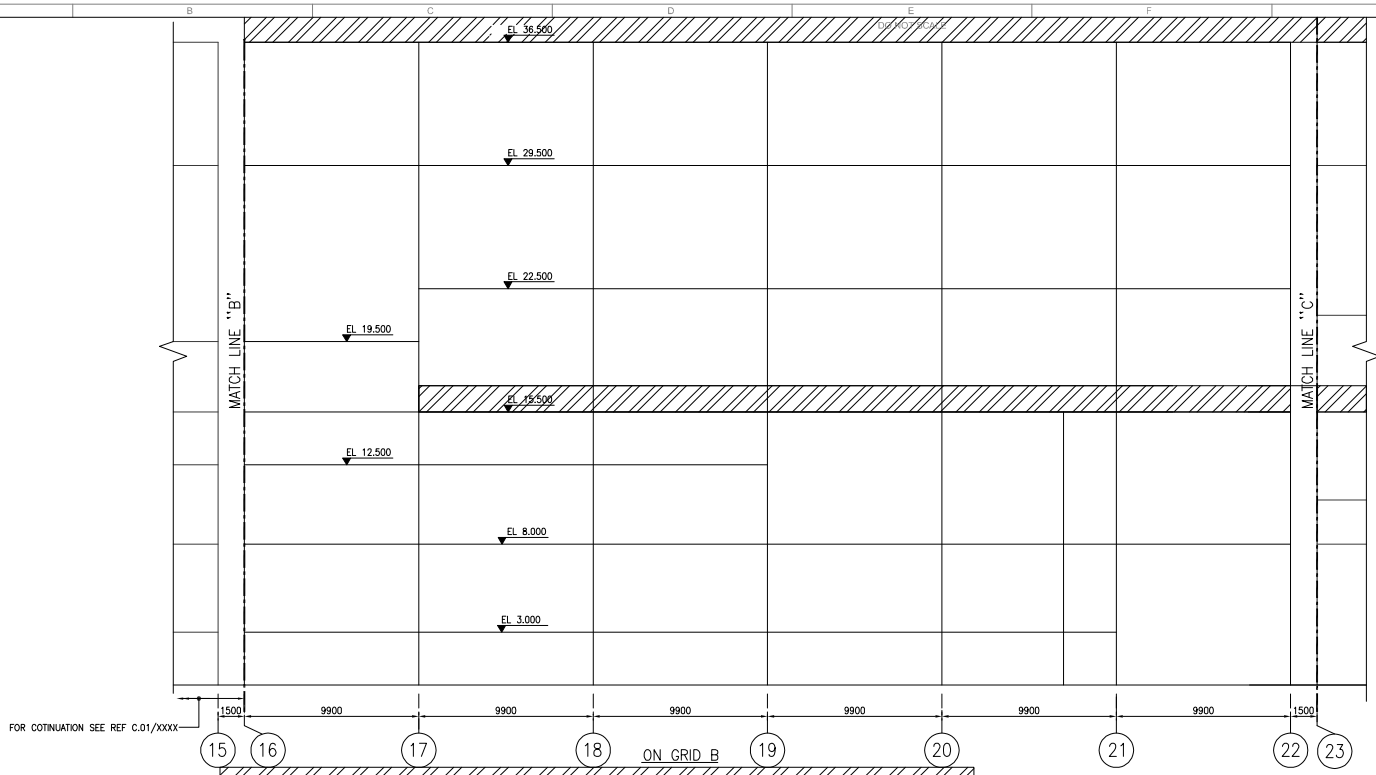

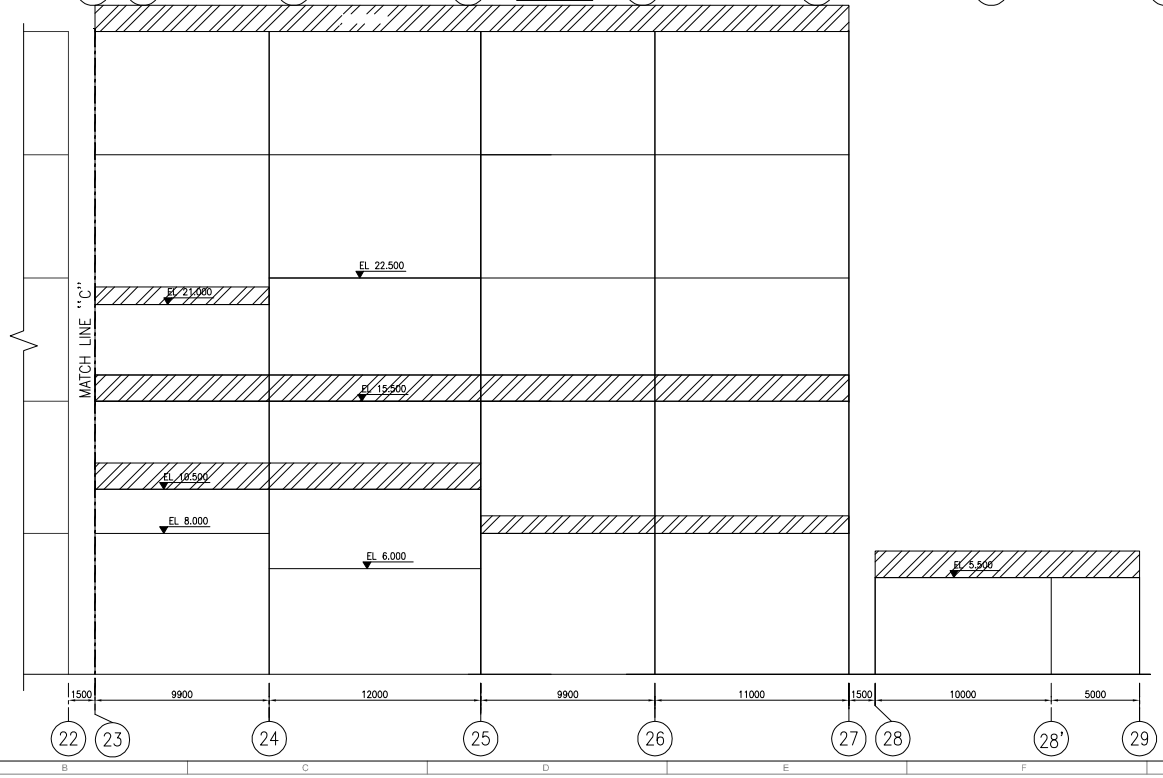

FOR TENDERING PURPOSE

REV. NO.	REVISION DESCRIPTION	DRAWN	CHK	APPROVED	CLIENT APPR.	DATE
–	–	–	–	–	–	–
–	–	–	–	–	–	–
–	–	–	–	–	–	–
–	–	–	–	–	–	–
–	–	–	–	–	–	–

CLIENT

ADITYA BIRLA GRASIM

GRASIM CELLULOSIC
(A UNIT OF GRASIM INDUSTRIES LTD.)
VILAYAT, BHARUCH (GUJRAT)

BDEP CONSULTANT:

MOVIN
MOVIN ENGINEERING CO., LTD

ADDRESS :-
–
–
–
–
–

THIS DRAWING AND/OR ITS CONTENTS, INFORMATION, AND PRINCIPLES OF DESIGN ARETHE EXCLUSIVE PROPERTY OF GRASIM CELLULOSIC, INDIA AND IS SUBMITTED TO YOU WITH THE AGREEMENT THAT IT IS NOT TO BE REPRODUCED IN ANY MANNER, COPIED, OR MODIFIED, NOR IS IT TO BE RELAYED IN PART OR IN WHOLE TO ANY OTHER FIRM OR INDIVIDUAL FOR ANY OTHER PROJECT EXCEPT BY WRITEN AGREEMENT WITH GRASIM CELLULOSIC, INDIA.

JACOBS

JACOBS ENGINEERING INDIA PRIVATE LIMITED.
JACOBS HOUSE, RAMKRISHNA MANDIR ROAD,
KONDIVITA, ANDHERI (EAST), MUMBAI – 400059
TEL. +91-22-2681 2000


A MEMBER OF THE JACOBS ENGINEERING GROUP, INC.

GRASIM CELLULOSIC
VSF EXPANSION PROJECT
AUXILLIARY AREA
ELEVATION ON GRID B


PROJ.NO.	DRAWING NO.		REV
44AC6500	44AC6500-000-C.01-XXXX-A1		A
DATE	FILE NAME	DRAWING SCALE / PLOT SCALE	DRAWN BY
29.05.18	44AC6500000C01XXXXA1A	1:150 / 1:1	SBK

A1


DO NOT SCALE

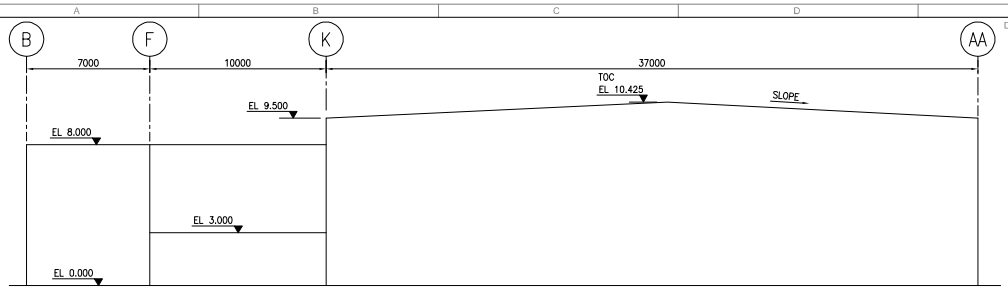


BETWEEN GRID 4 & 13
(LOOKING WEST)

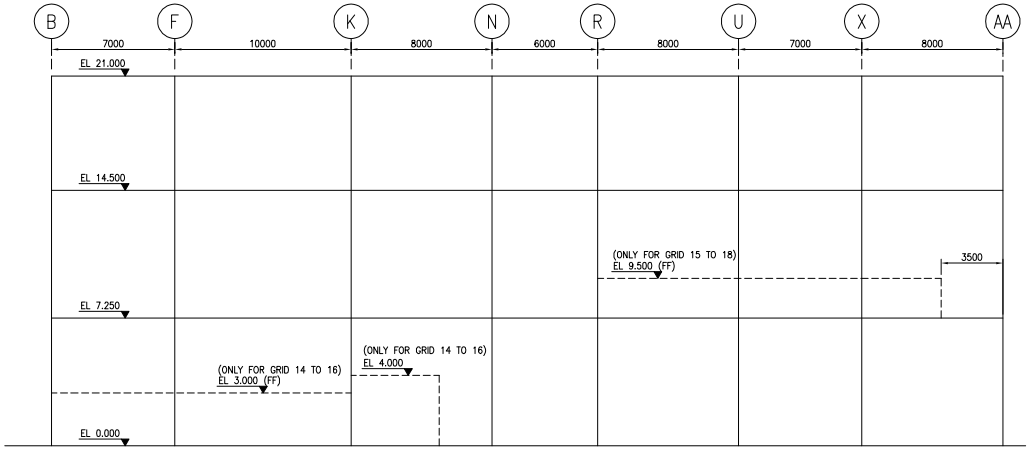


BETWEEN GRIDS 14 & 18
(LOOKING WEST)

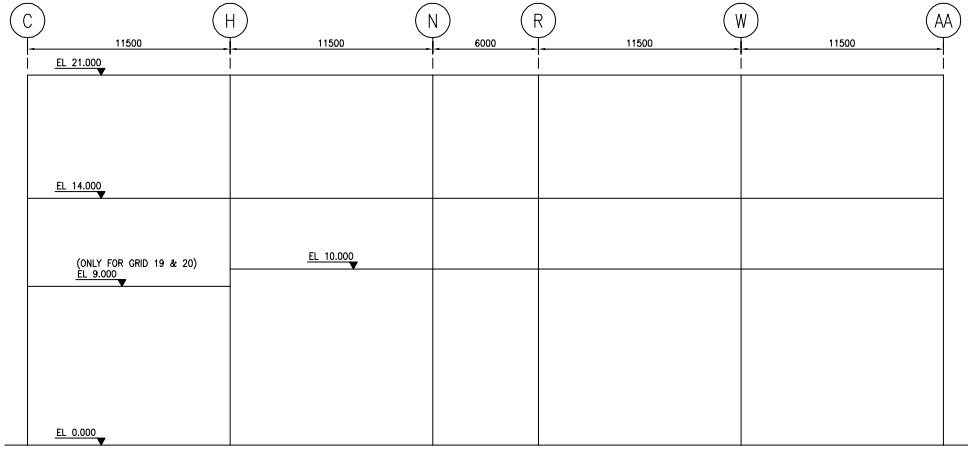

BETWEEN GRIDS 19 & 21
(LOOKING WEST)

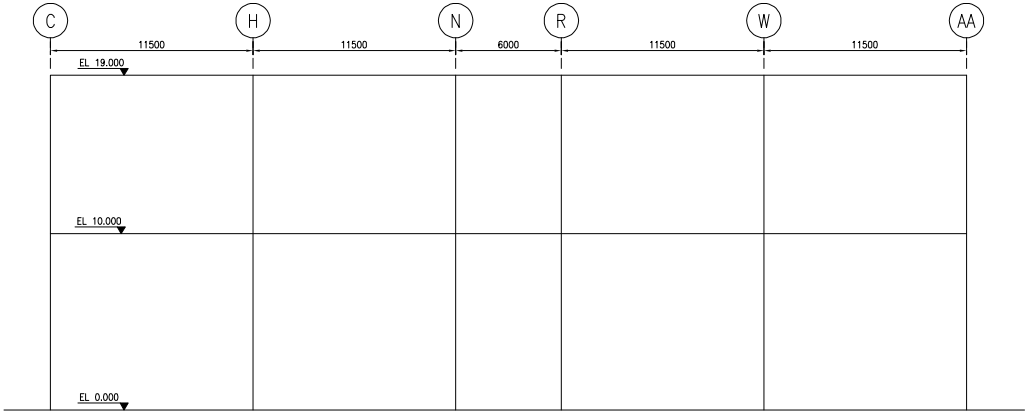

BETWEEN GRIDS 21 & 25

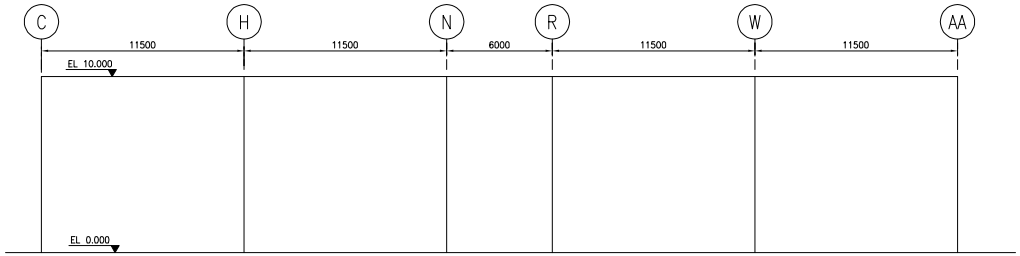

BETWEEN GRIDS 26 & 28

FOR TENDERING PURPOSE

REV. NO.	REVISION DESCRIPTION	DRAWN	CHK	APPROVED	CLIENT APPR.	DATE
–	–	–	–	–	–	
–	–	–	–	–	–	
–	–	–	–	–	–	
–	–	–	–	–	–	
–	–	–	–	–	–	

CLIENT
ADITYA BIRLA GRASIM
GRASIM CELLULOSIC
(A UNIT OF GRASIM INDUSTRIES LTD.)
VILAYAT, BHARUCH (GUJRAT)

EDEP CONSULTANT
MOVIN ENGINEERING CO., LTD

ADDRESS :-
–
–
–
–

THIS DRAWING AND/OR ITS CONTENTS, INFORMATION, AND PRINCIPLES OF DESIGN ARETHE EXCLUSIVE PROPERTY OF GRASIM CELLULOSIC, INDIA AND IS SUBMITTED TO YOU WITH THE AGREEMENT THAT IT IS NOT TO BE REPRODUCED IN ANY MANNER, COPIED, OR MODIFIED, NOR IS IT TO BE RELAYED IN PART OR IN WHOLE TO ANY OTHER FIRM OR INDIVIDUAL FOR ANY OTHER PROJECT EXCEPT BY WRITEN AGREEMENT WITH GRASIM CELLULOSIC, INDIA.

JACOBS

JACOBS ENGINEERING INDIA PRIVATE LIMITED.
JACOBS HOUSE, RAMKRISHNA MANDIR ROAD,
KONDIVITA, ANDHERI (EAST), MUMBAI – 400059
TEL. +91-22-2681 2000


A MEMBER OF THE JACOBS ENGINEERING GROUP, INC.

GRASIM CELLULOSIC
VSF EXPANSION PROJECT
VISCOSE AREA
ELEVATIONS


PROJ.NO.	DRAWING NO.		REV
44AC6500	44AC6500-000-C.01-0011A1		A
DATE	FILE NAME	DRAWING SCALE / PLOT SCALE	DRAWN BY
29.05.18	44AC6500000C010011A1A	1:150 / 1:1	SBK

A1

DO NOT SCALE

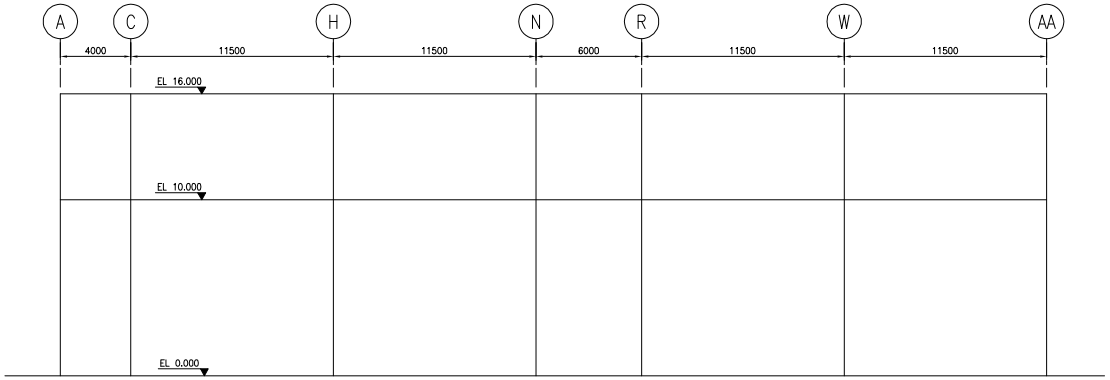

BETWEEN GRIDS 28 & 29

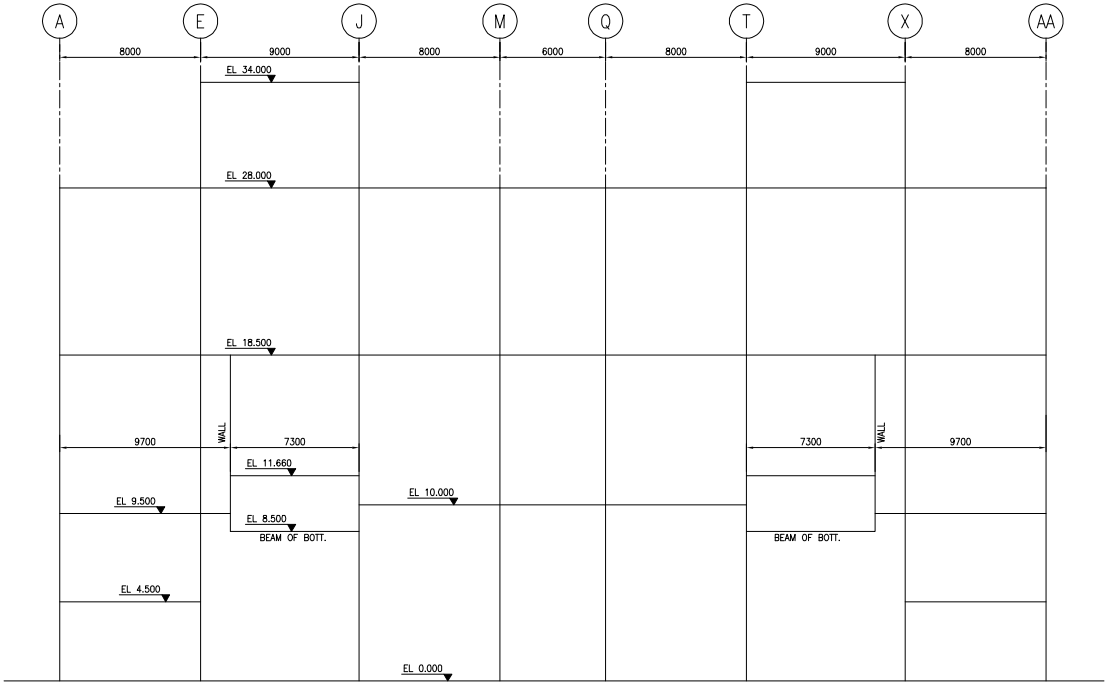

BETWEEN GRIDS 30 & 35

FOR TENDERING PURPOSE

REV. NO.	REVISION DESCRIPTION	DRAWN	CHK	APPROVED	CLIENT APPR.	DATE
–	–	–	–	–	–	–
–	–	–	–	–	–	–
–	–	–	–	–	–	–
–	–	–	–	–	–	–
–	–	–	–	–	–	–

CLIENT

ADITYA BIRLA GRASIM

GRASIM CELLULOSIC
(A UNIT OF GRASIM INDUSTRIES LTD.)
VILAYAT, BHARUCH (GUJRAT)

BDEP CONSULTANT

MOVIN
MOVIN ENGINEERING CO., LTD

ADDRESS :-
–
–
–
–

THIS DRAWING AND/OR ITS CONTENTS, INFORMATION, AND PRINCIPLES OF DESIGN ARETHE EXCLUSIVE PROPERTY OF GRASIM CELLULOSIC, INDIA AND IS SUBMITTED TO YOU WITH THE AGREEMENT THAT IT IS NOT TO BE REPRODUCED IN ANY MANNER, COPIED, OR MODIFIED, NOR IS IT TO BE RELAYED IN PART OR IN WHOLE TO ANY OTHER FIRM OR INDIVIDUAL FOR ANY OTHER PROJECT EXCEPT BY WRITTEN AGREEMENT WITH GRASIM CELLULOSIC, INDIA.

JACOBS

JACOBS ENGINEERING INDIA PRIVATE LIMITED.
JACOBS HOUSE, RAMKRISHNA MANDIR ROAD,
KONDIVITA, ANDHERI (EAST), MUMBAI – 400059
TEL. +91-22-2681 2000


A MEMBER OF THE JACOBS ENGINEERING GROUP, INC.

GRASIM CELLULOSIC
VSF EXPANSION PROJECT
VISCOSE AREA
ELEVATIONS


PROJ.NO.	DRAWING NO.		REV
44AC6500	44AC6500-000-C.01-0012-A1		A
DATE	FILE NAME	DRAWING SCALE / PLOT SCALE	DRAWN BY
29.05.18	44AC6500000C010012A1A	1:150 / 1:1	SBK

A1

DO NOT SCALE

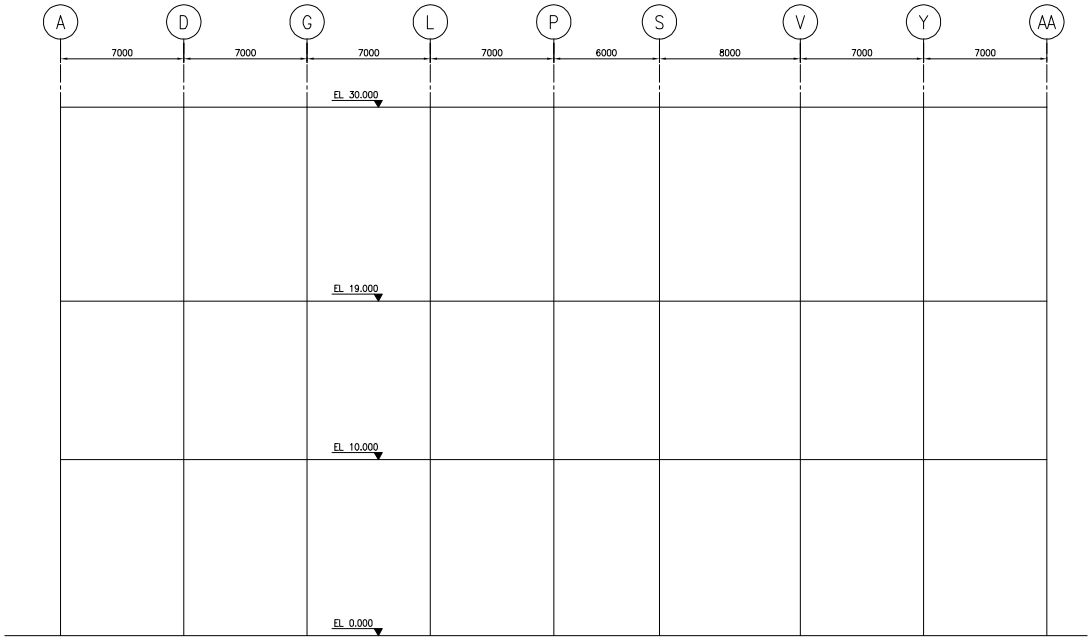

BETWEEN GRIDS 42 & 48

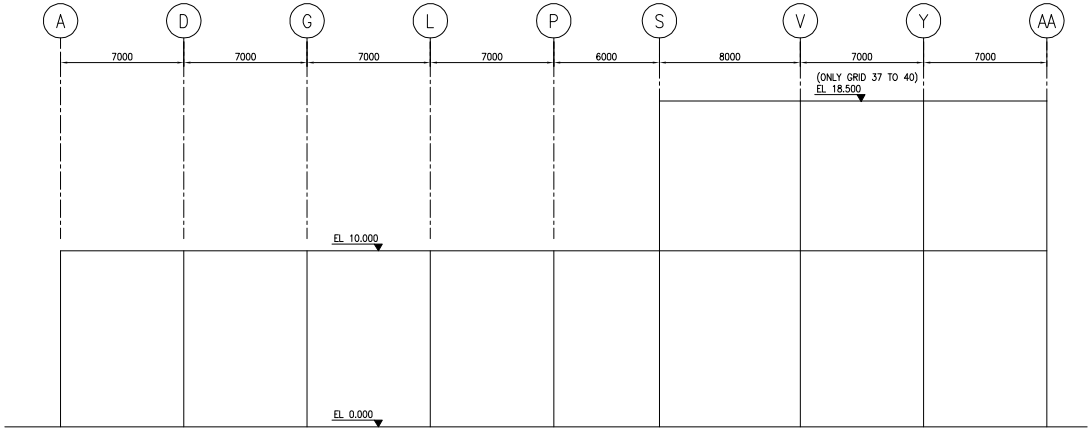

BETWEEN GRIDS 36 & 41

FOR TENDERING PURPOSE

REV. NO.	REVISION DESCRIPTION	DRAWN	CHK	APPROVED	CLIENT APPR.	DATE
–	–	–	–	–	–	–
–	–	–	–	–	–	–
–	–	–	–	–	–	–
–	–	–	–	–	–	–
–	–	–	–	–	–	–

CLIENT

ADITYA BIRLA GRASIM

GRASIM CELLULOSIC
(A UNIT OF GRASIM INDUSTRIES LTD.)
VILAYAT, BHARUCH (GUJRAT)

BDEP CONSULTANT

MOVIN
MOVIN ENGINEERING CO., LTD

ADDRESS :-
–
–
–
–
–

THIS DRAWING AND/OR ITS CONTENTS, INFORMATION, AND PRINCIPLES OF DESIGN ARETHE EXCLUSIVE PROPERTY OF GRASIM CELLULOSIC, INDIA AND IS SUBMITTED TO YOU WITH THE AGREEMENT THAT IT IS NOT TO BE REPRODUCED IN ANY MANNER, COPIED, OR MODIFIED, NOR IS IT TO BE RELAYED IN PART OR IN WHOLE TO ANY OTHER FIRM OR INDIVIDUAL FOR ANY OTHER PROJECT EXCEPT BY WRITTEN AGREEMENT WITH GRASIM CELLULOSIC, INDIA.

JACOBS

JACOBS ENGINEERING INDIA PRIVATE LIMITED.
JACOBS HOUSE, RAMKRISHNA MANDIR ROAD,
KONDIVITA, ANDHERI (EAST), MUMBAI – 400059
TEL. +91-22-2681 2000


A MEMBER OF THE JACOBS ENGINEERING GROUP, INC.

GRASIM CELLULOSIC
VSF EXPANSION PROJECT
VISCOSE AREA
ELEVATIONS

PROJ.NO.	DRAWING NO.		REV
44AC6500	44AC6500-000-C.01-0013-A1		A
DATE	FILE NAME	DRAWING SCALE / PLOT SCALE	DRAWN BY
29.05.18	44AC6500000C010013A1A	1:150 / 1:1	SBK

A1

DO NOT SCALE

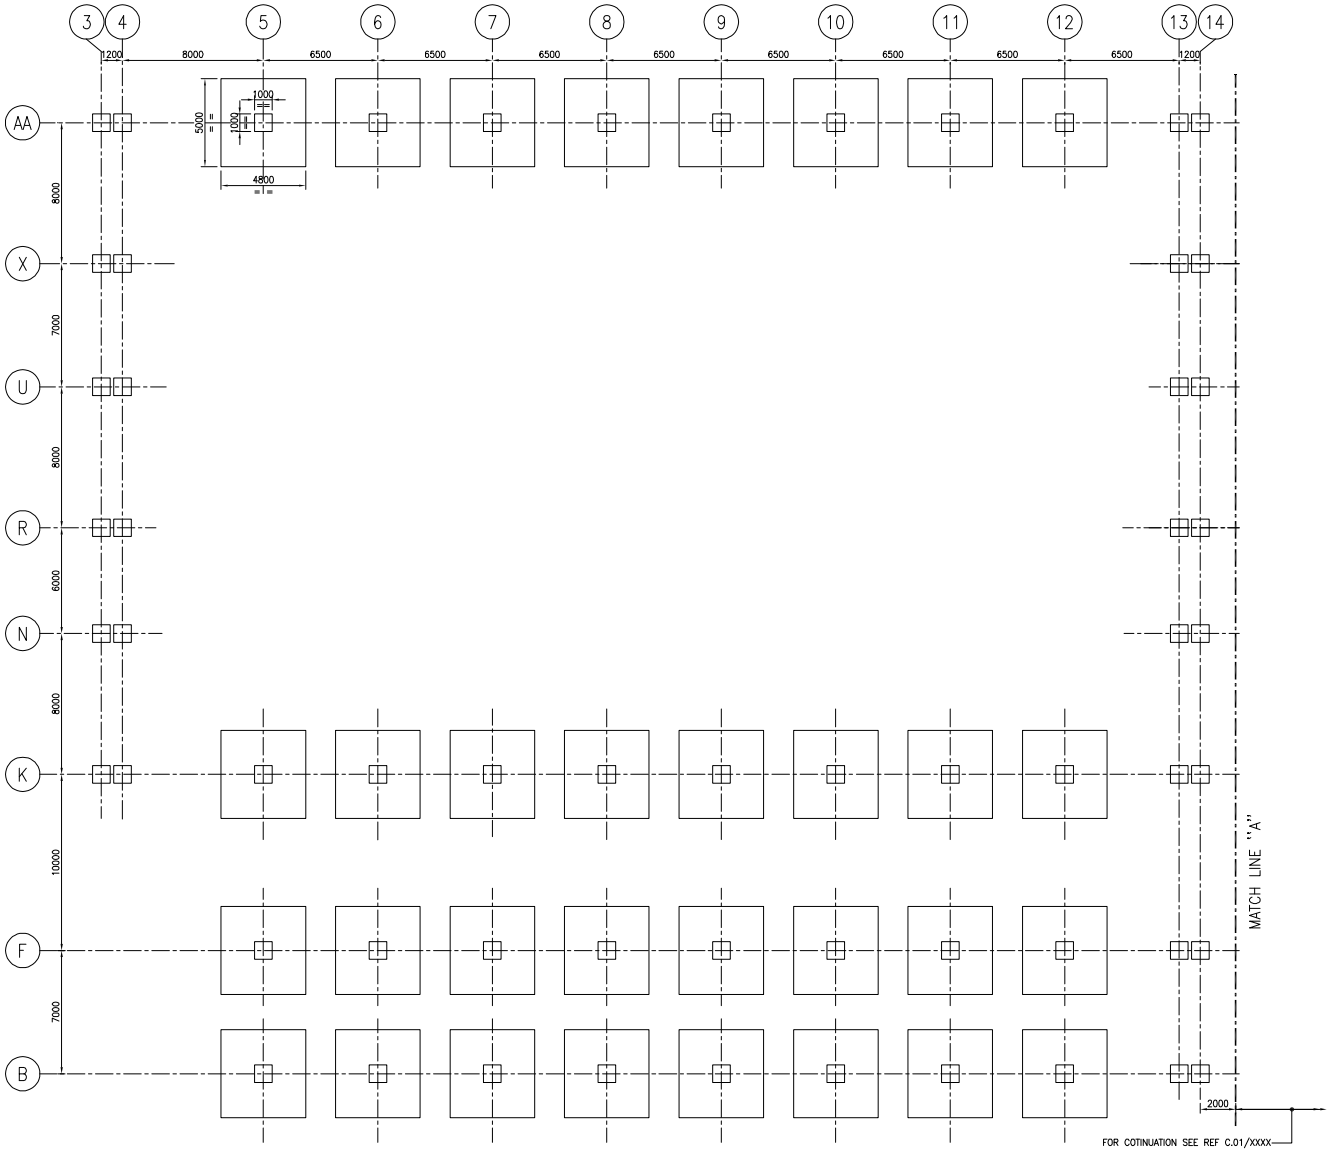

FOUNDATION PLAN

N

REF NORTH

FOR TENDERING PURPOSE

REV. NO.	REVISION DESCRIPTION	DRAWN	CHK	APPROVED	CLIENT APPR.	DATE
–	–	–	–	–	–	–
–	–	–	–	–	–	–
–	–	–	–	–	–	–
–	–	–	–	–	–	–
–	–	–	–	–	–	–

CLIENT

ADITYA BIRLA GRASIM

GRASIM CELLULOSIC
(A UNIT OF GRASIM INDUSTRIES LTD.)
VILAYAT, BHARUCH (GUJRAT)

BDEP CONSULTANT

MOVIN
MOVIN ENGINEERING CO., LTD

ADDRESS :-
–
–
–
–

THIS DRAWING AND/OR ITS CONTENTS, INFORMATION, AND PRINCIPLES OF DESIGN ARE THE EXCLUSIVE PROPERTY OF GRASIM CELLULOSIC, INDIA AND IS SUBMITTED TO YOU WITH THE AGREEMENT THAT IT IS NOT TO BE REPRODUCED IN ANY MANNER, COPIED, OR MODIFIED, NOR IS IT TO BE RELAYED IN PART OR IN WHOLE TO ANY OTHER FIRM OR INDIVIDUAL FOR ANY OTHER PROJECT EXCEPT BY WRITTEN AGREEMENT WITH GRASIM CELLULOSIC, INDIA.

JACOBS

JACOBS ENGINEERING INDIA PRIVATE LIMITED.
JACOBS HOUSE, RAMKRISHNA MANDIR ROAD,
KONDIVITA, ANDHERI (EAST), MUMBAI – 400059
TEL. +91-22-2681 2000


A MEMBER OF THE JACOBS ENGINEERING GROUP, INC.

GRASIM CELLULOSIC
VSF EXPANSION PROJECT
VISCOSE AREA
L/O OF FDN BETWEEN GRIDS 3-14 & B-AA

PROJ.NO.	DRAWING NO.		REV
44AC6500	44AC6500-000-C.01-XXXX-A1		A
DATE	FILE NAME	DRAWING SCALE / PLOT SCALE	DRAWN BY
29.05.18	44AC6500000C01XXXXA1A	1:150 / 1:1	SBK

A1

DO NOT SCALE

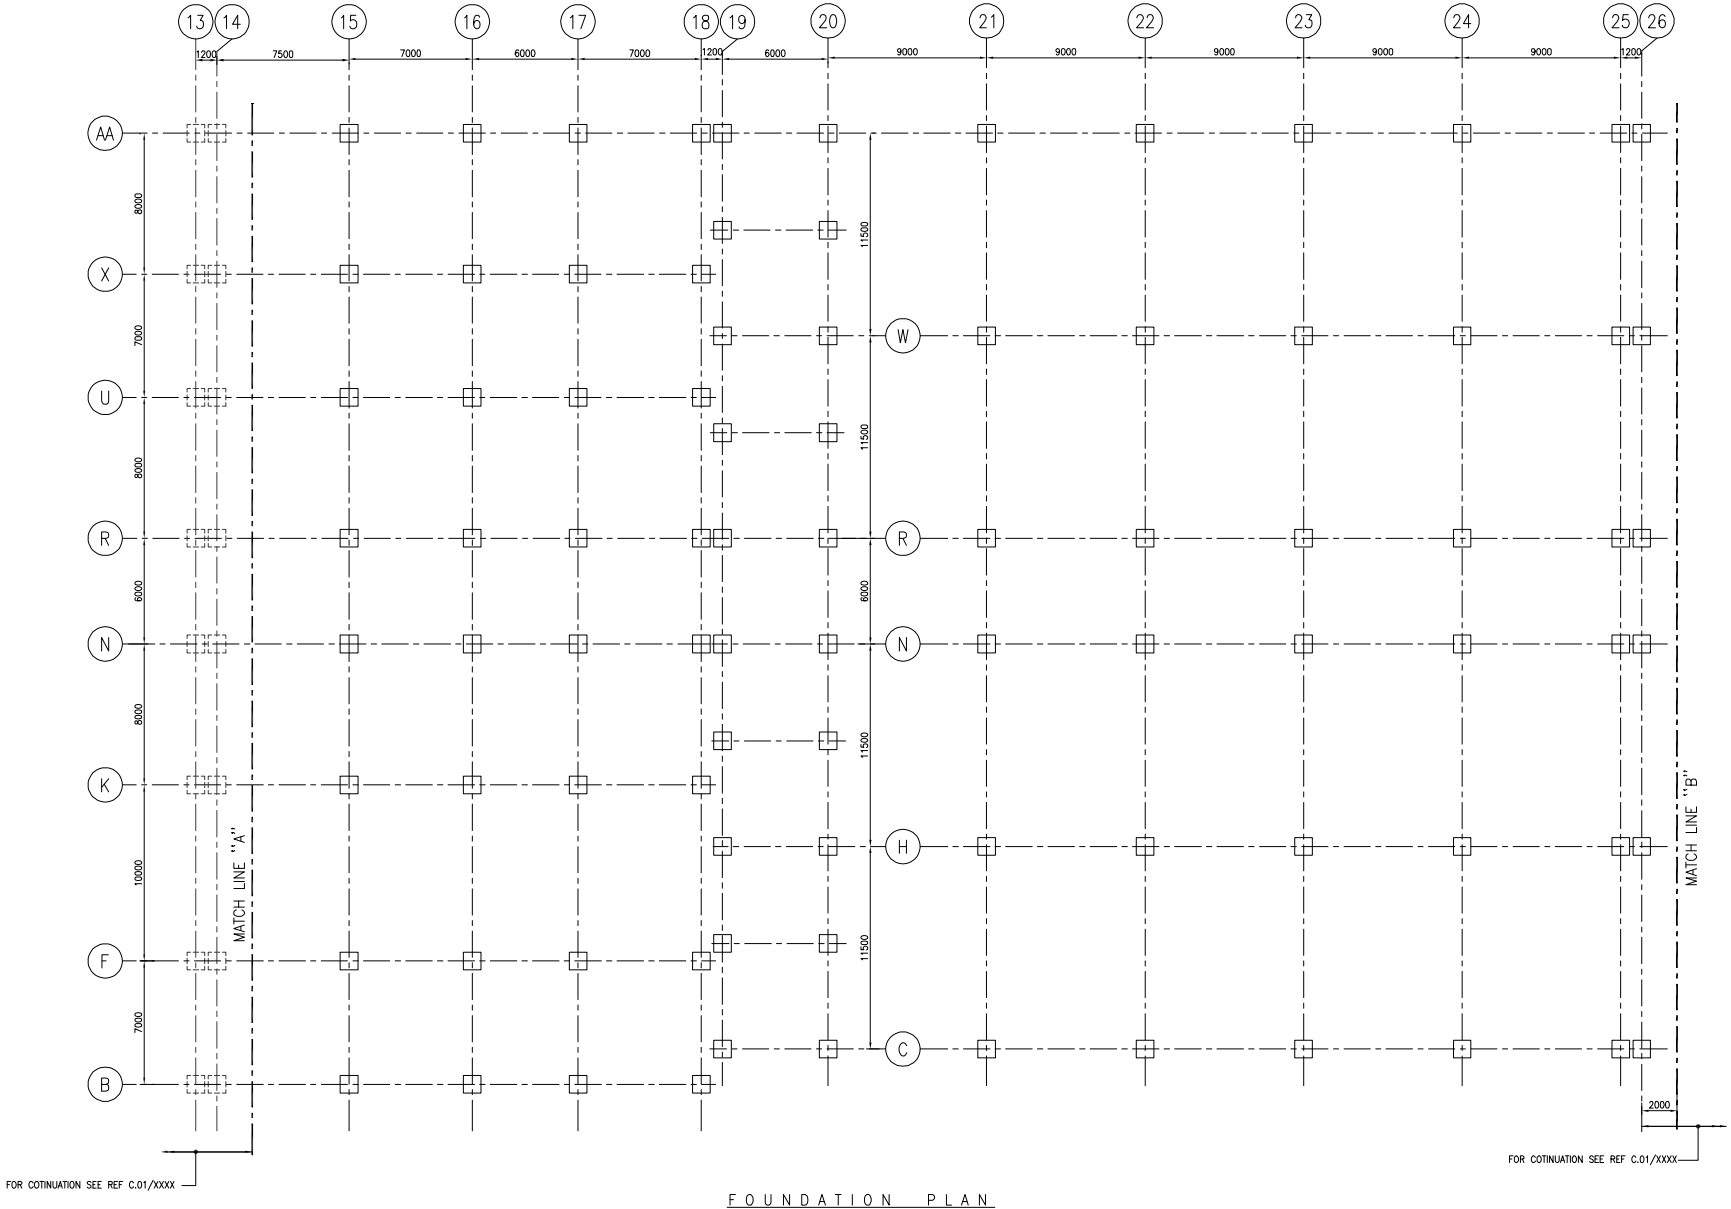

FOUNDATION PLAN

REF NORTH

FOR TENDERING PURPOSE

REV. NO.	REVISION DESCRIPTION	DRAWN	CHK	APPROVED	CLIENT APPR.	DATE
–	–	–	–	–	–	–
–	–	–	–	–	–	–
–	–	–	–	–	–	–
–	–	–	–	–	–	–
–	–	–	–	–	–	–

CLIENT

ADITYA BIRLA GRASIM

GRASIM CELLULOSIC
(A UNIT OF GRASIM INDUSTRIES LTD.)
VILAYAT, BHARUCH (GUJRAT)

BDEP CONSULTANT

MOVIN
MOVIN ENGINEERING CO., LTD

ADDRESS :-
–
–
–
–

THIS DRAWING AND/OR ITS CONTENTS, INFORMATION, AND PRINCIPLES OF DESIGN ARETHE EXCLUSIVE PROPERTY OF GRASIM CELLULOSIC, INDIA AND IS SUBMITTED TO YOU WITH THE AGREEMENT THAT IT IS NOT TO BE REPRODUCED IN ANY MANNER, COPIED, OR MODIFIED, NOR IS IT TO BE RELAYED IN PART OR IN WHOLE TO ANY OTHER FIRM OR INDIVIDUAL FOR ANY OTHER PROJECT EXCEPT BY WRITTEN AGREEMENT WITH GRASIM CELLULOSIC, INDIA.

JACOBS

JACOBS ENGINEERING INDIA PRIVATE LIMITED.
JACOBS HOUSE, RAMKRISHNA MANDIR ROAD,
KONDIVITA, ANDHERI (EAST), MUMBAI – 400059
TEL. +91-22-2681 2000


A MEMBER OF THE JACOBS ENGINEERING GROUP, INC.

GRASIM CELLULOSIC
VSF EXPANSION PROJECT
VISCOSE AREA
L/O OF FDN BETWEEN GRIDS 13–18 & B–AA AND 19–26 & C–AA

PROJ.NO.	DRAWING NO.		REV
44AC6500	44AC6500-000-C.01-XXXX-A1		0
DATE	FILE NAME	DRAWING SCALE / PLOT SCALE	DRAWN BY
29.05.18	44AC6500000C01XXXXA1A	1:150 / 1:1	SBK

A1

DO NOT SCALE

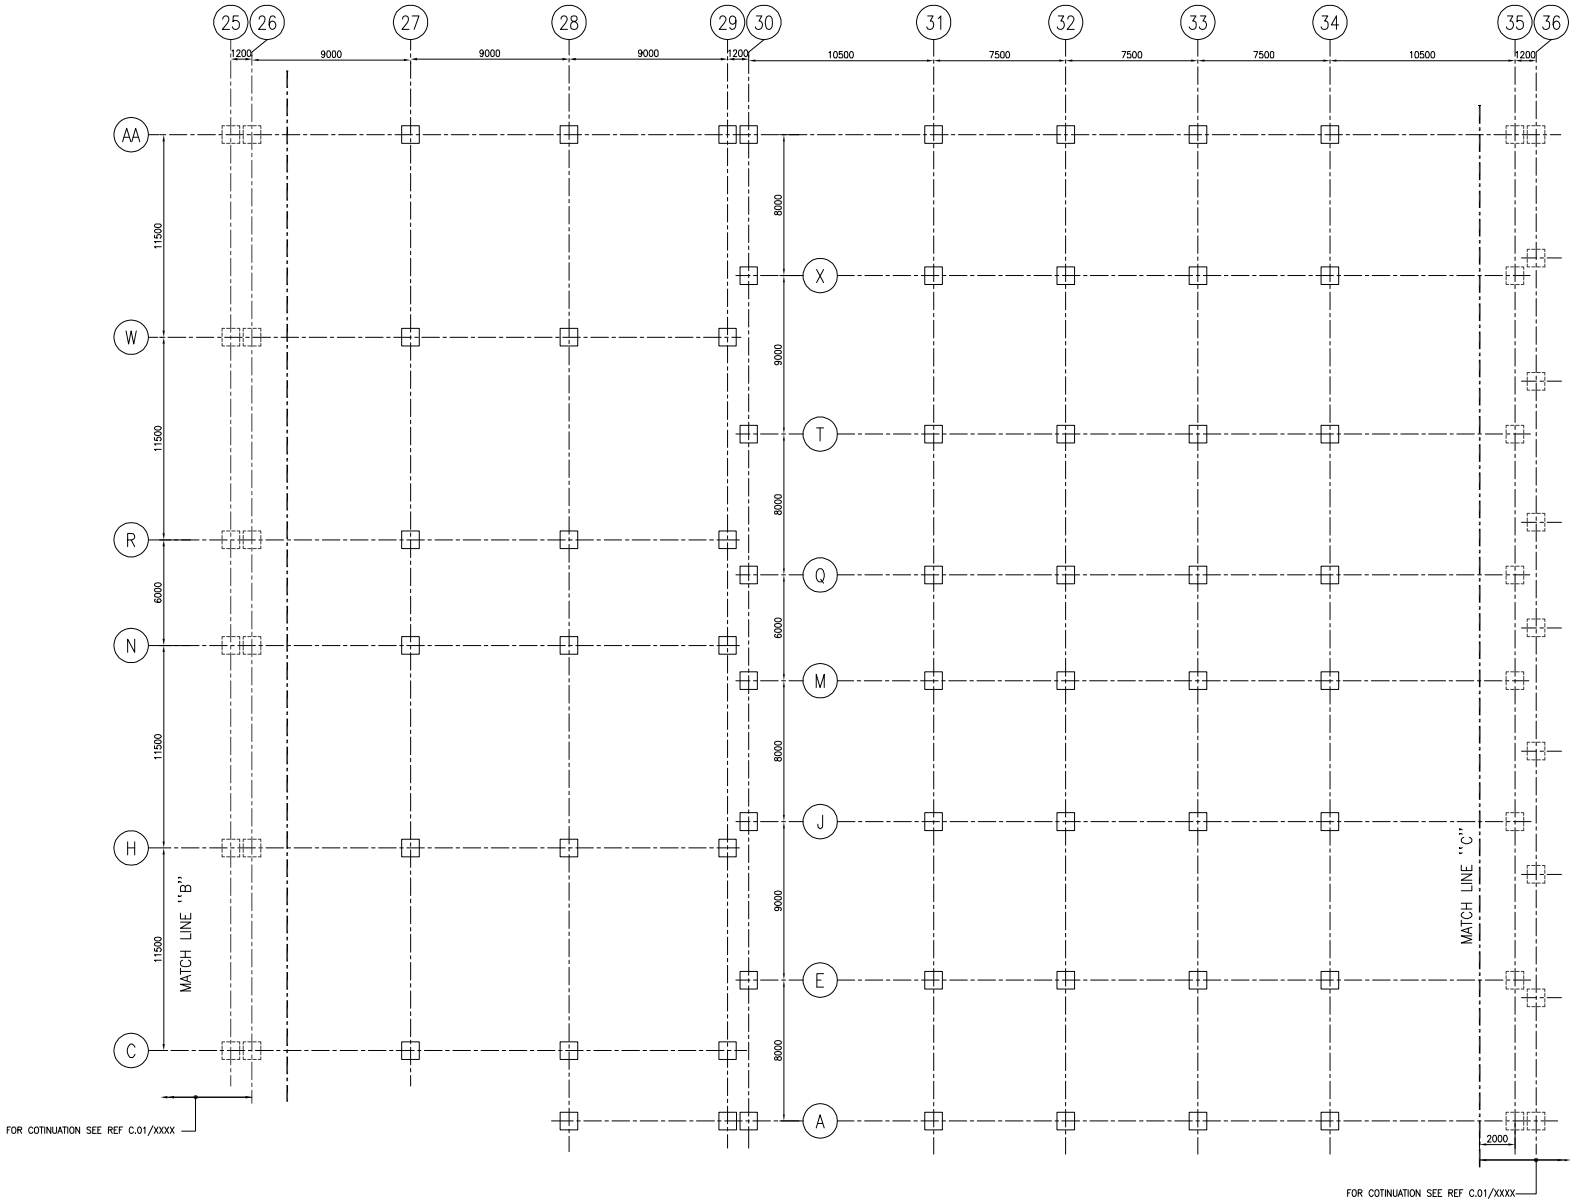

FOUNDATION PLAN

N

REF NORTH

FOR TENDERING PURPOSE

REV. NO.	REVISION DESCRIPTION	DRAWN	CHK	APPROVED	CLIENT APPR.	DATE
–	–	–	–	–	–	
–	–	–	–	–	–	
–	–	–	–	–	–	
–	–	–	–	–	–	
–	–	–	–	–	–	

CLIENT

ADITYA BIRLA GRASIM

GRASIM CELLULOSIC

(A UNIT OF GRASIM INDUSTRIES LTD.)

VILAYAT, BHARUCH (GUJRAT)

BDEP CONSULTANT

MOVIN ENGINEERING CO., LTD

ADDRESS :-
–
–
–
–

THIS DRAWING AND/OR ITS CONTENTS, INFORMATION, AND PRINCIPLES OF DESIGN ARETHE EXCLUSIVE PROPERTY OF GRASIM CELLULOSIC, INDIA AND IS SUBMITTED TO YOU WITH THE AGREEMENT THAT IT IS NOT TO BE REPRODUCED IN ANY MANNER, COPIED, OR MODIFIED, NOR IS IT TO BE RELAYED IN PART OR IN WHOLE TO ANY OTHER FIRM OR INDIVIDUAL FOR ANY OTHER PROJECT EXCEPT BY WRITTEN AGREEMENT WITH GRASIM CELLULOSIC, INDIA.

JACOBS

JACOBS ENGINEERING INDIA PRIVATE LIMITED.
JACOBS HOUSE, RAMKRISHNA MANDIR ROAD,
KONDIVITA, ANDHERI (EAST), MUMBAI – 400059
TEL. +91-22-2681 2000


A MEMBER OF THE JACOBS ENGINEERING GROUP, INC.

GRASIM CELLULOSIC
VSF EXPANSION PROJECT
VISCOSE AREA
L/O OF FDN BETWEEN GRIDS 25–27 & C–AA AND 28–36 & A–AA

PROJ.NO.	DRAWING NO.		REV
44AC6500	44AC6500-000-C.01-XXXX-A1		A
DATE	FILE NAME	DRAWING SCALE / PLOT SCALE	DRAWN BY
30.05.18	44AC6500000C01XXXXA1A	1:150 / 1:1	SBK

A1

DO NOT SCALE

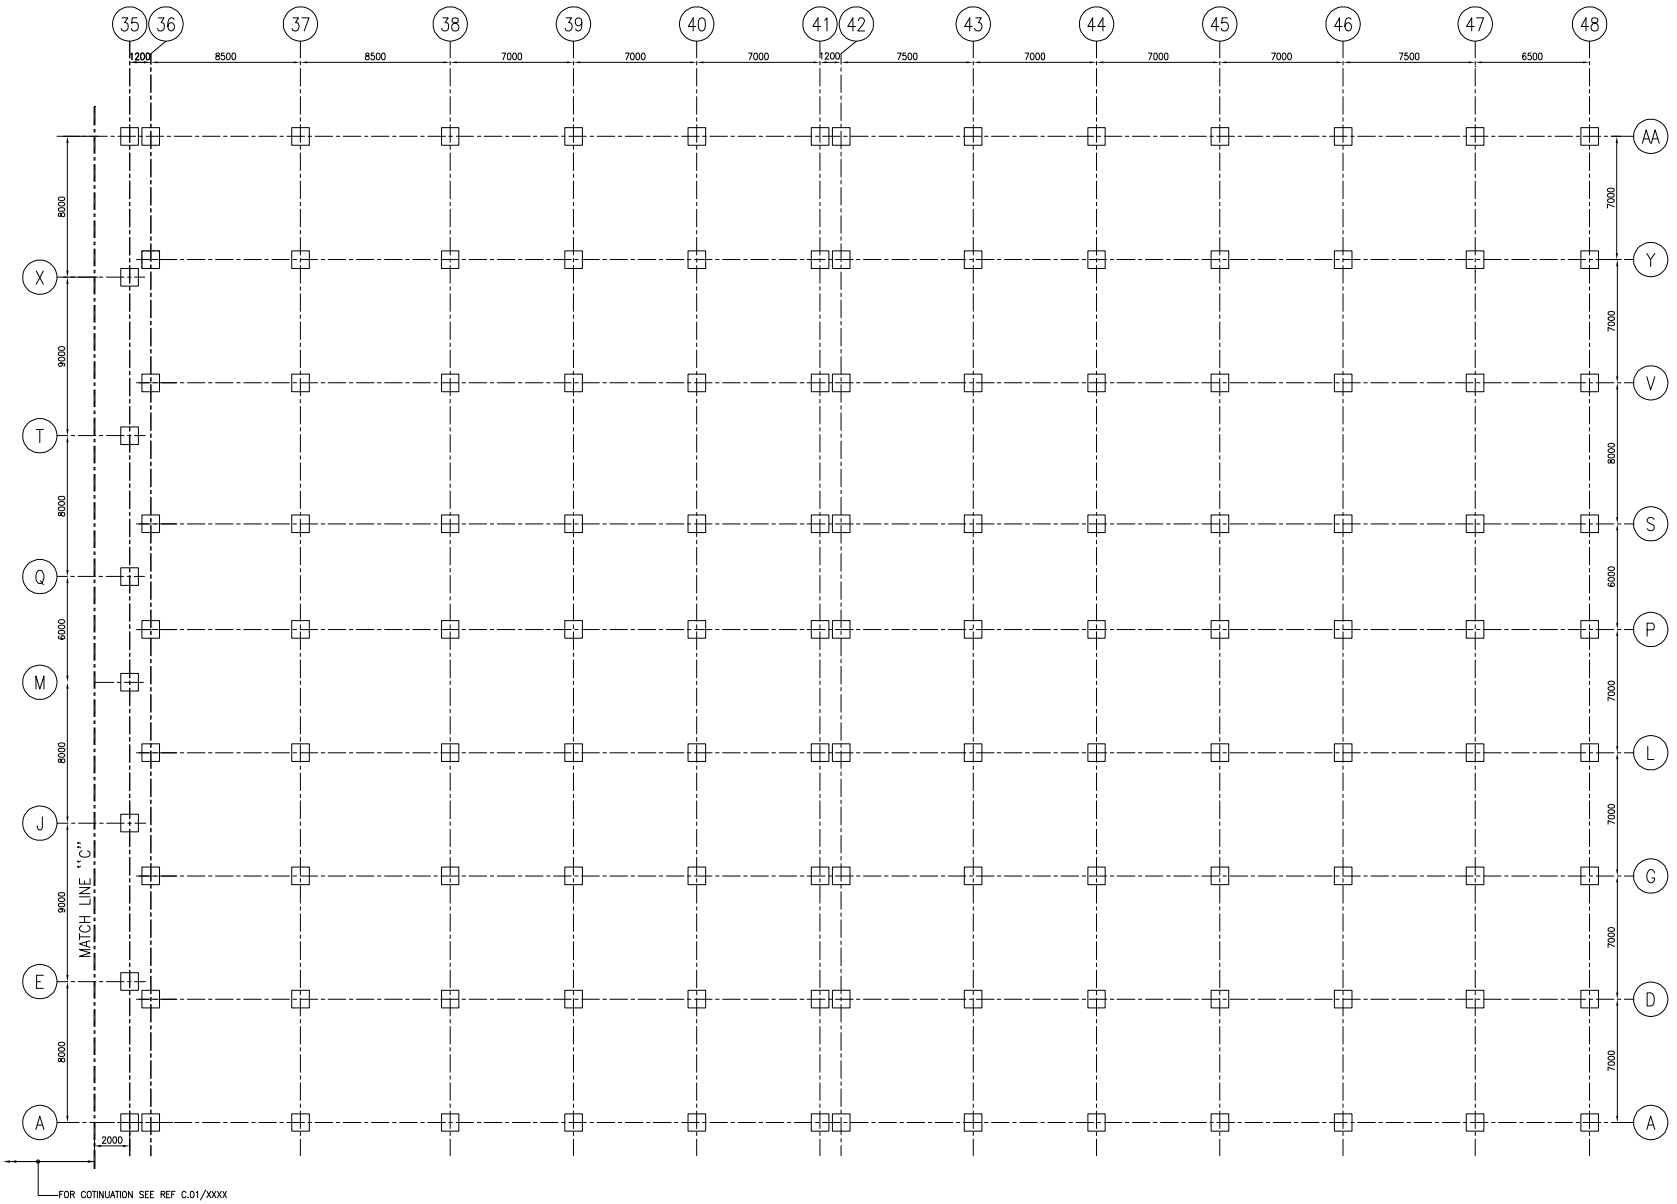

FOUNDATION PLAN

N

REF NORTH

FOR TENDERING PURPOSE

REV. NO.	REVISION DESCRIPTION	DRAWN	CHK	APPROVED	CLIENT APPR.	DATE
–	–	–	–	–	–	
–	–	–	–	–	–	
–	–	–	–	–	–	
–	–	–	–	–	–	
–	–	–	–	–	–	

CLIENT

ADITYA BIRLA GRASIM

GRASIM CELLULOSIC
(A UNIT OF GRASIM INDUSTRIES LTD.)
VILAYAT, BHARUCH (GUJRAT)

BDEP CONSULTANT

MOVIN
MOVIN ENGINEERING CO., LTD

ADDRESS :-
–
–
–
–
–

THIS DRAWING AND/OR ITS CONTENTS, INFORMATION, AND PRINCIPLES OF DESIGN ARE THE EXCLUSIVE PROPERTY OF GRASIM CELLULOSIC, INDIA AND IS SUBMITTED TO YOU WITH THE AGREEMENT THAT IT IS NOT TO BE REPRODUCED IN ANY MANNER, COPIED, OR MODIFIED, NOR IS IT TO BE RELAYED IN PART OR IN WHOLE TO ANY OTHER FIRM OR INDIVIDUAL FOR ANY OTHER PROJECT EXCEPT BY WRITTEN AGREEMENT WITH GRASIM CELLULOSIC, INDIA.

JACOBS

JACOBS ENGINEERING INDIA PRIVATE LIMITED.
JACOBS HOUSE, RAMKRISHNA MANDIR ROAD,
KONDIVITA, ANDHERI (EAST), MUMBAI – 400059
TEL. +91-22-2681 2000


A MEMBER OF THE JACOBS ENGINEERING GROUP, INC.

GRASIM CELLULOSIC
VSF EXPANSION PROJECT
VISCOSE AREA
L/O OF FDN BETWEEN GRIDS 35–48 & A–AA

PROJ.NO.	DRAWING NO.		REV
44AC6500	44AC6500-000-C.01-XXXX-A1		A
DATE	FILE NAME	DRAWING SCALE / PLOT SCALE	DRAWN BY
31.05.18	44AC6500000C01XXXXA1A	1:150 / 1:1	SBK

A1

DO NOT SCALE

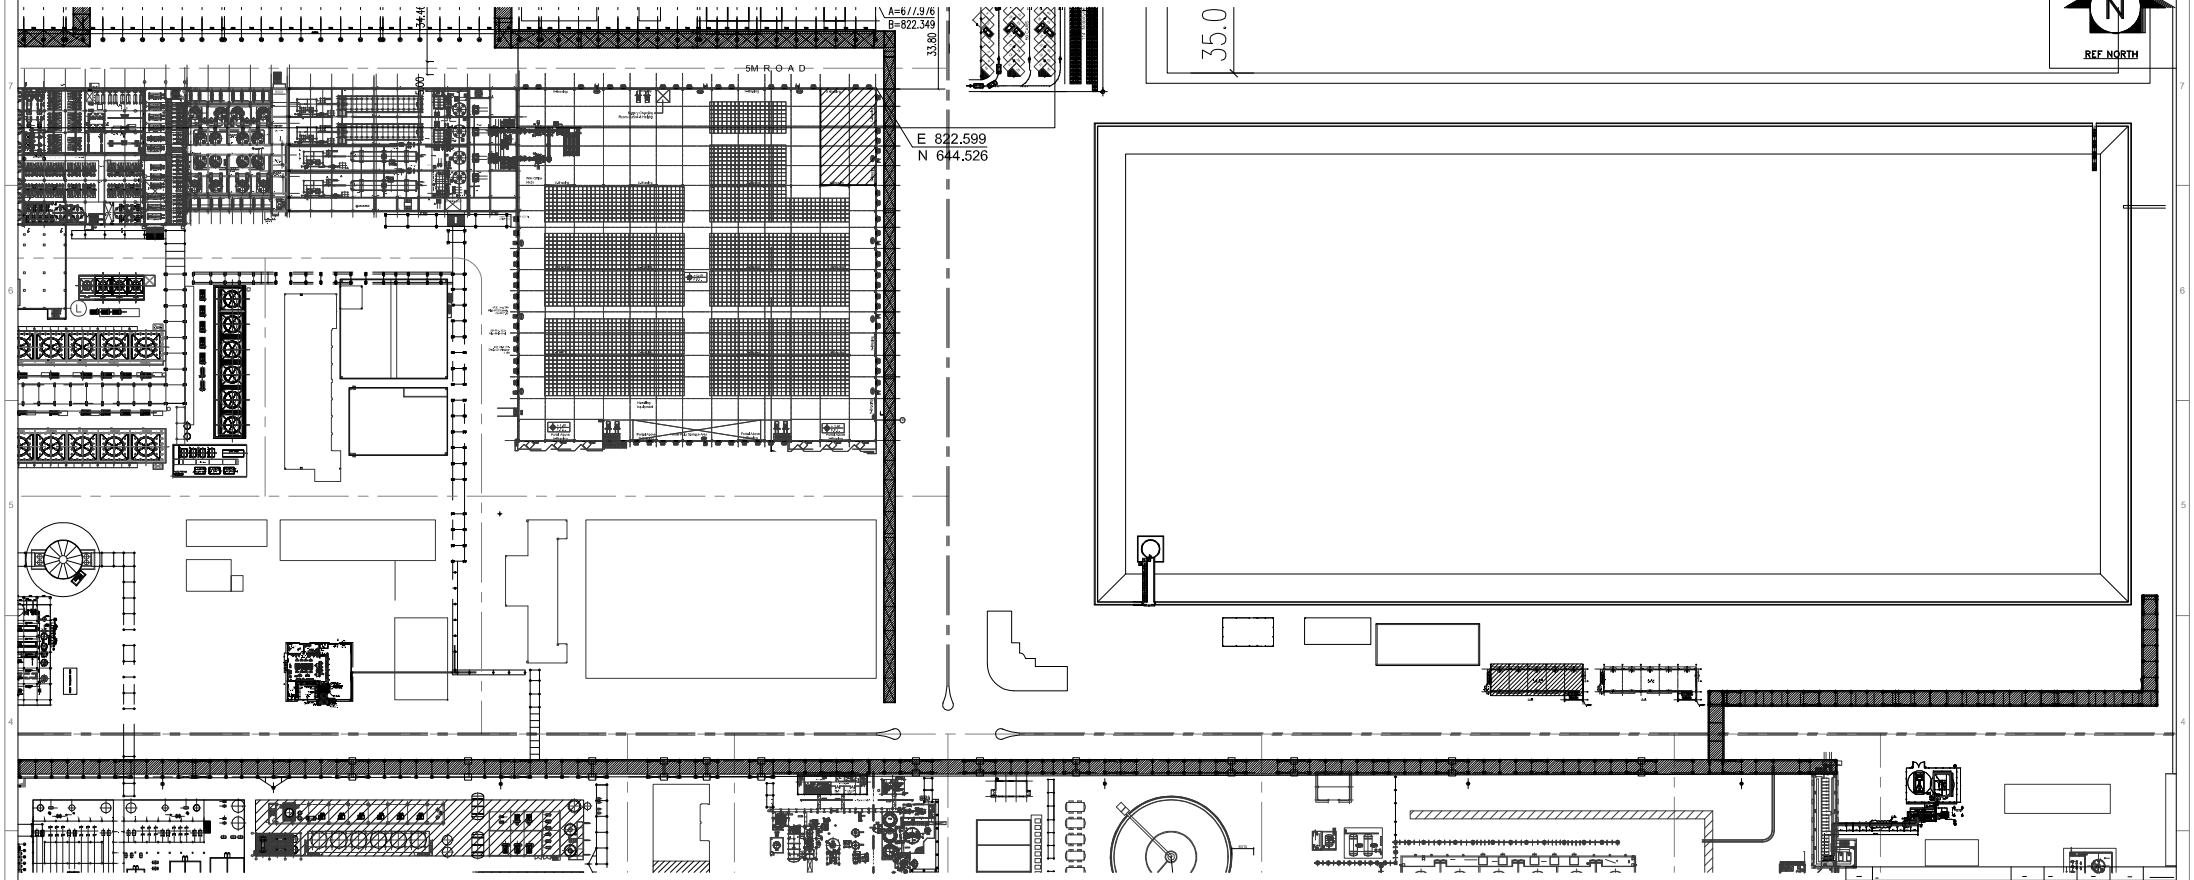

REV. NO.	REVISION DESCRIPTION	DRAWN	CHK	APPROVED	CLIENT APPR.	DATE
–	–	–	–	–	–	–
–	–	–	–	–	–	–
–	–	–	–	–	–	–
–	–	–	–	–	–	–
–	–	–	–	–	–	–

CLIENT

ADITYA BIRLA GRASIM

GRASIM CELLULOSIC
(A UNIT OF GRASIM INDUSTRIES LTD.)
VILAYAT, BHARUCH (GUJRAT)

BDEP CONSULTANT

MOVIN
MOVIN ENGINEERING CO., LTD

ADDRESS :-
–
–
–
–

THIS DRAWING AND/OR ITS CONTENTS, INFORMATION, AND PRINCIPLES OF DESIGN ARETHE EXCLUSIVE PROPERTY OF GRASIM CELLULOSIC, INDIA AND IS SUBMITTED TO YOU WITH THE AGREEMENT THAT IT IS NOT TO BE REPRODUCED IN ANY MANNER, COPIED, OR MODIFIED, NOR IS IT TO BE RELAYED IN PART OR IN WHOLE TO ANY OTHER FIRM OR INDIVIDUAL FOR ANY OTHER PROJECT EXCEPT BY WRITTEN AGREEMENT WITH GRASIM CELLULOSIC, INDIA.

FOR TENDERING PURPOSE

JACOBS

JACOBS ENGINEERING INDIA PRIVATE LIMITED.
JACOBS HOUSE, RAMKRISHNA MANDIR ROAD,
KONDIVITA, ANDHERI (EAST), MUMBAI – 400059
TEL. +91-22-2681 2000

A MEMBER OF THE JACOBS ENGINEERING GROUP, INC.

GRASIM CELLULOSIC
VSF EXPANSION PROJECT


PIPE RACK


PROJ.NO.	DRAWING NO.		REV
44AC6500	44AC6500-000-C.01-XXXX-A1		A
DATE	FILE NAME	DRAWING SCALE / PLOT SCALE	DRAWN BY
29.05.18	44AC6500000C01XXXXA1A	1:150 / 1:1	SBK

A1

DO NOT SCALE

REF NORTH

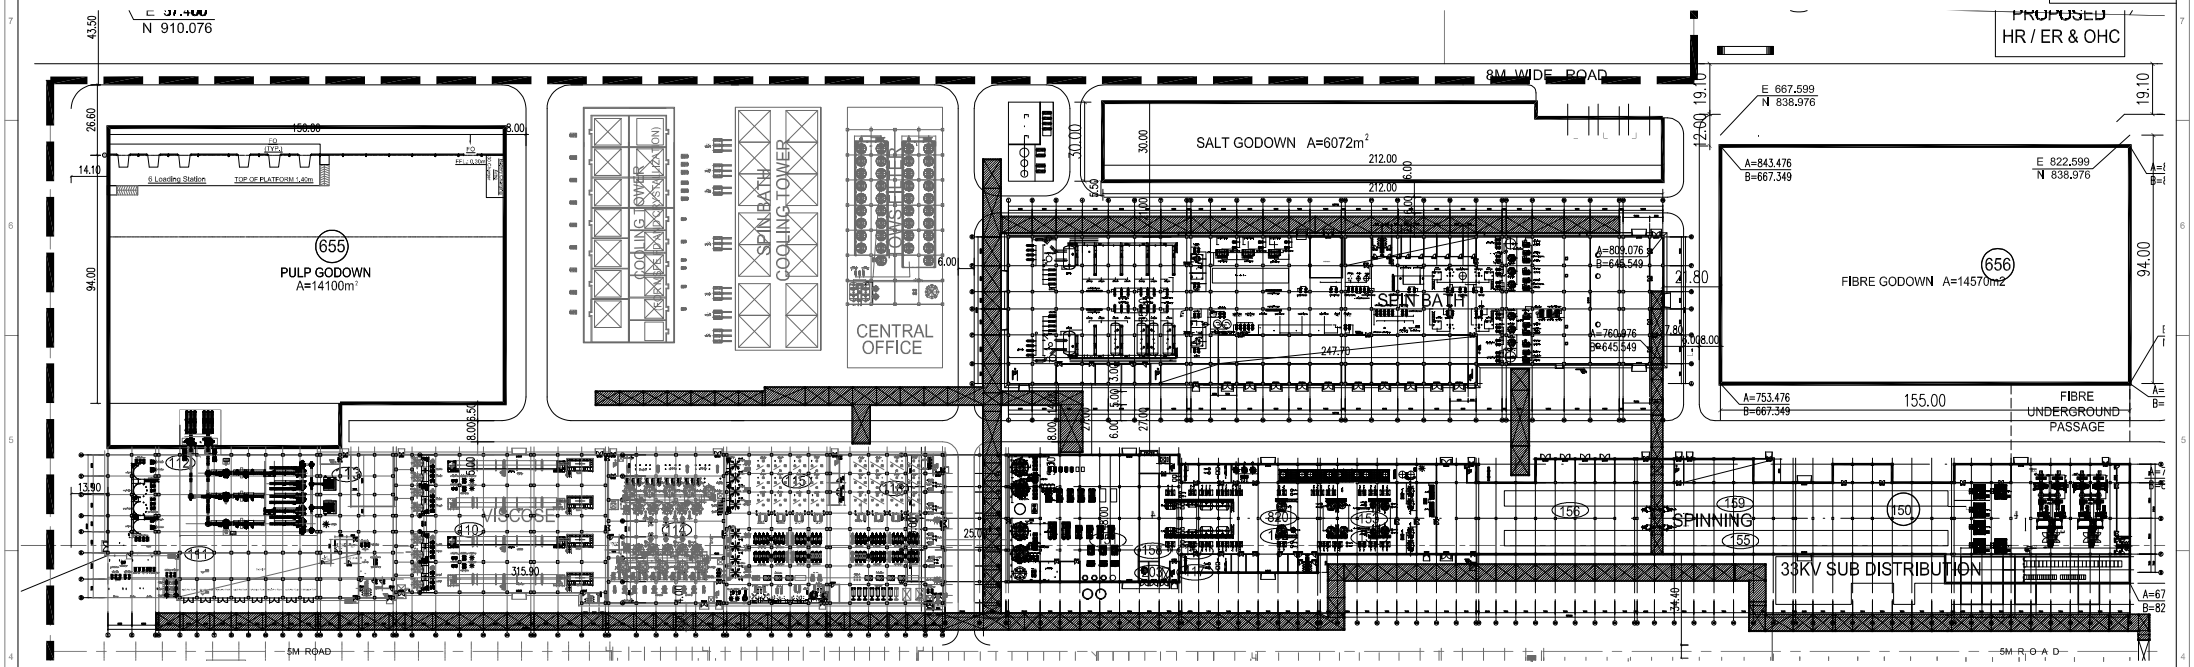

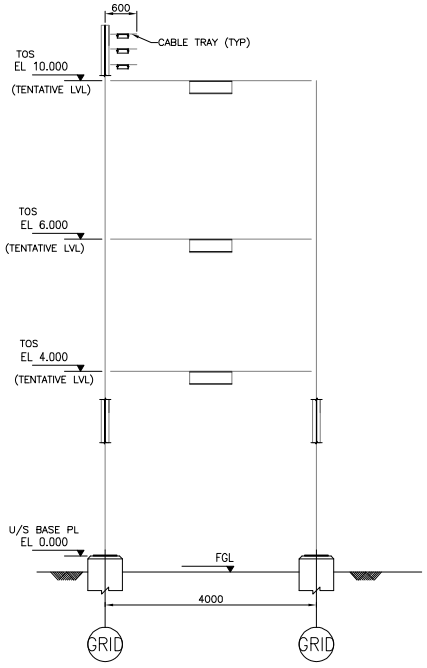

TYP PIPE RACK SECTION
SCALE 1:50

FOR TENDERING PURPOSE

REV. NO.	REVISION DESCRIPTION	DRAWN	CHK	APPROVED	CLIENT APPR.	DATE
–	–	–	–	–	–	
–	–	–	–	–	–	
–	–	–	–	–	–	
–	–	–	–	–	–	
–	–	–	–	–	–	

CLIENT
ADITYA BIRLA GRASIM
GRASIM CELLULOSIC
(A UNIT OF GRASIM INDUSTRIES LTD.)
VILAYAT, BHARUCH (GUJRAT)

BDEP CONSULTANT
MOVIN
MOVIN ENGINEERING CO., LTD

ADDRESS :-
–
–
–
–
–

THIS DRAWING AND/OR ITS CONTENTS, INFORMATION, AND PRINCIPLES OF DESIGN ARE THE EXCLUSIVE PROPERTY OF GRASIM CELLULOSIC, INDIA AND IS SUBMITTED TO YOU WITH THE AGREEMENT THAT IT IS NOT TO BE REPRODUCED IN ANY MANNER, COPIED, OR MODIFIED, NOR IS IT TO BE RELAYED IN PART OR IN WHOLE TO ANY OTHER FIRM OR INDIVIDUAL FOR ANY OTHER PROJECT EXCEPT BY WRITTEN AGREEMENT WITH GRASIM CELLULOSIC, INDIA.

JACOBS

JACOBS ENGINEERING INDIA PRIVATE LIMITED.
JACOBS HOUSE, RAMKRISHNA MANDIR ROAD,
KONDIVITA, ANDHERI (EAST), MUMBAI – 400059
TEL. +91-22-2681 2000


A MEMBER OF THE JACOBS ENGINEERING GROUP, INC.

GRASIM CELLULOSIC
VSF EXPANSION PROJECT


PIPE RACK

PROJ.NO.	DRAWING NO.		REV
44AC6500	44AC6500-000-C.01-XXXX-A1		A
DATE	FILE NAME	DRAWING SCALE / PLOT SCALE	DRAWN BY
29.05.18	44AC6500000C01XXXXA1A	1:150 / 1:1	SBK


A1

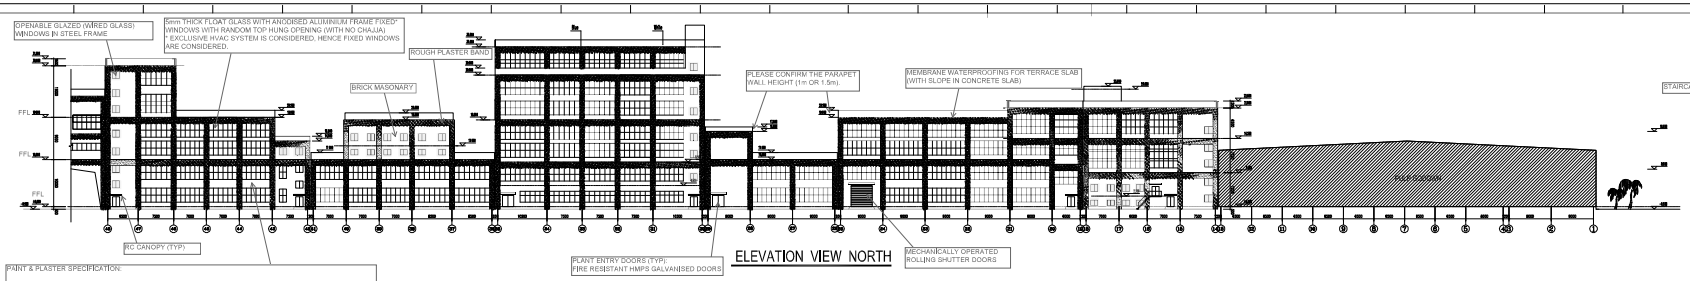


ELEVATION VIEW NORTH

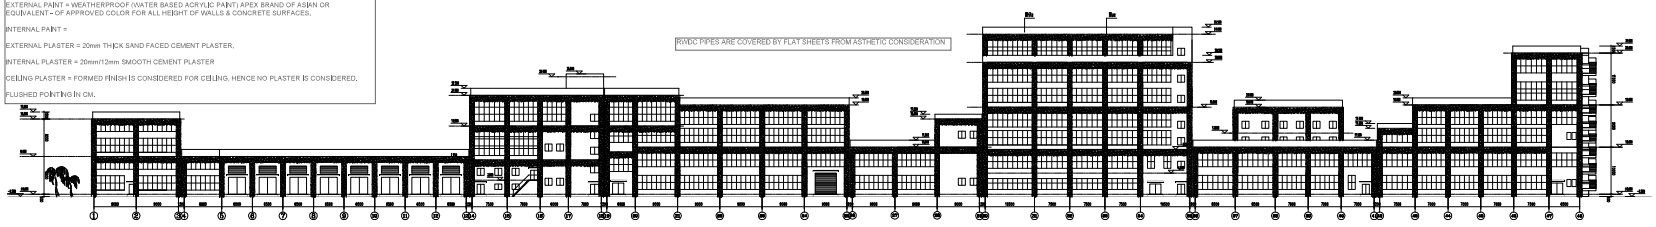

ELEVATION VIEW SOUTH

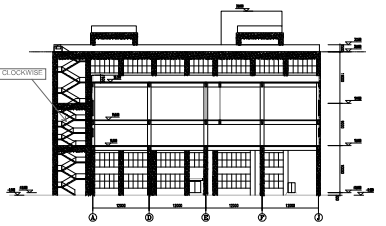


ELEVATION VIEW EAST

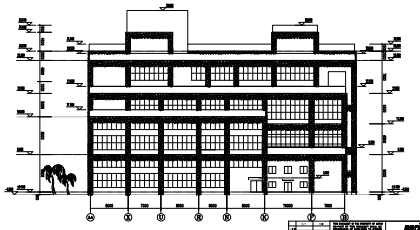


ELEVATION VIEW WEST

ELEVATIONS


DO NOT SCALE

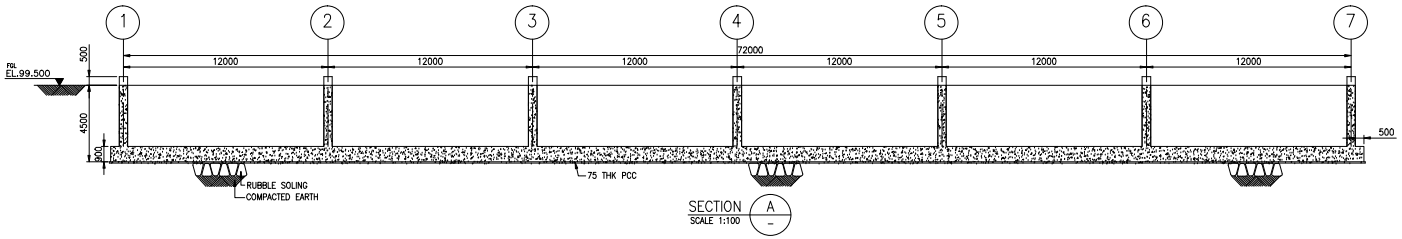


SECTION A
SCALE 1:100

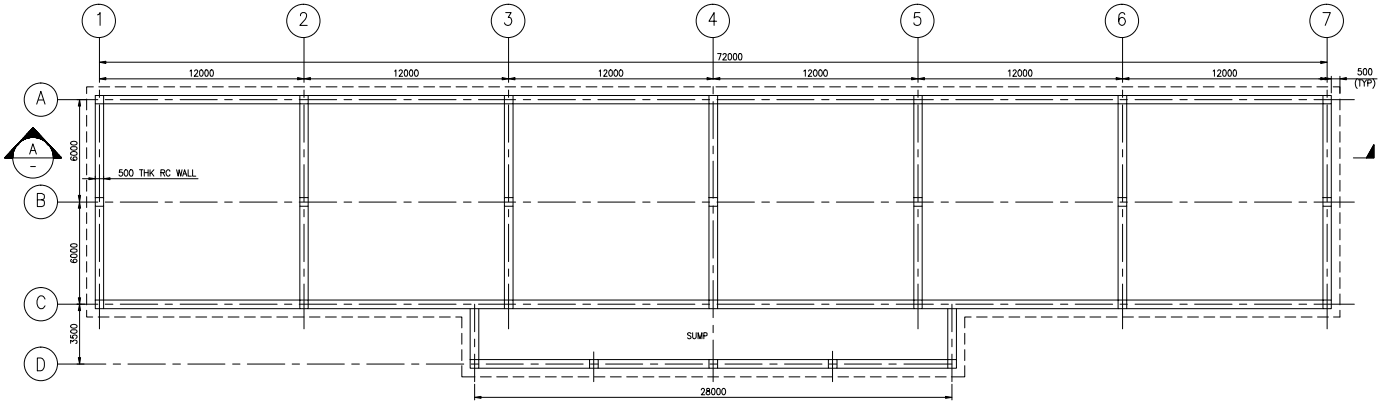

PLAN FOR MSFE
SCALE 1:150

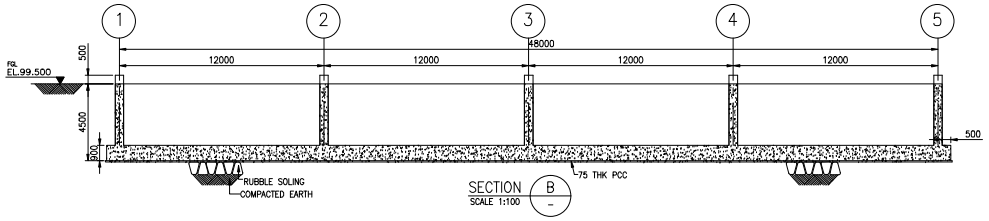

SECTION B
SCALE 1:100

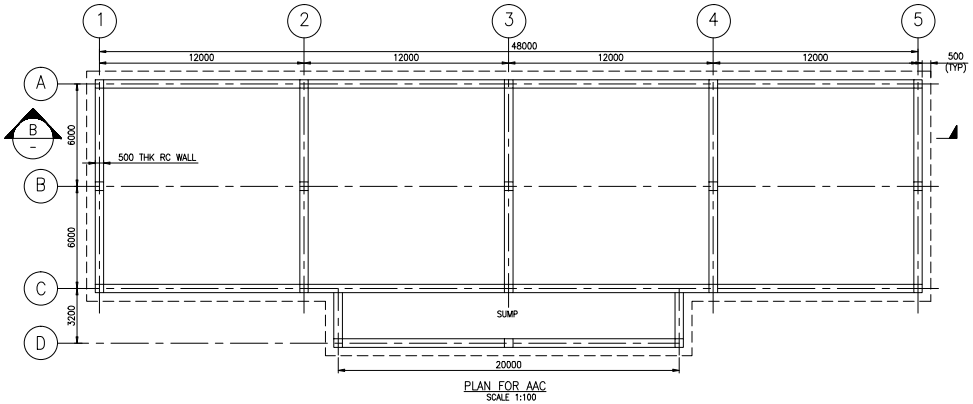

PLAN FOR AAC
SCALE 1:100

MEMBER SIZES

SR. NO.	DESCRIPTION	SIZES	
		WIDTH	DEPTH
1	RCC COLUMN	500	500
2	RC WALL THICKNESS	–	500
3	RAFT THICKNESS	–	900

NOTES:

1. ALL DIMENSIONS ARE IN mm AND LEVELS ARE IN METRES.
2. EL 100.000 CORRESPONDS TO RL 13.000.

FOR TENDER

REV. NO.	DESCRIPTION	DRAWN	CHK'D	APPROVED	CLIENT APPR.	DATE
–	–	–	–	–	–	–
–	–	–	–	–	–	–
–	–	–	–	–	–	–
–	–	–	–	–	–	–
–	–	–	–	–	–	–

CLIENT

ADITYA BIRLA GRASIM

GRASIM CELLULOSIC
(A UNIT OF GRASIM INDUSTRIES LTD.)
VILAYAT, BHARUCH (GUJRAT)

BDEP CONSULTANT

MOVIN
MOVIN ENGINEERING CO., LTD

JACOBS

JACOBS ENGINEERING INDIA PRIVATE LIMITED.
JACOBS HOUSE, RAMKRISHNA MANDIR ROAD,
KONDIVITA, ANDHERI (EAST), MUMBAI – 400059
TEL. +91-22-2681 2000

THIS DRAWING AND/OR ITS CONTENTS, INFORMATION, AND PRINCIPLES OF DESIGN ARETHE EXCLUSIVE PROPERTY OF GRASIM CELLULOSIC, INDIA AND IS SUBMITTED TO YOU WITH THE AGREEMENT THAT IT IS NOT TO BE REPRODUCED IN ANY MANNER, COPIED, OR MODIFIED, NOR IS IT TO BE RELAYED IN PART OR IN WHOLE TO ANY OTHER FIRM OR INDIVIDUAL FOR ANY OTHER PROJECT EXCEPT BY WRITTEN AGREEMENT WITH GRASIM CELLULOSIC, INDIA.


A MEMBER OF THE JACOBS ENGINEERING GROUP, INC.

GRASIM CELLULOSIC
BROWNFIELD VSF EXPANSION PROJECT
COOLING TOWER FOR MSFE & AAC
PLAN & SECTION

PROJ.NO.	DRAWING NO.		REV
–	–		–
DATE	FILE NAME	DRAWING SCALE	PLOT SCALE / DRAWN BY
–	–	–	1:1 / –

DO NOT SCALE

NORTH

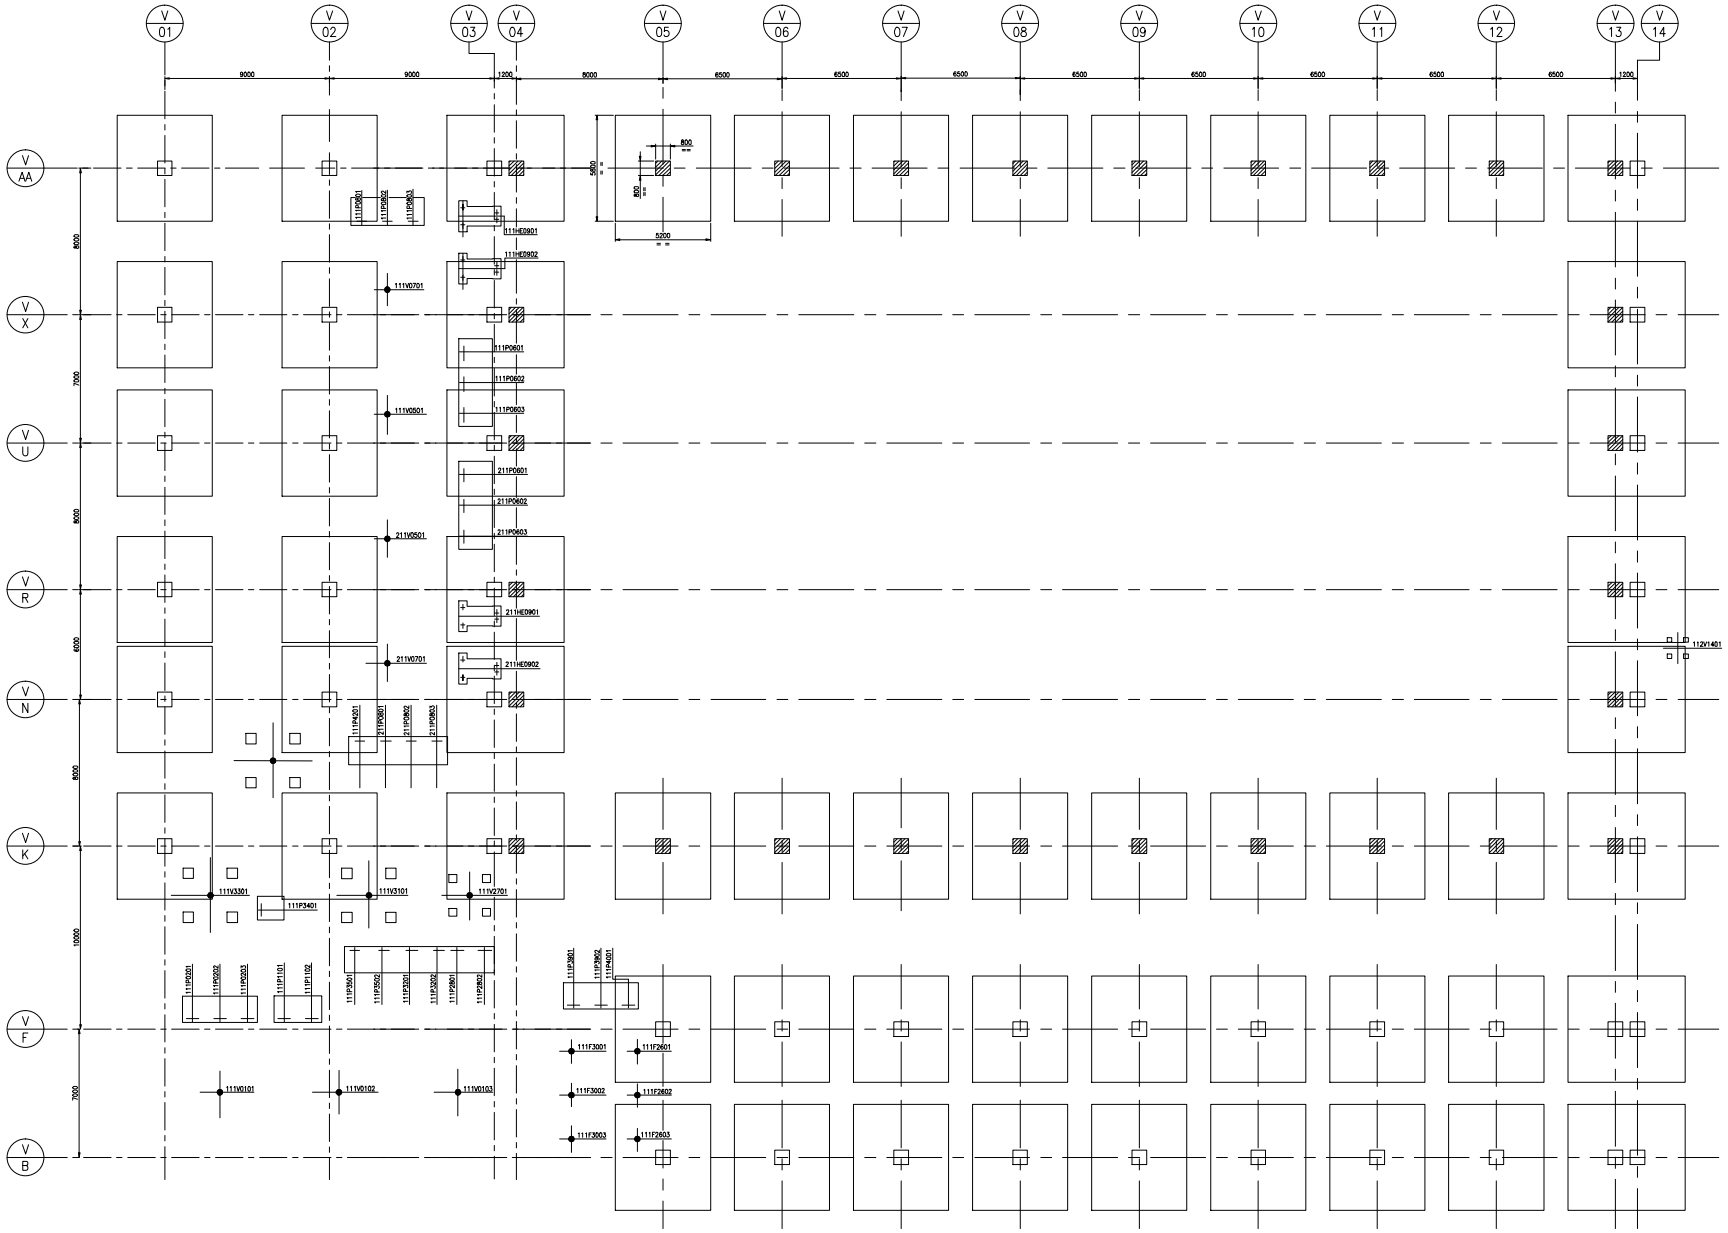

FOUNDATION LAYOUT
SCALE 1:100

THIS DWG SHALL BE READ IN-CONJUNCTION WITH C.01/XXXX/A2.

FOR TENDER

NOTES:-
1. ALL DIMENSIONS ARE IN mm AND ELEVATIONS IN m.
2. FOR GENERAL NOTES ON CONC. WORKS REF C.01/XXXX/A2.

BULK MTO:-

M25	223.0 m³
8 ϕ	0.0 t
10 ϕ	0.0 t
20 ϕ	0.0 t
25 ϕ	0.0 t
32 ϕ	0.0 t

REV. NO.	REVISION DESCRIPTION	DRAWN	CHK	APPROVED	CLIENT APPR.	DATE
A	ISSUED FOR APPROVAL	KSP	HM	KN		05/05/2022

CLIENT
ADITYA BIRLA GRASIM CELLULOSIC
(A UNIT OF GRASIM INDUSTRIES LTD.)
VILAYAT, BHARUCH (GUJRAT)

EPC CONSULTANT
MOVIN ENGINEERING CO., LTD
ADDRESS :-

THIS DRAWING AND/OR ITS CONTENTS, INFORMATION, AND PRINCIPLES OF DESIGN ARE THE EXCLUSIVE PROPERTY OF JACOBS ENGINEERING INDIA AND IS SUBMITTED TO YOU WITH THE UNDERSTANDING THAT IT WILL NOT BE COPIED, REPRODUCED, OR USED BY YOU OR ANY OTHER PERSON IT IS TO BE RELEASED IN PART OR IN WHOLE TO ANY OTHER FIRM OR INDIVIDUAL FOR ANY OTHER PROJECT EXCEPT BY WRITTEN AGREEMENT WITH GRASIM CELLULOSIC, INDIA.

JACOBS

JACOBS ENGINEERING INDIA PRIVATE LIMITED.
JACOBS HOUSE, RAMKRISHNA MANDIR ROAD,
KONDIVITA, ANDHERI (EAST), MUMBAI – 400059
TEL. +91-22-2681 3000


A MEMBER OF THE JACOBS ENGINEERING GROUP, INC.

GRASIM CELLULOSIC
VSF EXPANSION PROJECT
VISCOSE
L/O OF FDN BETWEEN GRIDS 01-13 & B TO AA


PROJECT	DRAWING NO.	REV
44AC8500	44AC8500-00/C.01/2101	A

DATE	FILE NAME	DRAWING SCALE	PLOT SCALE	DRAWN BY
XX.XX.XXXX	C_01_2101	1:100	1:1	RSP


DO NOT SCALE

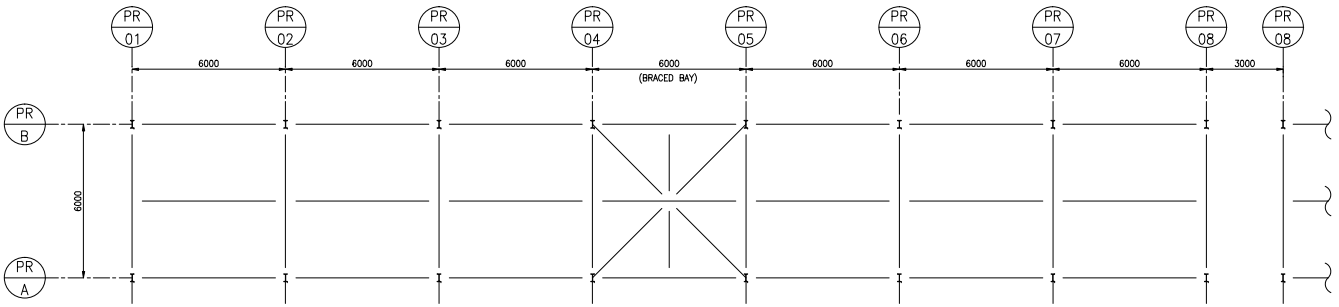

PLAN AT TOS EL. 105.500, 109.500 & 113.500
SCALE-1:100

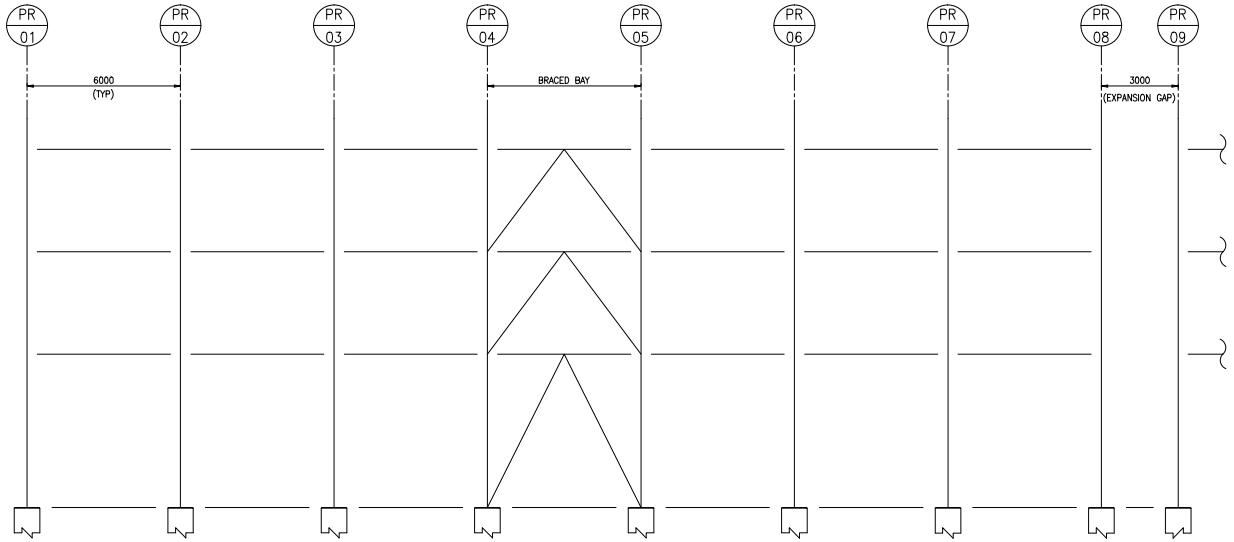

TYP LONGITUDINAL ELEVATION
SCALE-1:100 (LOOKING NORTH)

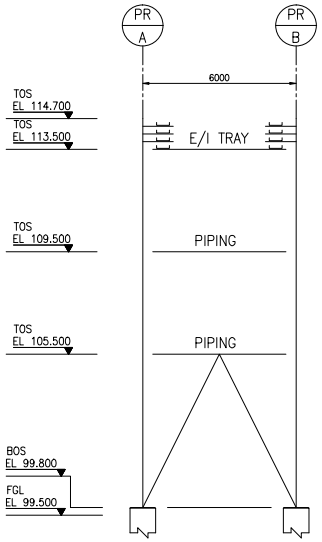

TYP CROSS SECTION
SCALE-1:100 (LOOKING NORTH)

FOR TENDER

NOTES:

1) ALL DIMENSIONS ARE IN mm & LEVELS ARE IN m.
2) EL 100.000 CORRESPONDS TO RL 13.000

REV. NO.	DESCRIPTION	DRAWN	CHK'D	APPROVED	CLIENT APPR.	DATE
–	–	–	–	–	–	–
–	–	–	–	–	–	–
–	–	–	–	–	–	–
–	–	–	–	–	–	–
–	–	–	–	–	–	–

CLIENT

ADITYA BIRLA GRASIM

GRASIM CELLULOSIC
(A UNIT OF GRASIM INDUSTRIES LTD.)
VILAYAT, BHARUCH (GUJRAT)

BDEP CONSULTANT

MOVIN
MOVIN ENGINEERING CO., LTD

JACOBS

JACOBS ENGINEERING INDIA PRIVATE LIMITED.
JACOBS HOUSE, RAMKRISHNA MANDIR ROAD,
KONDIVITA, ANDHERI (EAST), MUMBAI – 400059
TEL. +91-22-2681 2000


THIS DRAWING AND/OR ITS CONTENTS, INFORMATION, AND PRINCIPLES OF DESIGN ARETHE EXCLUSIVE PROPERTY OF GRASIM CELLULOSIC, INDIA AND IS SUBMITTED TO YOU WITH THE AGREEMENT THAT IT IS NOT TO BE REPRODUCED IN ANY MANNER, COPIED, OR MODIFIED, NOR IS IT TO BE RELAYED IN PART OR IN WHOLE TO ANY OTHER FIRM OR INDIVIDUAL FOR ANY OTHER PROJECT EXCEPT BY WRITTEN AGREEMENT WITH GRASIM CELLULOSIC, INDIA.

A MEMBER OF THE JACOBS ENGINEERING GROUP, INC.


GRASIM CELLULOSIC
VILAYAT BROWNFIELD VSF EXPANSION PROJECT
PIPE RACK
FRAMMING PLANS AND ELEVATIONS
–

PROJ.NO.	DRAWING NO.		REV
–	–		–
DATE	FILE NAME	DRAWING SCALE	PLOT SCALE / DRAWN BY
		–	1:1 / –


DO NOT SCALE

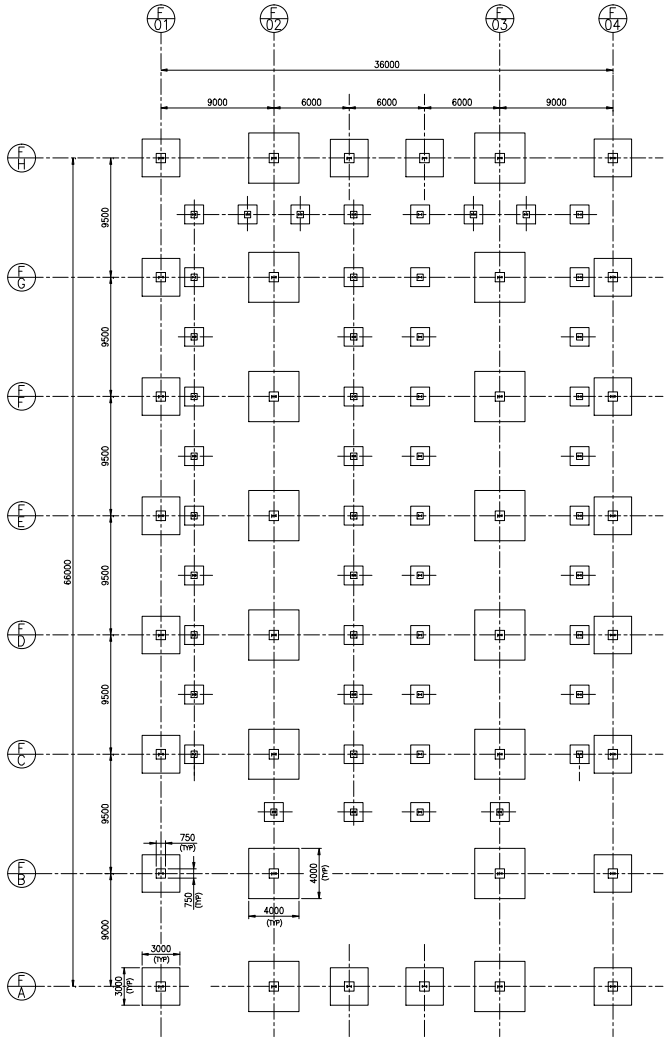

TOWS FILTER STRUCTURE LAYOUT
SCALE 1:200

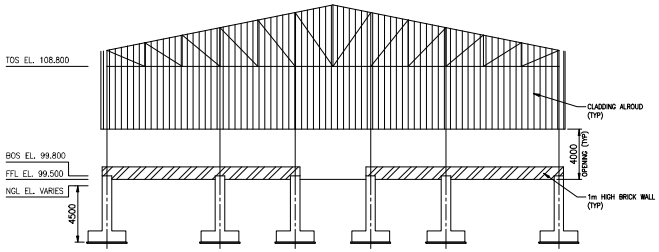

ELEVATION ALONG GRID F A & F H
SCALE 1:200

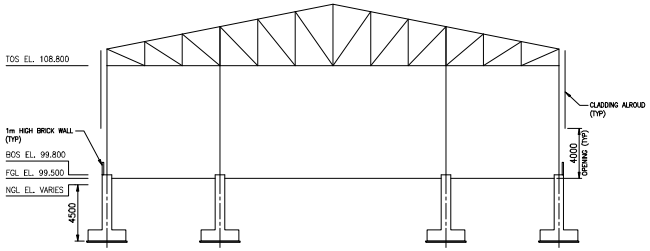

ELEVATION ALONG GRID F B & F C
SCALE 1:200

FOR TENDER

REV. NO.	DESCRIPTION	DRAWN	CHK'D	APPROVED	CLIENT APPR.	DATE
–	–	–	–	–	–	
–	–	–	–	–	–	
–	–	–	–	–	–	
–	–	–	–	–	–	
–	–	–	–	–	–	
–	–	–	–	–	–	

CLIENT
ADITYA BIRLA GRASIM
GRASIM CELLULOSIC
(A UNIT OF GRASIM INDUSTRIES LTD.)
VILAYAT, BHARUCH (GUJRAT)

BDEP CONSULTANT
MOVIN
MOVIN ENGINEERING CO., LTD

JACOBS
JACOBS ENGINEERING INDIA PRIVATE LIMITED.
JACOBS HOUSE, RAMKRISHNA MANDIR ROAD,
KONDIVITA, ANDHERI (EAST), MUMBAI – 400059
TEL. +91-22-2681 2000

THIS DRAWING AND/OR ITS CONTENTS, INFORMATION, AND PRINCIPLES OF DESIGN ARETHE EXCLUSIVE PROPERTY OF GRASIM CELLULOSIC, INDIA AND IS SUBMITTED TO YOU WITH THE AGREEMENT THAT IT IS NOT TO BE REPRODUCED IN ANY MANNER, COPIED, OR MODIFIED, NOR IS IT TO BE RELAYED IN PART OR IN WHOLE TO ANY OTHER FIRM OR INDIVIDUAL FOR ANY OTHER PROJECT EXCEPT BY WRITTEN AGREEMENT WITH GRASIM CELLULOSIC, INDIA.

A MEMBER OF THE JACOBS ENGINEERING GROUP, INC.

GRASIM CELLULOSIC
VILAYAT BROWNFIELD VSF EXPANSION PROJECT
SPINBATH AREA
TOWS FILTER STRUCTURE
–

PROJ.NO.	DRAWING NO.		REV
–	–		–
DATE	FILE NAME	DRAWING SCALE / PLOT SCALE	DRAWN BY
		– / 1:1	–

DO NOT SCALE

TYPE OF INSERT PLATE	THK OF IP (mm) / DIA OF LUGS (ø)	DETAILS OF INSERT PLATE		SHEAR & MOMENT			SHEAR & TENSION		UNIT WT. (Kg.)	
		PLAN	CROSS SECTION	SHEAR (t)	MOMENT ABOUT (tm) Mx	MOMENT ABOUT (tm) My	SHEAR (t)	TENSION (t)	PLATE	LUGS.
A1a	12	SIZE 150x150	300	4.75	0.15	0.15	4.75	5.0	2.1	1.05
A1b	16			8.95	0.2	0.2	8.95	6.5	2.8	1.9
A2a	12	SIZE 200x200	300	4.75	0.25	0.25	4.75	5.0	3.9	1.05
A2b	16			8.95	0.3	0.3	8.95	6.5	5.0	1.9
A3a	12	SIZE 250x250	300	7.15	0.5	0.35	7.1	7.6	5.9	2.1
A3b	16			13.4	0.7	0.45	13.4	9.8	7.85	3.75
A4a	12	SIZE 300x300	350	6.7	0.75	0.5	6.7	8.85	8.5	2.5
A4b	16			13.0	0.95	0.6	13.0	10.0	11.3	4.45
A5a	12	SIZE 350x350	350	6.7	0.95	0.6	6.7	8.85	11.55	2.65
A5b	16			13.0	1.05	0.7	13.0	10.0	15.4	4.7
A6a	12	SIZE 400x400	350	6.7	1.1	0.75	6.7	8.85	15.0	2.75
A6b	16			13.0	1.3	0.85	13.0	10.0	15.0	4.95

TYPE OF INSERT PLATE	THK OF IP (mm) / DIA OF LUGS (ø)	DETAILS OF INSERT PLATE		SHEAR & MOMENT			SHEAR & TENSION		UNIT WT. (Kg.)	
		PLAN	CROSS SECTION	SHEAR (t)	MOMENT ABOUT (tm) Mx	MOMENT ABOUT (tm) My	SHEAR (t)	TENSION (t)	PLATE	LUGS.
B1a	12	SIZE 150x200	300	4.75	0.25	0.15	4.75	5.0	2.85	1.05
B1b	16			8.95	0.3	0.2	8.95	6.5	3.75	1.9
B2a	12	SIZE 200x300	350	4.35	0.75	0.3	4.35	5.9	5.65	1.65
B2b	16			8.85	0.85	0.75	8.85	6.65	7.55	1.85
B3a	12	SIZE 200x400	350	4.35	0.75	0.3	4.35	5.9	7.55	1.85
B3b	16			8.85	0.85	0.75	8.85	6.65	10.05	3.3
B4a	12	SIZE 250x400	350	6.7	0.75	0.6	6.7	8.85	9.4	2.4
B4b	16			13.0	0.85	0.7	13.0	10.0	12.55	4.2
B5a	12	SIZE 250x500	400	8.1	1.3	1.0	8.1	13.5	11.8	3.5
B5b	16			16.7	1.65	1.3	16.7	18.0	15.7	6.25
B6a	12	SIZE 300x400	350	6.7	0.75	0.75	6.7	8.85	11.3	2.5
B6b	16			13.0	0.85	0.85	13.0	10.0	15.05	4.45

NOTES:–

1. ALL DIMENSIONS ARE IN mm AND ELEVATIONS ARE IN m.
2. ALL LUGS SHALL BE OF 12 & 16 ø HYSD BARS CONFORMING TO IS–1786 AND SHALL BE CONNECTED TO INSERT PLATES BY 6 mm FILLET WELDS AS SHOWN IN SKETCHES.
3. MS INSERT PLATES (12 /16 mm THK) CONFORMING TO IS–2062 SHALL BE USED.
4. INSERT PLATES SHALL BE MKD ON DWG AS UNDER:–
   IP–B2b AT EL. 100.500
   (ELEVATION OF IP (TOP EDGE); TYPE OF IP)
5. INSERT PLATES SHALL BE KEPT FLUSH WITH CONCRETE SURFACE.
6. UNLESS NOTED THE LONGER SIDE OF THE IP SHALL BE VERTICAL.
7. MOMENT, SHEAR & TENSILE CAPACITIES ARE DERATED BY 25% TO ALLOW FOR SITE WELDING & WORKMANSHIP.


HOLD LIST:–

NIL


BULK MTO:–


NOT APPLICABLE

FOR TENDER

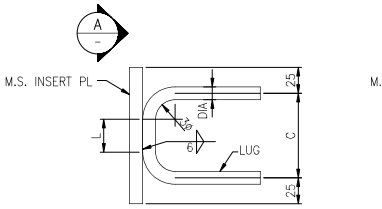


BENDING DIMENSION FOR 12/16 DIA LUGS
(WHEN C > 200)

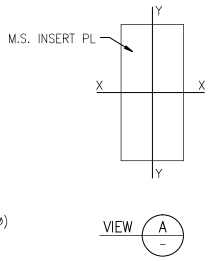

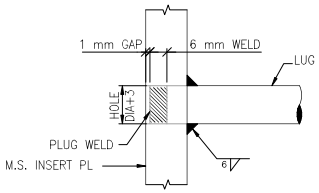

WELD DET. OF 12/16 DIA LUGS W/ IP
(WHEN C < 200)

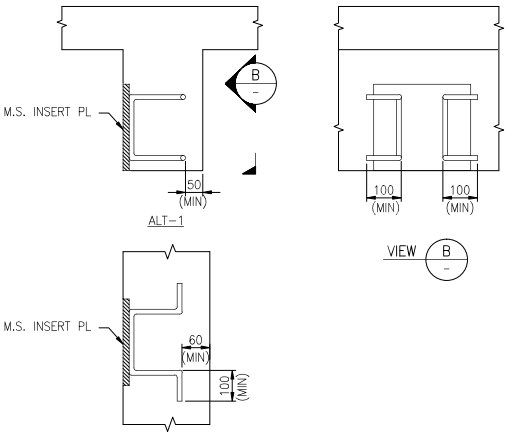

ALTERNATE LUG ARRANGEMENT
(FOR MEMBERS WHERE CONCRETE DIMENSIONS ARE RESTRICTED)

REV. NO.	DESCRIPTION	DRAWN	CHK'D	APPROVED	CLIENT APPR.	DATE
–	–	–	–	–	–	——
–	–	–	–	–	–	——
–	–	–	–	–	–	——
–	–	–	–	–	–	——
A	ISSUED FOR TENDER	KSP	US	EN	–	XX.XX.XXXX

CLIENT

ADITYA BIRLA GRASIM

GRASIM CELLULOSIC

(A UNIT OF GRASIM INDUSTRIES LTD.)
VILAYAT, BHARUCH (GUJRAT)

BDEP CONSULTANT

MOVIN ENGINEERING CO., LTD

JACOBS

JACOBS ENGINEERING INDIA PRIVATE LIMITED.
JACOBS HOUSE, RAMKRISHNA MANDIR ROAD,
KONDIVITA, ANDHERI (EAST), MUMBAI – 400059
TEL. +91–22–2681 2000 .

THIS DRAWING AND/OR ITS CONTENTS, INFORMATION, AND PRINCIPLES OF DESIGN ARETHE EXCLUSIVE PROPERTY OF GRASIM CELLULOSIC, INDIA AND IS SUBMITTED TO YOU WITH THE AGREEMENT THAT IT IS NOT TO BE REPRODUCED IN ANY MANNER, COPIED, OR MODIFIED, NOR IS IT TO BE RELAYED IN PART OR IN WHOLE TO ANY OTHER FIRM OR INDIVIDUAL FOR ANY OTHER PROJECT EXCEPT BY WRITTEN AGREEMENT WITH GRASIM CELLULOSIC, INDIA.


A MEMBER OF THE JACOBS ENGINEERING GROUP, INC.

GRASIM CELLULOSIC
VILAYAT VSF EXPANSION PROJECT
STANDARD INSERT PLATE DETAILS
–
–

PROJ.NO.	DRAWING NO.		REV
44AC6500	44AC6500/00/C.01/1503		A
DATE	FILE NAME	DRAWING SCALE / PLOT SCALE	DRAWN BY
XX.XX.XXXX	C.01 1503	1:100 / 1:1	KSP


A2

DO NOT SCALE

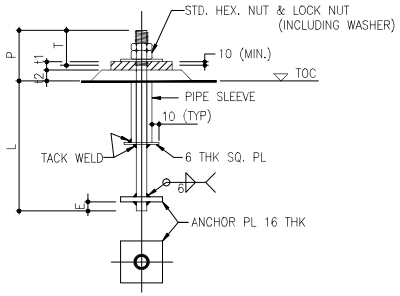


DIA OF BOLT	L	ANCHOR PL	PIPE SLEEVE	E	CAPACITY IN 'kN'	
					TENSION	SHEAR
M20	575	60 SQ.	50 NB x 300 LG.	20	24.5	25.1
M24	650	75 SQ.	80 NB x 300 LG.	25	35.3	36.2
M30	875	100 SQ.	80 NB x 450 LG.	30	56.1	56.5
M33	925	100 SQ.	80 NB x 450 LG.	35	69.4	68.4
M36	1075	110 SQ.	80 NB x 450 LG.	40	81.7	81.4
M42	1350	120 SQ.	100 NB x 450 LG.	45	112.0	110.8

ANCHOR BOLT TYPE "K"

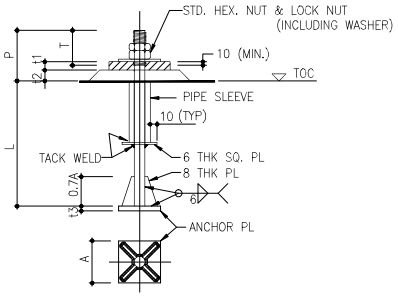

DIA OF BOLT	L	ANCHOR PL		PIPE SLEEVE	CAPACITY IN 'kN'	
		A	t3		TENSION	SHEAR
M36	675	160 SQ.	16	80 NB x 450 LG.	81.7	81.4
M42	700	200 SQ.	20	100 NB x 450 LG.	112.0	110.8
M48	750	200 SQ.	25	100 NB x 450 LG.	147.0	144.5
M56	750	240 SQ.	25	125 NB x 450 LG.	203.0	197.0

ANCHOR BOLT TYPE "L"

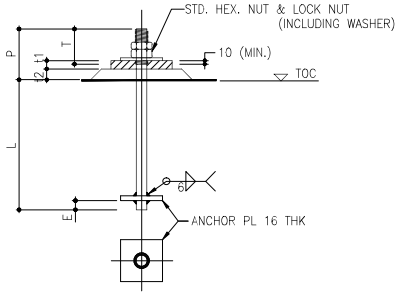

DIA OF BOLT	L	ANCHOR PL	E	CAPACITY IN 'kN'	
				TENSION	SHEAR
M12	350	50 SQ.	20	8.8	9.0
M16	450	50 SQ.	20	15.7	16.0
M20	575	60 SQ.	20	24.5	25.1
M24	650	75 SQ.	25	35.3	36.2
M30	875	100 SQ.	30	56.1	56.5

ANCHOR BOLT TYPE "M"

BOLT DESIGNATION


e.g. 4 – K – M20 – N1 – 90

- 90 — PROJECTION ABOVE ROUGH CONCRETE
- N1 — SINGLE NUT (N1) OR DOUBLE NUT (N2)
- M20 — DIAMETER OF BOLT
- K — TYPE OF BOLT
- 4 — NO OF BOLTS

t1 = BASE PLATE THICKNESS (VARIES)
t2 = GROUT THICKNESS (VARIES)
T = THREADED LENGTH = (2D+20) FOR SINGLE NUT
= (3D+20) FOR DOUBLE NUT
P = T+t1+t2–10 (ROUND TO NEAREST 5 mm)

UNLESS NOTED, ANCHOR BOLTS COVERED IN THIS DWG. CONFORMS TO,

a) ANCHOR BOLTS (RODS) SHALL BE OF PROPERTY CLASS 4.6 & NUTS OF PROPERTY CLASS 4.
b) BOLTS SHALL BE TURNED FROM M.S. ROUNDS CONFORMING TO IS 2062 GRADE–A & IS 432 GRADE–I.
c) NUTS AND WASHERS SHALL CONFORM TO IS 1363 & IS 3138.
d) THREADING SHALL BE COARSE CONFORMING TO IS 1367 & IS 4218.
e) SLEEVE SHALL BE M.S. TUBES (MEDIUM) AS PER IS 1239.
ANCHOR BOLT SHALL BE TEMPERED BEFORE MACHINING IF MADE BY FORGING. THE FORGING
TEMPERATURE SHALL BE ABOVE 900°C BUT LOWER THAN SUPER HEATING TEMPERATURE.

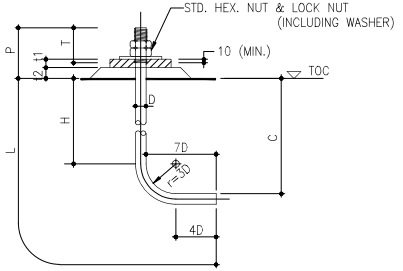

DIA OF BOLT	L	H	C	CAPACITY IN 'kN'	
				TENSION	SHEAR
M10	295	200	230	5.8	6.2
M12	354	240	276	8.4	9.0
M16	502	350	398	15.7	16.0
M20	615	424	485	24.5	25.0
M24	748	520	592	35.3	36.0

ANCHOR BOLT TYPE "J"

NOTES
1. FOR GENERAL NOTES REFER DWGS.
CONC. DWG. : 18–3293–00/C.01/1061/A2
STRUCTURAL DWG. : 18–3293–00/S.01/1062/A2

HOLD LIST
NIL

BULK MTO
NOT APPLICABLE

FOR TENDER

REV. NO.	DESCRIPTION	DRAWN	CHK'D	APPROVED	CLIENT APPR.	DATE
–	–	–	–	–	–	——
–	–	–	–	–	–	——
–	–	–	–	–	–	——
–	–	–	–	–	–	——
A	ISSUED FOR TENDER	KSP	US	EN	–	XX.XX.XXXX

CLIENT
ADITYA BIRLA GRASIM
GRASIM CELLULOSIC
(A UNIT OF GRASIM INDUSTRIES LTD.)
VILAYAT, BHARUCH (GUJRAT)

BDEP CONSULTANT
MOVIN ENGINEERING CO., LTD

JACOBS
JACOBS ENGINEERING INDIA PRIVATE LIMITED.
JACOBS HOUSE, RAMKRISHNA MANDIR ROAD,
KONDIVITA, ANDHERI (EAST), MUMBAI – 400059
TEL. +91–22–2681 2000

THIS DRAWING AND/OR ITS CONTENTS, INFORMATION, AND PRINCIPLES OF DESIGN ARETHE EXCLUSIVE PROPERTY OF GRASIM CELLULOSIC, INDIA AND IS SUBMITTED TO YOU WITH THE AGREEMENT THAT IT IS NOT TO BE REPRODUCED IN ANY MANNER, COPIED, OR MODIFIED, NOR IS IT TO BE RELAYED IN PART OR IN WHOLE TO ANY OTHER FIRM OR INDIVIDUAL FOR ANY OTHER PROJECT EXCEPT BY WRITTEN AGREEMENT WITH GRASIM CELLULOSIC, INDIA.


A MEMBER OF THE JACOBS ENGINEERING GROUP, INC.

GRASIM CELLULOSIC
VILAYAT VSF EXPANSION PROJECT
STANDARD ANCHOR BOLT DETAILS
–
–

PROJ.NO.	DRAWING NO.			REV
44AC6500	44AC6500/00/C.01/1506			A
DATE	FILE NAME	DRAWING SCALE	PLOT SCALE	DRAWN BY
XX.XX.XXXX	C.01 1506	1:100	1:1	KSP

A2

IF IN DOUBT, ASK. | PL. DO NOT SCALE

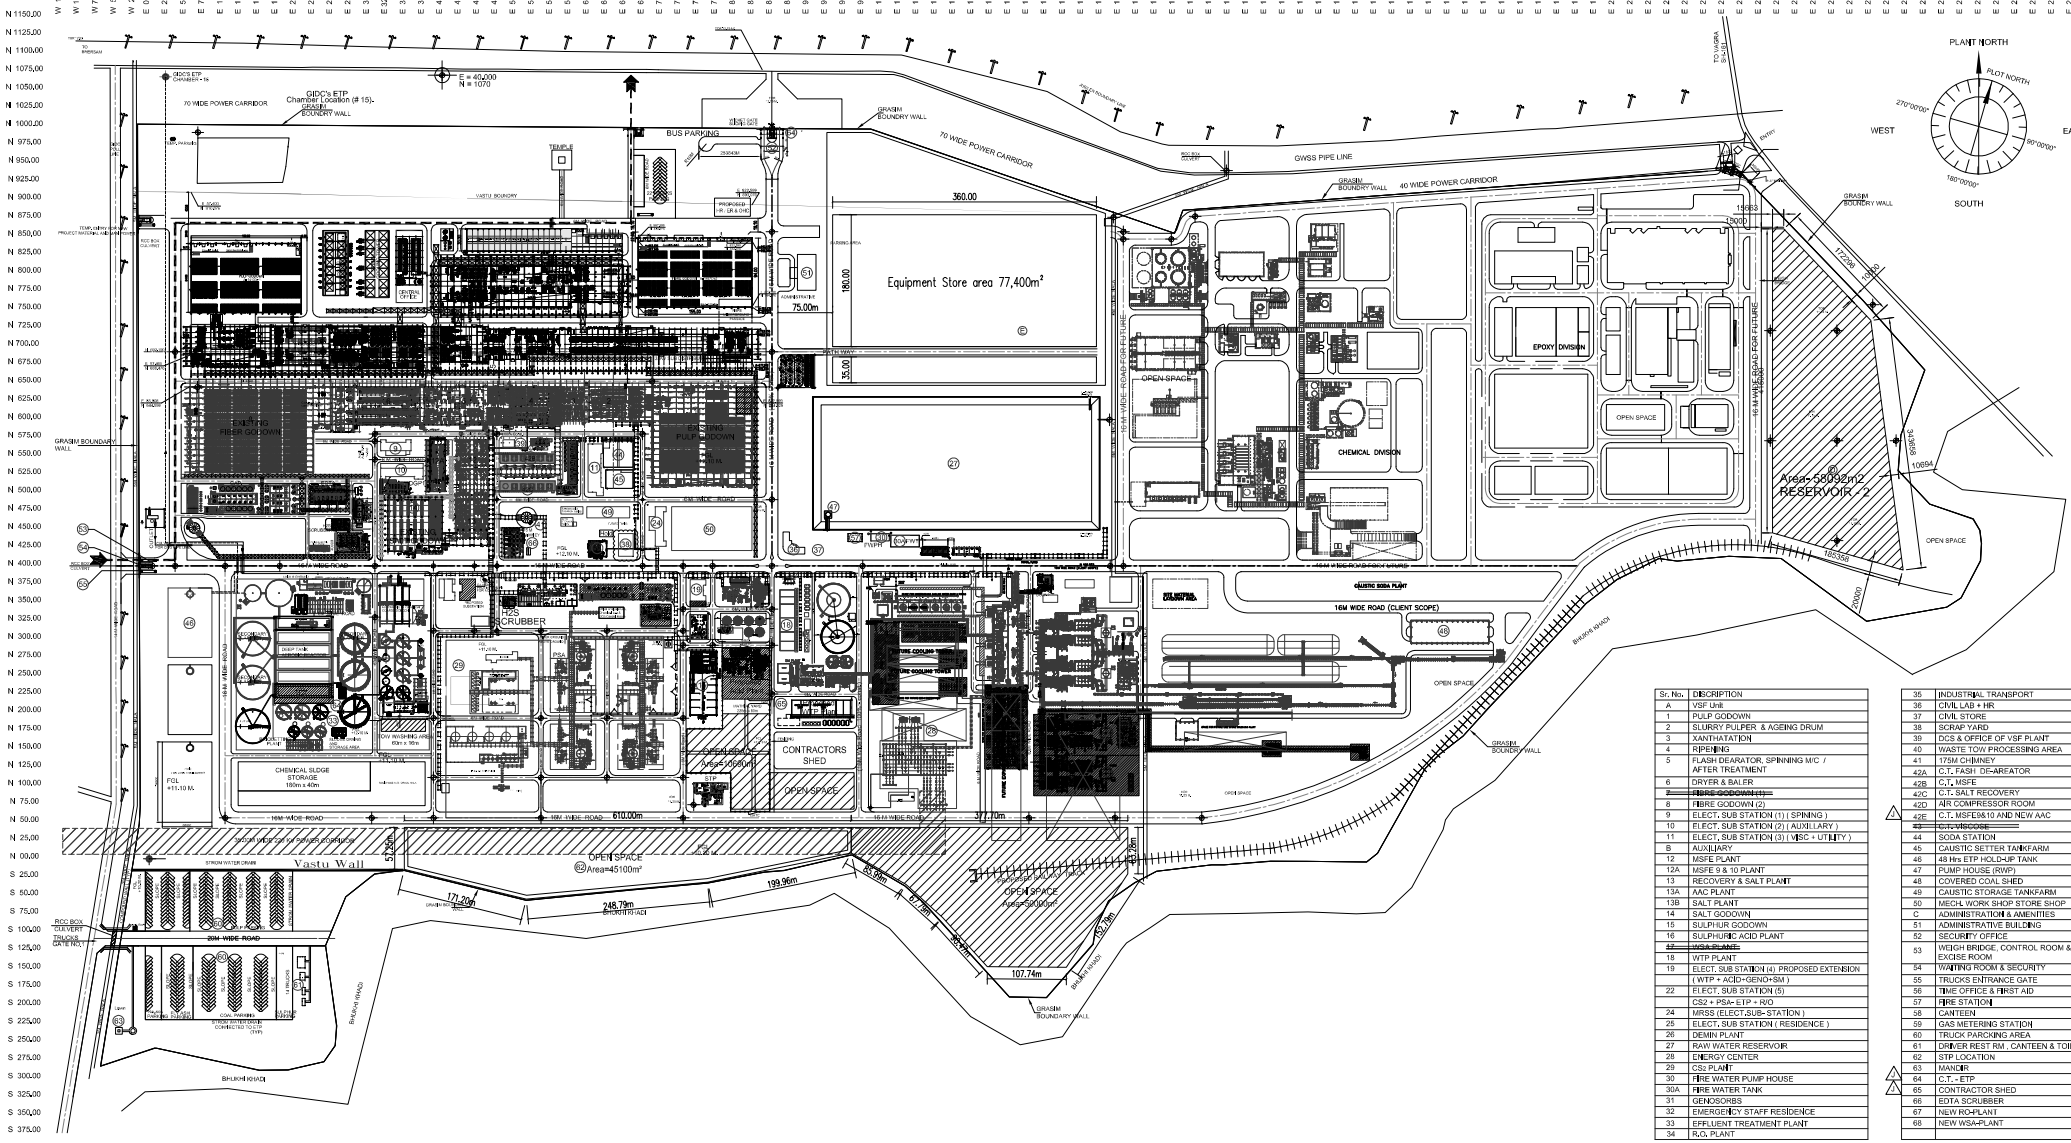

Sr. No.	DESCRIPTION
A	VSF Unit
1	PULP GODOWN
2	SLURRY PULPER & AGEING DRUM
3	XANTHATATION
4	RIPENING
5	FLASH DEARATOR, SPINNING M/C / AFTER TREATMENT
6	DRYER & BALER
~~7~~	~~FIBRE GODOWN (1)~~
8	FIBRE GODOWN (2)
9	ELECT. SUB STATION (1) (SPINING)
10	ELECT. SUB STATION (2) (AUXILLARY)
11	ELECT. SUB STATION (3) (VISC + UTILITY)
B	AUXILIARY
12	MSFE PLANT
12A	MSFE 9 & 10 PLANT
13	RECOVERY & SALT PLANT
13A	AAC PLANT
13B	SALT PLANT
14	SALT GODOWN
15	SULPHUR GODOWN
16	SULPHURIC ACID PLANT
~~17~~	~~HCSA PLANT~~
18	WTP PLANT
19	ELECT. SUB STATION (4) PROPOSED EXTENSION (WTP + ACID+GENO+SM)
22	ELECT. SUB STATION (5)
	CS2 + PSA+ ETP + R/O
24	MRSS (ELECT.SUB-STATION)
25	ELECT. SUB STATION (RESIDENCE)
26	DEMIN PLANT
27	RAW WATER RESERVOIR
28	ENERGY CENTER
29	CS2 PLANT
30	FIRE WATER PUMP HOUSE
30A	FIRE WATER TANK
31	GENOSORBS
32	EMERGENCY STAFF RESIDENCE
33	EFFLUENT TREATMENT PLANT
34	R.O. PLANT

35	INDUSTRIAL TRANSPORT
36	CIVIL LAB + HR
37	CIVIL STORE
38	SCRAP YARD
39	DCS & OFFICE OF VSF PLANT
40	WASTE TOW PROCESSING AREA
41	175M CHIMNEY
42A	C.T. FASH DE-AREATOR
42B	C.T. MSFE
42C	C.T. SALT RECOVERY
42D	AIR COMPRESSOR ROOM
42E	C.T. MSFE9&10 AND NEW AAC
~~43~~	~~C.T. VISCOSE~~
44	SODA STATION
45	CAUSTIC SETTER TANKFARM
46	48 Hrs ETP HOLD-UP TANK
47	PUMP HOUSE (RWP)
48	COVERED COAL SHED
49	CAUSTIC STORAGE TANKFARM
50	MECH. WORK SHOP STORE SHOP
C	ADMINISTRATION & AMENITIES
51	ADMINISTRATIVE BUILDING
52	SECURITY OFFICE
53	WEIGH BRIDGE, CONTROL ROOM & EXCISE ROOM
54	WAITING ROOM & SECURITY
55	TRUCKS ENTRANCE GATE
56	TIME OFFICE & FIRST AID
57	FIRE STATION
58	CANTEEN
59	GAS METERING STATION
60	TRUCK PARCKING AREA
61	DRIVER REST RM , CANTEEN & TOILET AREA
62	STP LOCATION
63	MANDIR
64	C.T. - ETP
65	CONTRACTOR SHED
66	EDTA SCRUBBER
67	NEW RO-PLANT
68	NEW WSA-PLANT

Notes
1. All Dimensions are in Meters.
2. No Dimension are to be Scaled of the Drawing. Only written Dimensions are to be Followed.
3. All Drawings are inter related & shall be read in conjunction with Individual Utility Drawings, for the exact location & sizes of all Proposed Utilities & Equipments.

FOR TENDERING PURPOSE

REV	DATE	DESCRIPTION	DRAWN	CHKD.	APPD.
P0	01.04.18	Plot Plan revised after China visit			

MAT.:	QTY.:	TOTAL Wt. IN Kgs.	
PLOT PLAN OF GRASIM CELLULOSIC DIVISION VILAYAT	DATE	12.12.2017	SIGN:
	DRAWN		
	CHECKED		
	APPROVED		
REF: 278668(V)-APE-02	F.NO:	SCALE: NTS	

GRASIM CELLULOSIC
(A UNIT OF GRASIM INDUSTRIES LTD.)
VILAYAT, BHARUCH (GUJRAT)

DWG. NO.:					REV:
0	GC	CVL	01	001	P0

This Drawing/tech. document is the property of Grasim Cellulosic Division, Vilayat, must not be copied in whole or part or lent out without their written permission.