




Opening Direction

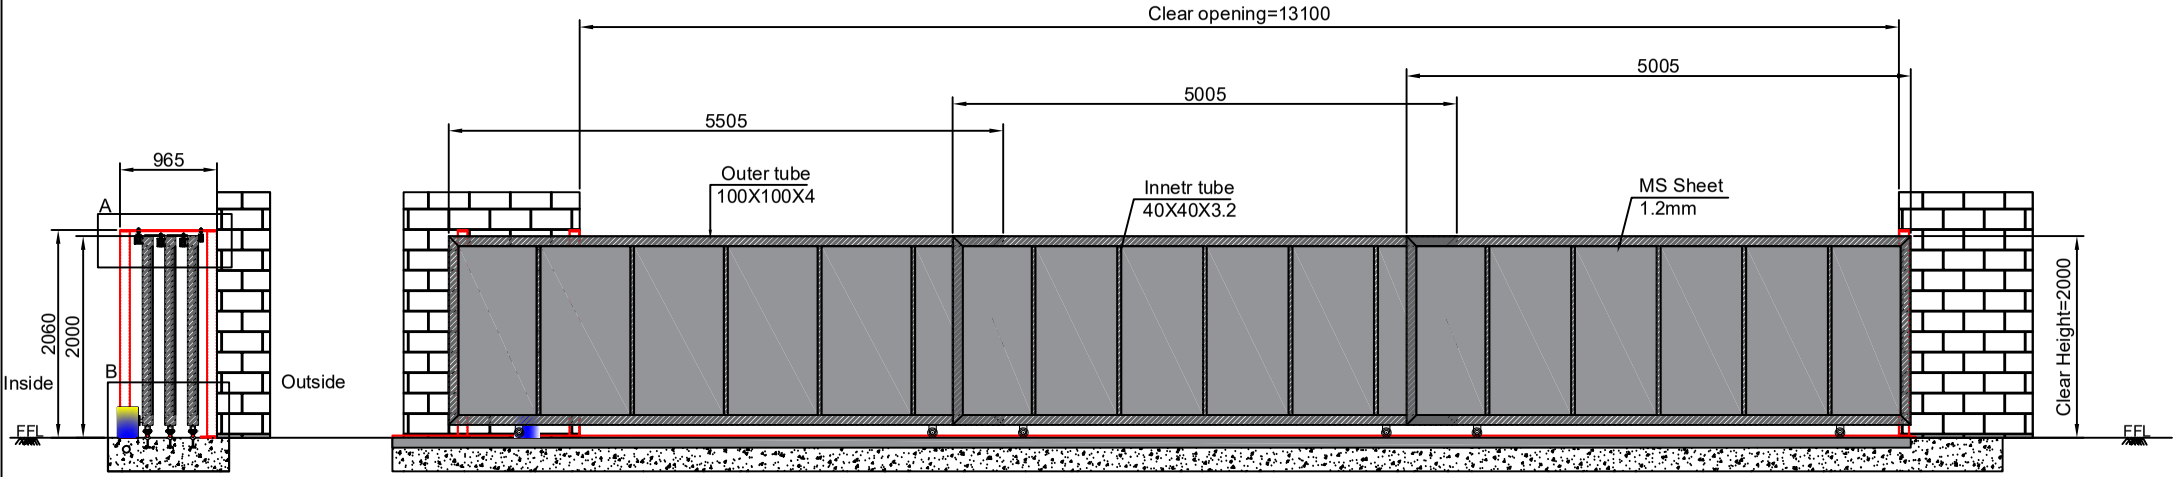

Opening Direction

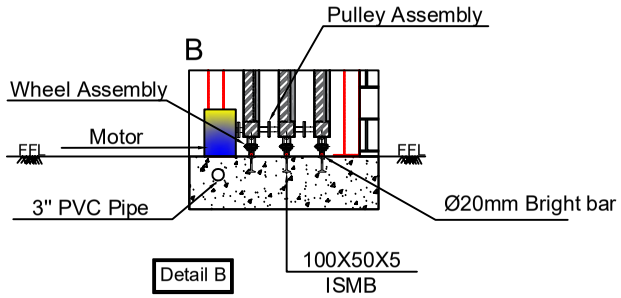

Detail B

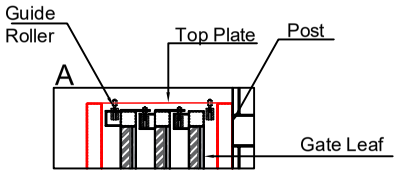

Detail A

Note:-

1.All Dimension are in MM.

2.All Civil work will be in Client scope

3.Civil,Installation and Fabrication Tolerance will be ±20mm

4.Reuired Parking will be 5610mm

5.Coating: Approved RAL 9010

This drawing & design is the property of NIHVA TECHNOLOGIES. Not to be sold or copied to any other concern.

TITLE:- 3L Telescopic Sliding Gate (E17,WH)

NIHVA TECHNOLOGIES PVT. LTD.

NIHVA TECHNOLOGIES PVT. PUNE
Tel : 020 66304033
Email:- info@nihva.com
Website:- www.nihva.com

	NAME	DATE	SIGN
DRAWN	SUJATA	19/07/2022	
CHECK	M.S	19/07/2022	
APPRD.	A.K	19/07/2022	

If any queries contact : design@nihva.com

ALL DIMENSION ARE IN mm

CLIENT - OC Specialities

LOCATION - Solapur

PRODUCT - Telescopic Sliding Gate | QTY-01

DWG NO:- NIHVA/22-23/CLT/0051_1 | REV- 01

SCALE: NTS | SCALE:-- 1:1 | SHEET: 01 OF 01

Rev No.	Revision	Date	Revised By
1.	Opening has been changed from 12800mm to 13100mm	19/07/2022	Sujata