
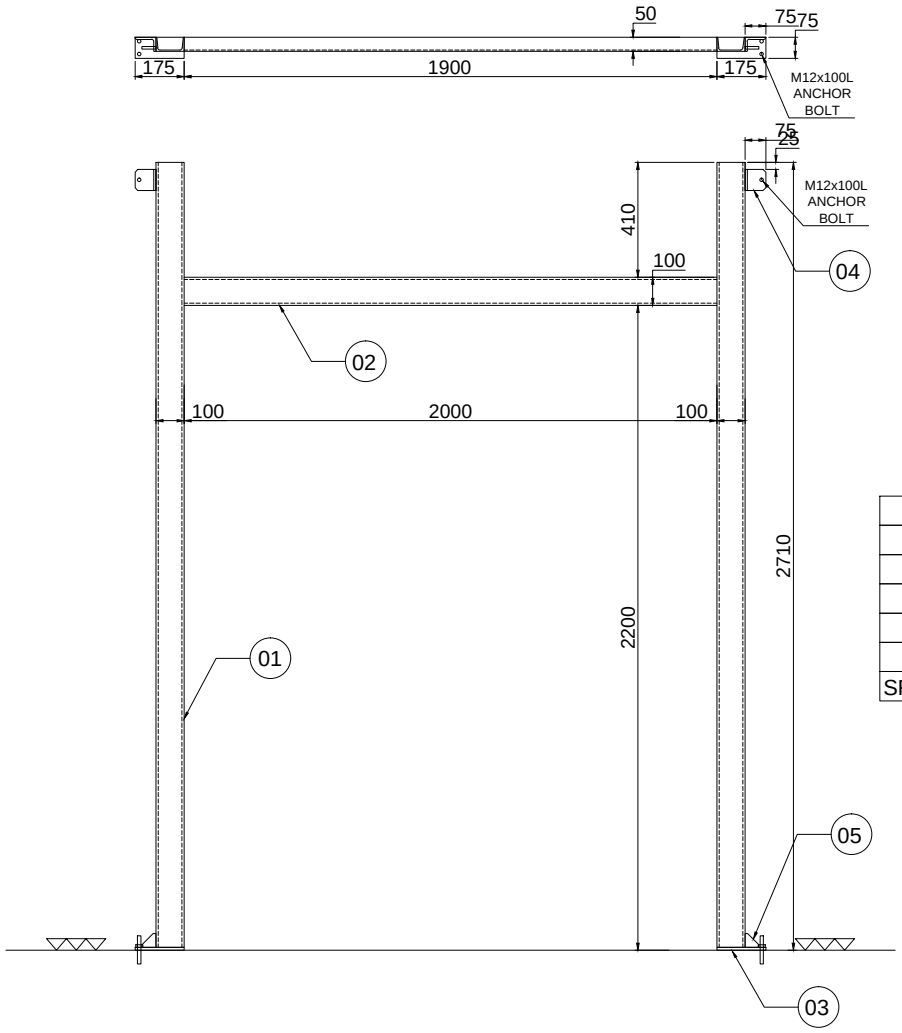


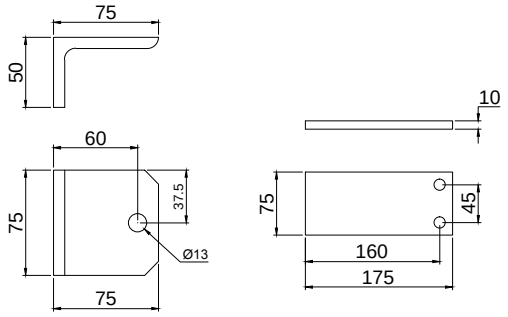

06	ANCHOR BOLT	M12 X 100L	6 NOS
05	RIB	50 X 10 X 50L	2 NOS
04	ISA	75 X 8 X 75L	2 NOS
03	FLAT	75 X 10 X 175L	2 NOS
02	ISMC	100 X 50 X 2000L	1 NO
01	ISMC	100 X 50 X 2700L	2 NOS
SR.NO	DESCRIPTION	SPECIFICATION	QTY

RAL COLOR - RAL 7001

NOTE : USE R. TUBE 96 X 48 X 4.8 THK IF IN STOCK.

NOTE : USE OLD STRUCTURE DO THE REQUIRED MODIFICATION AS PER ABOVE DRAWING.

This drawing & designing is the property of NIHVA TECHNOLOGIES. Not to be sold or copied to any other concern.

TITLE
HIGH SPEED DOOR
HS9020GHY STRUCTURE.

NIHVA
NIHVA TECHNOLOGIES PVT. LTD.
NIHVA TECHNOLOGIES PVT. LTD. PUNE
Tel : 020 66304033
Email:- info@nihva.com
Website:- www.nihva.com

	NAME	SIGN	DATE
DRAWN	P.A		22.01.20
CHECK	G.J		22.01.20
APPROVAL			

CLIENT -

PROJECT -

SITE -

If any queries contact : design@nihva.com

DWG. NO. : NIHVA/19-20/VDR/289 REV- 00

ALL DIMENSION ARE IN mm

SCALE: NTS WT: SHEET: 01 OF 01