

SHUTTER TYPE	HIGH QUALITY 2HRS FIRE SHUTTERS
SHUTTER SLATS	1.0 mm ZINCALUME STEEL SOLID SLATES
FINISHING OF SLATS	POWER COAT STANDARD RAL COLOUR
GUIDE RAIL	GALVANIZED ,3mm THICK
FINISHING OF GUIDE	POWDER COAT STANDARD RAL COLOUR
BOTTOM BAR	T-120
FINISHING OF B/BAR	POWDER COAT STANDARD RAL COLOUR
BOX DESIGN	MILD STEEL SECTION FRAME DESIGN
FINISHING OF BOX	POWDER COAT STANDARD RAL COLOUR
BOX COVER PLATE	0.8mm ZINCALUME STEEL SHEET
FINISHING OF COVER	POWDER COAT STANDARD RAL COLOUR
OPERATION	MOTORIZE WITH MANUAL OVERRIDE CHAIN
MOTOR POWER SOURCE	230 VOLTS,1 PHASE,50HZ
FIRE MODE	THERMAL FUSIBLE LINK WILL AUTO CLOSE BY GRAVITY FORCE WHWN ROOM TEMP RISES UP TO 71°C ERS-EMERGENCY RELEASE SYSTEMS READY TO RECEIVED24VDC FIRE SIGNAL FROM FIRE CONTROL ROOM AND SHUTTER SHALL CLOSE DOWN BY GRAVITY FORCE WITHOUT DELAY
ADDITIONAL ITEM	

LOCATION	SHUTTER NO.	CLEAR WIDTH (STRUCTURE)	CLEAR HEIGHT (STRUCTURE)	QUANTITY	MOTOR POSITION
	FRS	3000 mm	3000mm	02 NOS	RH


COLOR
1.WHITE (RAL 9010) ☐
2.GREY (RAL 7025) ☐

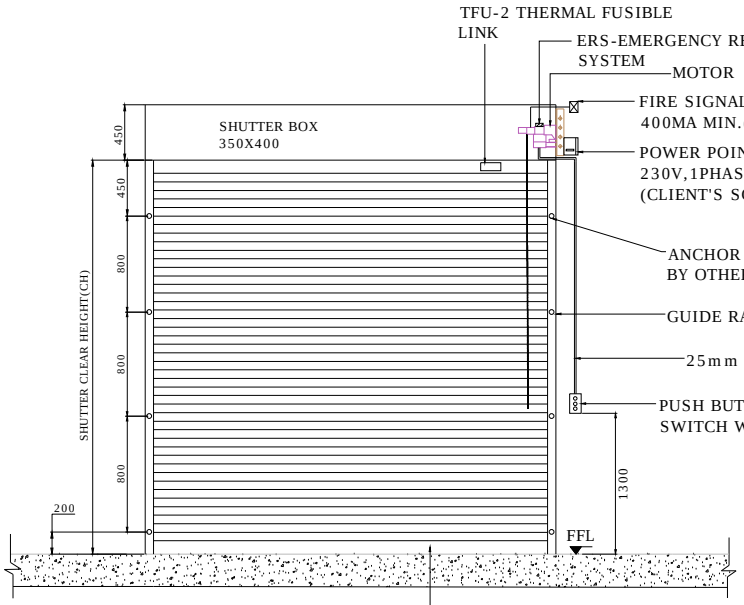


ELEVATION VIEW

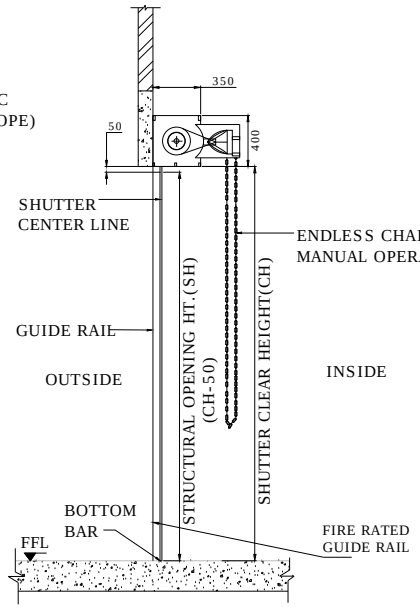


SIDE VIEW

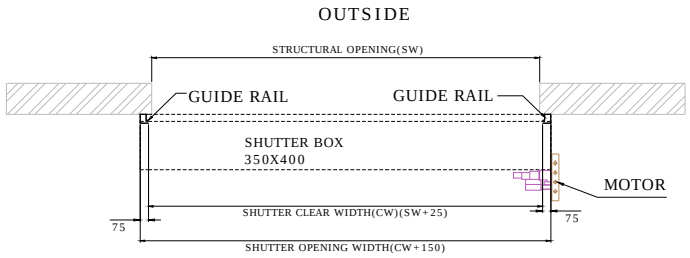


INSIDE
PLAN VIEW

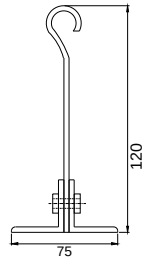


FIRE RATED BOTTOM BAR

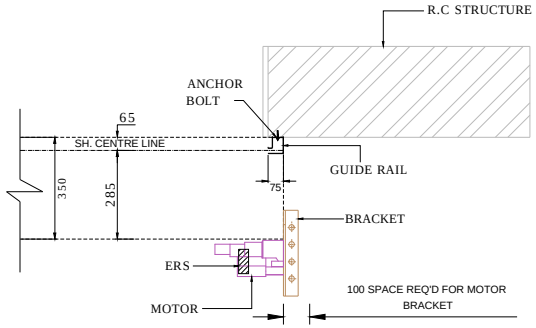


GUIDE & MOTOR ASSEMBLY DETAILS

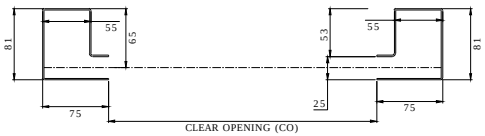

GALVANISED STEEL GUIDE RAIL
THICKNESS 3mm

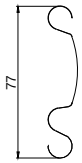

SHUTTER SLAT

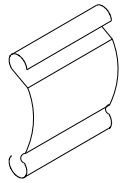

NOTE:-CLIENT SHOULD MENTION COLOR FOR SHUTTER

This drawing & designing is the property of NIHVA TECHNOLOGIES. Not to be sold or copied to any other concern.

TITLE: FIRE RATED ROLLING SHUTTER

NIHVA TECHNOLOGIES PVT. LTD. PUNE
Tel : 020 66304033
Email:- info@nihva.com
Website:- www.nihva.com

	NAME	SIGN	DATE
DRAWN	SURAJ		21/08/18
CHECK	PRADEEP		21/08/18
APPROVAL	R.D		21/08/18

CLIENT - DEVI CONSTRUCTION
PROJECT -
SITE - PUNE

If any queries contact : design@nihva.com
DWG. NO. : NIHVA/18-19/0107 REV. - 0
ALL DIMENSION ARE IN mm
SCALE: NTS WT: SHEET: 01 OF 01