
MAINTENANCE STOPPER

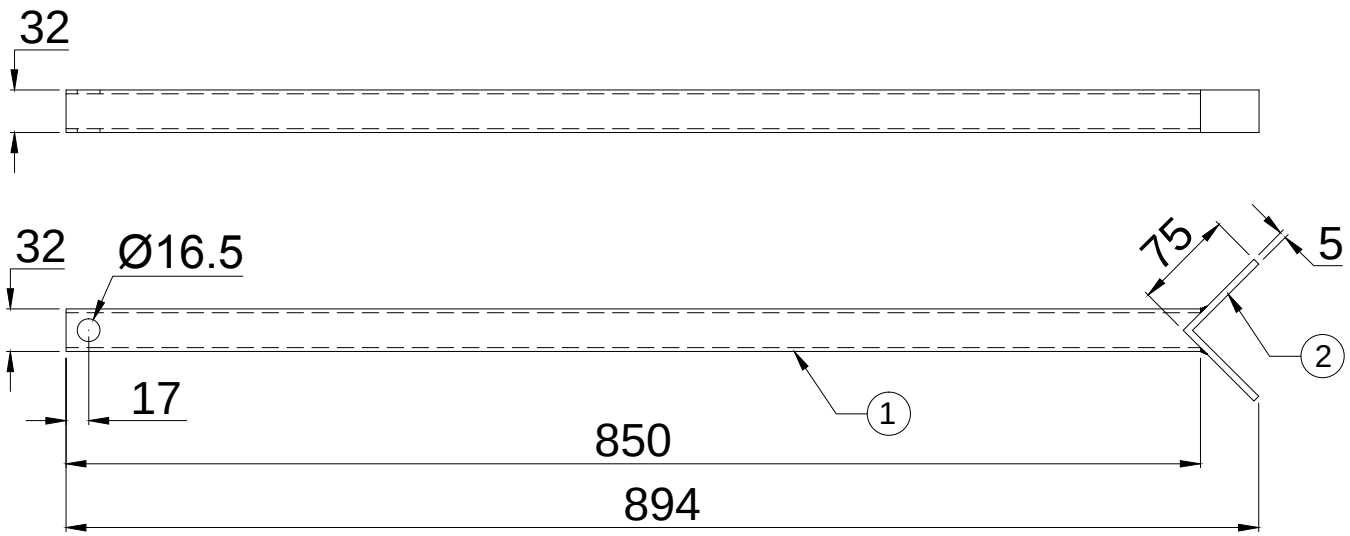

1. SQ .TUBE 32 X 32 X 3 THK X 850L = 2 NOS
2. ISA 75 X 75 X 5 X 32L = 2 NOS

SR NO	CLEAR WIDTH	QTY.
1	mm	NOS

TOLERANCE - ±5mm

This drawing & design is the property of NIHVA TECHNOLOGIES. Not to be sold or copied to any other concern.

TITLE			
MAINTENANCE STOPPER DRG			NIHVA TECHNOLOGIES PVT. LTD.
NAME	SIGN	DATE	
DRAWN P.A			CLIENT -
CHECK SHEKHAR			PROJECT - DLBJ1001
APPRD. SHEKHAR			SITE LOCATION -
If any queries contact : design@nihva.com			DWG. NO. : NIHVA/17-18/ REV- 0
ALL DIMENSION ARE IN mm			SCALE: NTS WT: SHEET: 01 OF 01

NIHVA TECHNOLOGIES PVT. LTD. PUNE
Tel : 020 66304033
Email:- info@nihva.com
Website:- www.nihva.com