
MS STRUCTURE FOR MRS 4000 X 4500

QTY- 2 NO

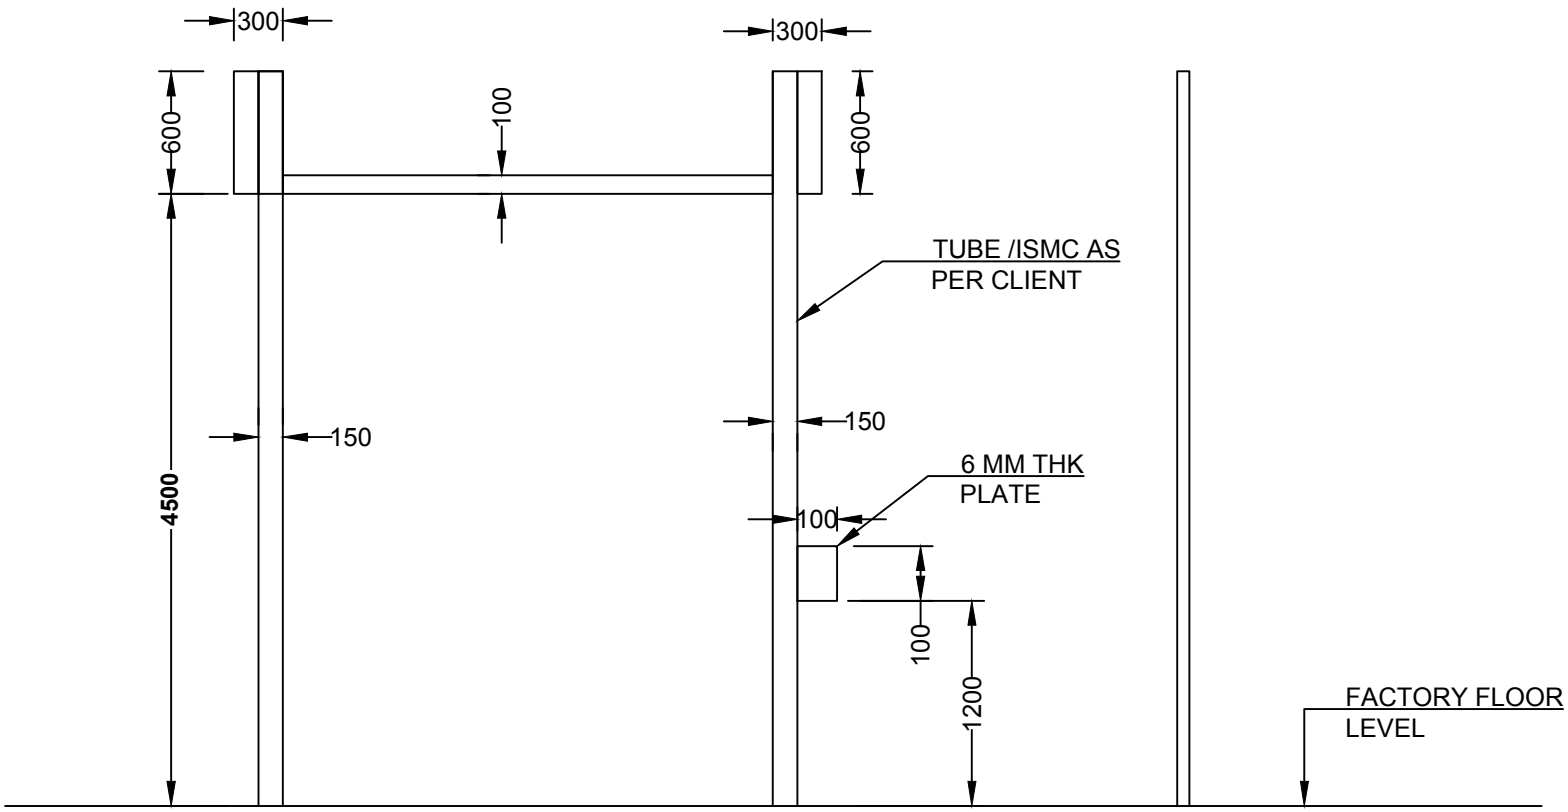

NOTES-

1. REQUIRED M.S. STRUCTURE , FITTING & ALL CIVIL WORK IS IN CLIENT SCOPE .
2. STRUCTURE SHOULD BE RIGID & NEED TO BE FIXED/WELDED WITH EXISTING STRUCTURE AT SITE BY CLIENT .

This drawing & design is the property of NIHVA TECHNOLOGIES. Not to be sold or copied to any other concern

TITLE	MS STRUCTURE FOR MRS 4000x4500			NIHVA TECHNOLOGIES PVT. LTD. PUNE Tel : 020 66304033 Email:- info@nihva.com Website:- www.nihva.com
	NAME	SIGN	DATE	
DRAWN	SMS		13.5.21	CLIENT :- ARP CONSTRUCTION
CHECK	SMS		13.5.21	PROJECT :- JOHN DEERE
APPV'ED				LOCATION :- PUNE
If any queries contact : design@nihva.com				DWG. NO. :- NIHVA/21-22/006/MRS REV.:- 01
ALL DIMENSION ARE IN mm				SCALE: NTS WT: SHEET: 01 OF 01