


Revision	Date	By
A New measurements, doors redrawn	2022-10-10	EB

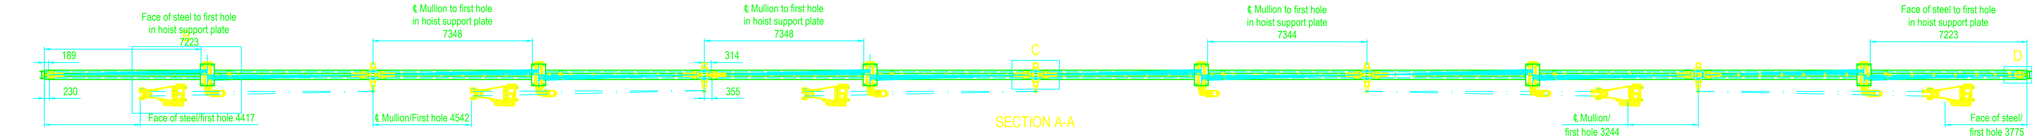


SECTION A-A

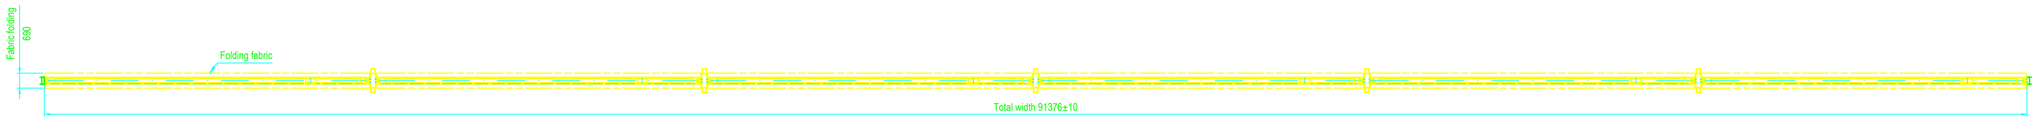


SECTION B-B

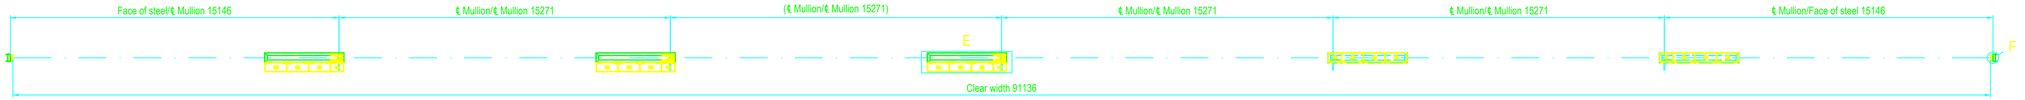


SECTION C-C

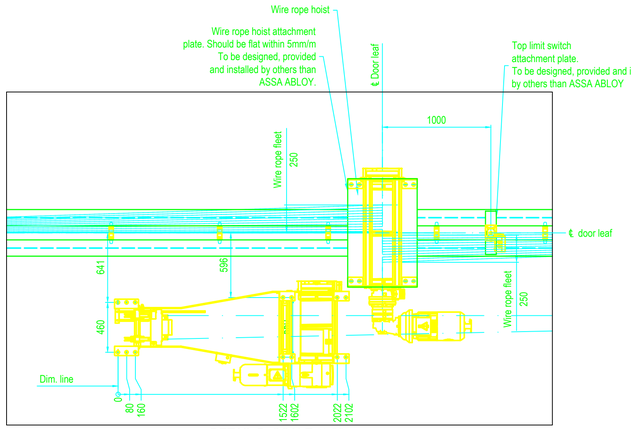


DETAIL B, SCALE (1:20)

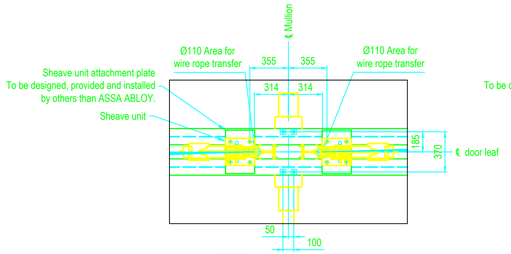


DETAIL C, SCALE (1:20)

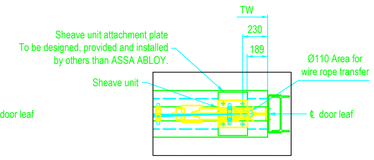

DETAIL D, SCALE (1:20)

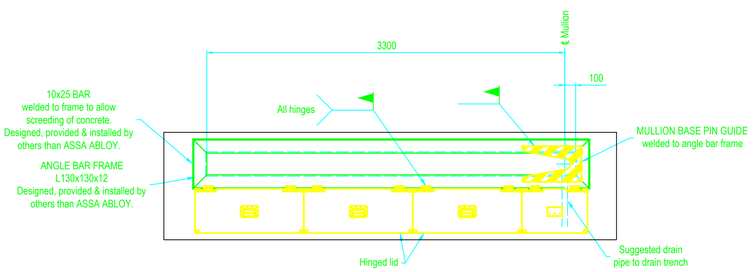

DETAIL E, SCALE (1:20)

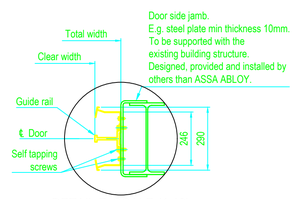

DETAIL F, SCALE (1:10)

DOOR IDENTITY NUMBER: 84801001

LOAD DIAGRAM & NOTES, ref. to drwng. no. 77450

INTERFACE, SECTIONS ref. to drwng. no. 77449

INTERFACE, ELEVATION ref. to drwng. no. 77447

DESIGNED EB	SIZE A1P	SCALE 1:100
CODE 84801	If not otherwise stated: Tolerances ISO 2768-m EN ISO 13920-B	
ITEM NO	Cutting class ISO 9013-442	
DATE 2022-08-30	Weld class ISO 5817-C	
ASSA ABLOY	Surface finish Smooth raw surface	

GMR Aero Technic Hangar2
India
Megadoor 91136x14700/14000
Interface, Plan views

DRAWING NO 77448

REVISION A

PLOT DATE