


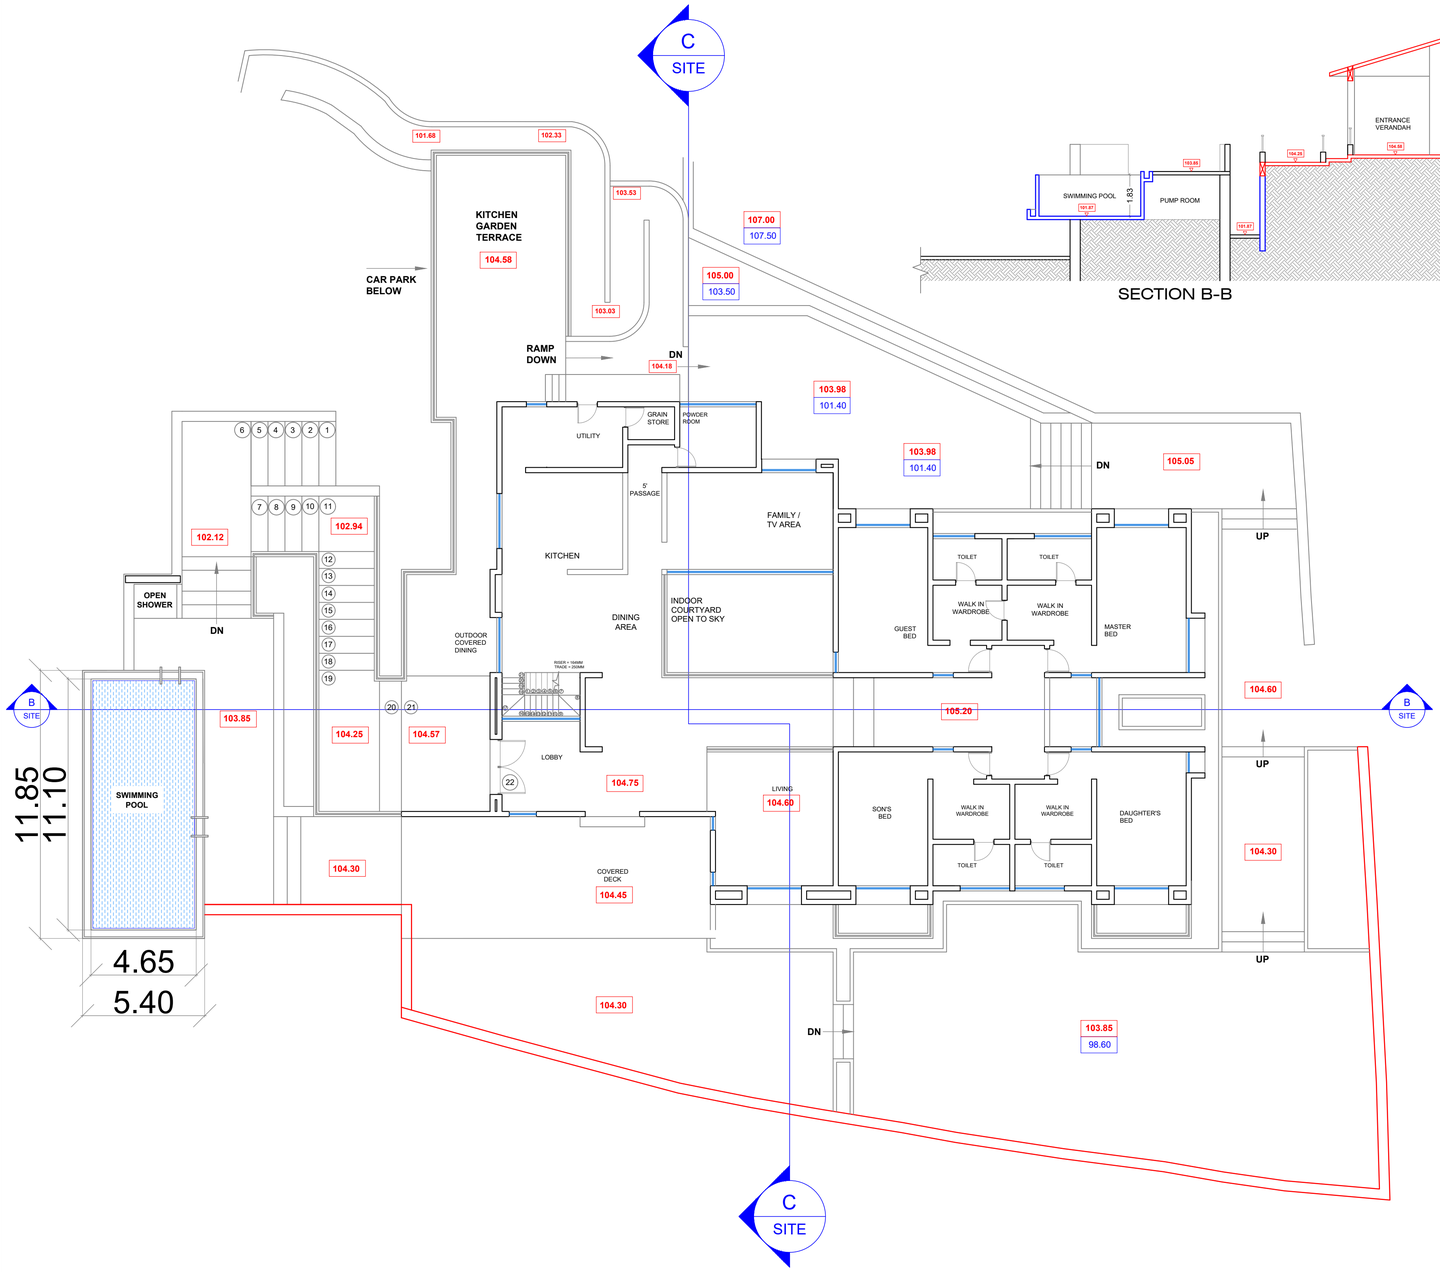


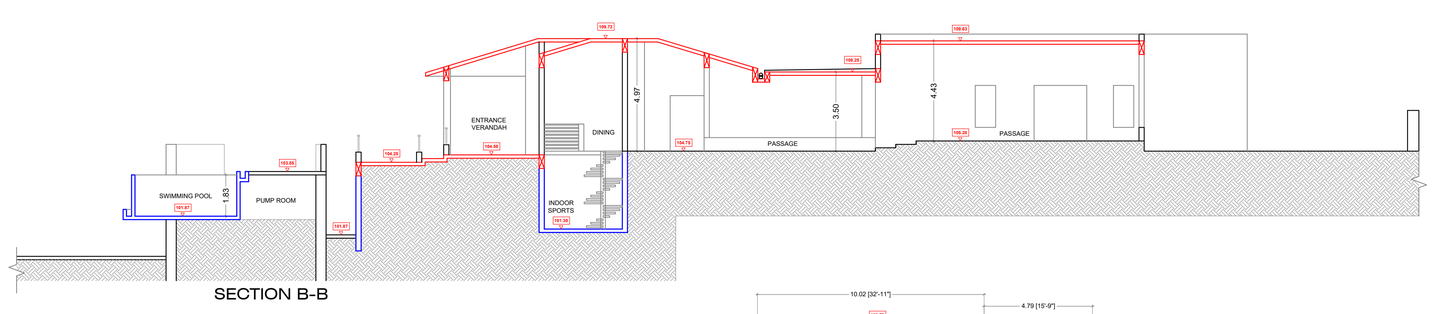

SECTION B-B

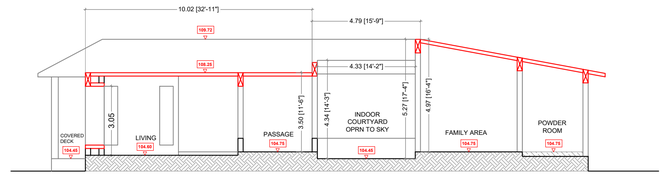

SECTION - CC

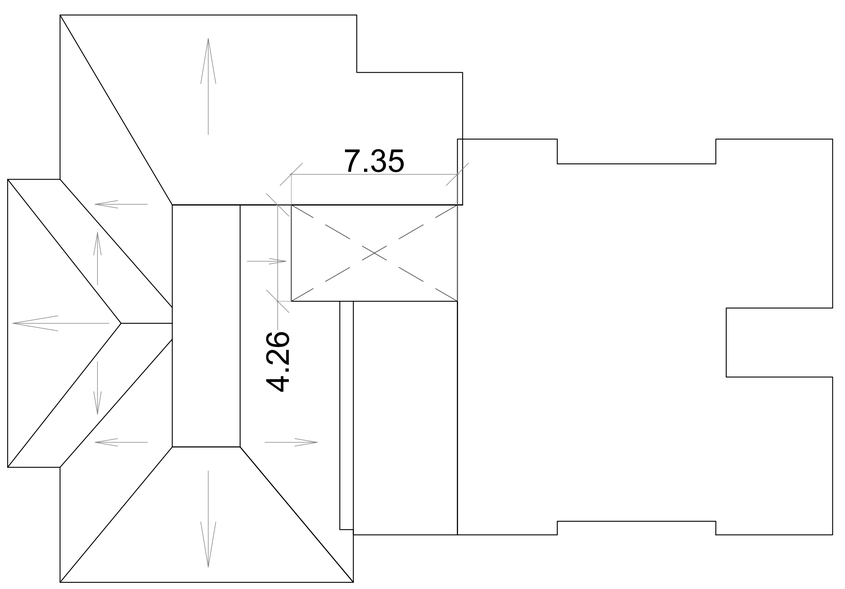

ROOF PLAN

ADVANCE COPY

REVISION	DATE	DESCRIPTION
R0	08.12.22	-

BRIEF NOTES :

- In Case Of Any Discrepancy, Contact Architect.
- All Designs Are Property Of AXIS PARADIGM SPACES (I) PVT. LTD.
- Drawing Should Not Be Scaled.
- All Measurements To Be Checked And Verified On Site
- Copywright And Property Of The Drawing Belongs To AXIS PARADIGM SPACES (I) PVT. LTD. And Shall Be Returned On Completion Of This Work.
- For R.c.c. Details, Refer R.c.c. Drawing.
- Hatch Portion In Toilets Indicate Sunk In floor
- Refer Separate Drawings For Toilet, Staircase, Window Door,Railing And Grill Details
- All Dimentions are in meters only

FN-DD-DF-02 R0 - 01.09.10

SCHEDULE OF OPENINGS

TYPE	SIZE	SILL LVL	LINTLE LVL

DRAWING TITLE : WORKING DRAWING

SUB TITLE : RETRACTABLE ROOF

PROJECT NAME : PROPOSED FARM HOUSE AT PLOT NO. 3, S. NO. 277/11, 407 / 408, 412 (P), 434/1 TO 9, 435 (1 TO 11) AT BHUGAON, TAL. MULSHI, PUNE.

axis
paradigm spaces (i) p. ltd.
architecture and interior design
3, Omkar, Plot No.-20, Madhavbaug, Co.Op.Hsg.Soc. Shivtirthnagar, Pune-38
tel.:+91020-25430586 telefax:+91020-25430587 e-mail:info@axisassociates.com

NORTH

SCALE	JOB NO.	DRAWN BY	APPROVED BY	DATE	COMPUTER FILE
N.S.T.	00-R-P00	MVH	ARP	01.02.2022	----