
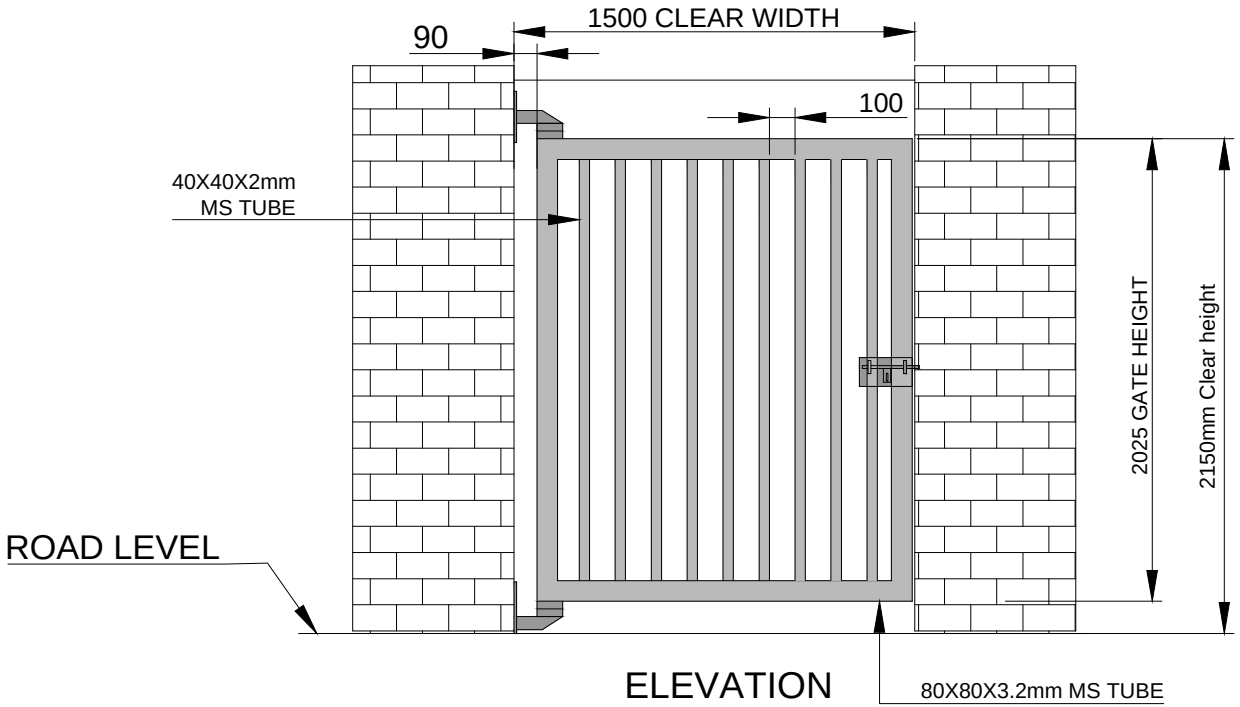


ELEVATION

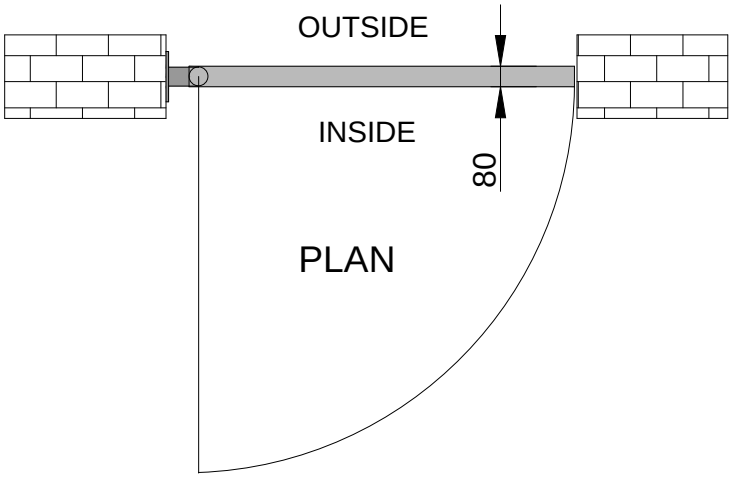

PLAN

TOLERANCE- ±10mm

SR NO	TUBE SPECIFICATION	
1	MS 80X80X3.2mm	OUTER FRAME
2	MS 40X40X2mm	INNER PATTERN

DIMENSION :

CLEAR WIDTH	CLEAR HEIGHT	QUANTITY
1500	2150	01 NO

MATERIAL :

THICKNESS :

NOTE-
1. ALL REQUIRED CIVIL WORK WILL BE IN CLIENTS SCOPE.
2. ONE COAT OF RED OXIDE & TWO COAT OF APPROVED RAL SHADE WILL BE GIVEN TO THE GATE.

NIHVA
NIHVA TECHNOLOGIES PVT. LTD.
NIHVA TECHNOLOGIES PVT. LTD. PUNE
Email:- info@nihva.com
Website:- www.nihva.com

TITLE:

WICKET GATE

CLIENT'S APPROVAL :

CLIENT -**PHARMADEEP TURNKEY CONSULTANT**

PROJECT -**PSE CHEMICALS AND PHARMA**

SITE LOCATION -M.P

DWG. NO. : NIHVA/18-19/0224

SCALE: NTS	WT:	SHEET:1 OF 1

DRAWN BY: SURAJ		29-12-2018
CHECK BY: PRADEEP		29-12-2018
APPROVED BY : R.D		29-12-2018

If any queries contact : design@nihva.com

NOTE: ALL DIMENSIONS ARE IN mm

THIS DRAWING & DESIGNING IS THE PROPERTY OF NIHVA TECHNOLOGIES. NOT TO BE SOLD OR COPIED TO ANY OTHER CONCERN.