




SIDE VIEW

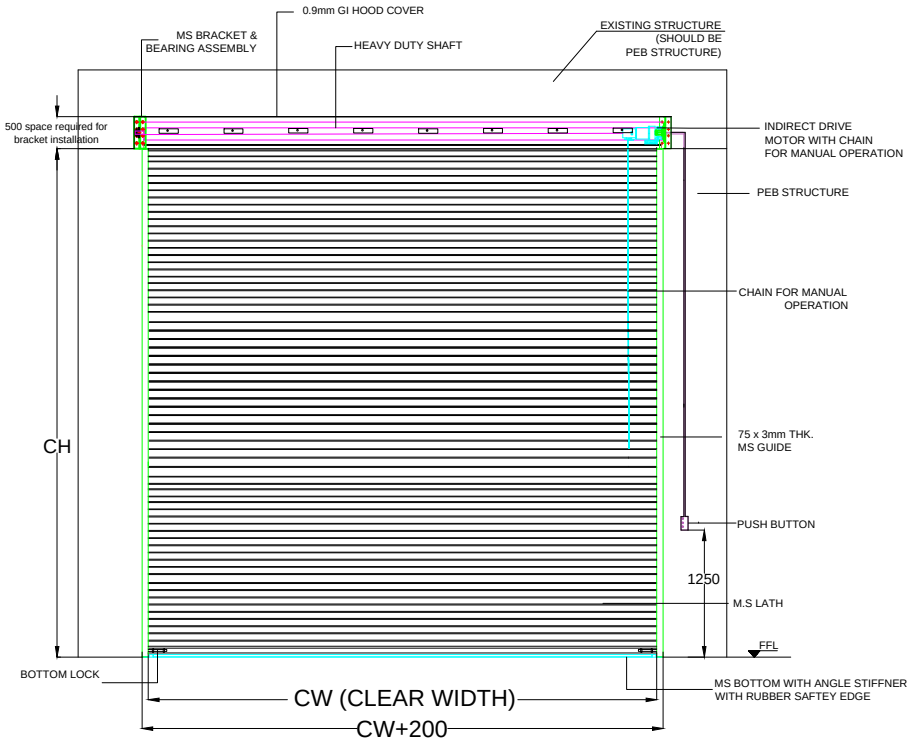


ELEVATION

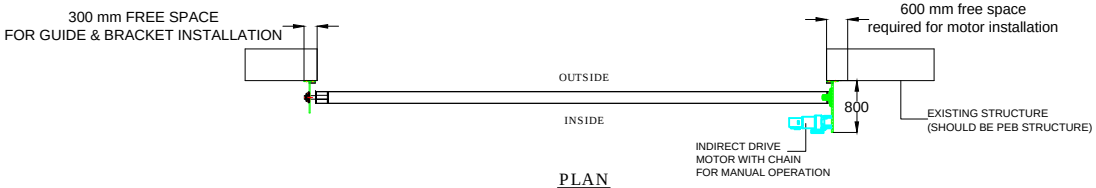

PLAN

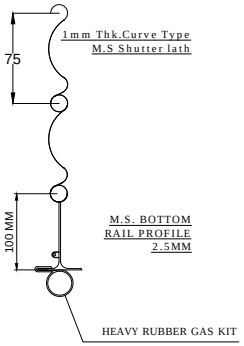

M.S. BOTTOM RAIL PROFILE 2.5MM

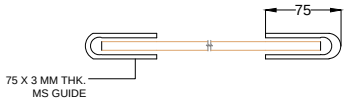

RAL COLOR & CODE

RAL 1003	
RAL 2004	
RAL 3000	
RAL 5002	
RAL 6005	
RAL 7035	
RAL 9005	
RAL 9010	

TOLERANCE - ±10mm

CLEAR WIDTH	CLEAR HEIGHT	QTY.
2400mm	3600mm	103 Nos.

NOTE-
1. ALL CIVIL WORK WILL BE CLIENT'S SCOPE.
2.STRUCTURE REQUIRED FOR SHUTTER IS IN CLIENT'S SCOPE.
3. RAL CODE - PLEASE TICK IN GIVEN BOX.

This drawing & design is the property of NIHVA TECHNOLOGIES. Not to be sold or copied to any other concern.

TITLE: MOTORISED ROLLING SHUTTER

	NAME	SIGN	DATE
DRAWN	A.K.		04.02.19
CHECK	P.A.		04.02.19
APPRD.	R.D.		04.02.19

If any queries contact : design@nihva.com

ALL DIMENSION ARE IN mm

NIHVA
NIHVA TECHNOLOGIES PVT. LTD.
Website:- www.nihva.com
NIHVA TECHNOLOGIES PVT. LTD. PUNE
Tel : 020 66304033
Email:- info@nihva.com

CLIENT - ESR
PROJECT -
SITE LOCATION - ULUBERIA
DWG. NO. : NIHVA/18-19/0266/R0
REV- R00
SCALE: NTS
WT:
SHEET: 01 OF 01