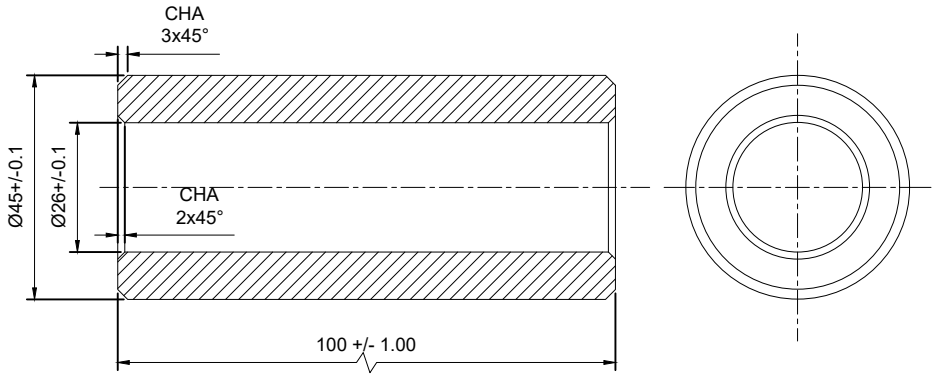


NOTE:~ MTL : MS

BUSH Ø45 X 100L = 80NOS

NOTE : ~ PLEASE MAINTAIN 7 MM GAP BETWEEN TWO LIP BUSHES.

This drawing & design is the property of NIHVA TECHNOLOGIES. Not to be sold or copied to any other concern.

TITLE				
LIP MOUNTING BUSH				NIHVA TECHNOLOGIES PVT. LTD.
	NAME	DATE	SIGN	
DRAWN				
CHECK				
APPRD.				SITE LOCATION - PUNE
If any queries contact : design1@nihva.com				DWG. NO. : NIHVA/24-25/00XX
ALL DIMENSION ARE IN mm				SCALE: NTS / WT: / REV- 0