
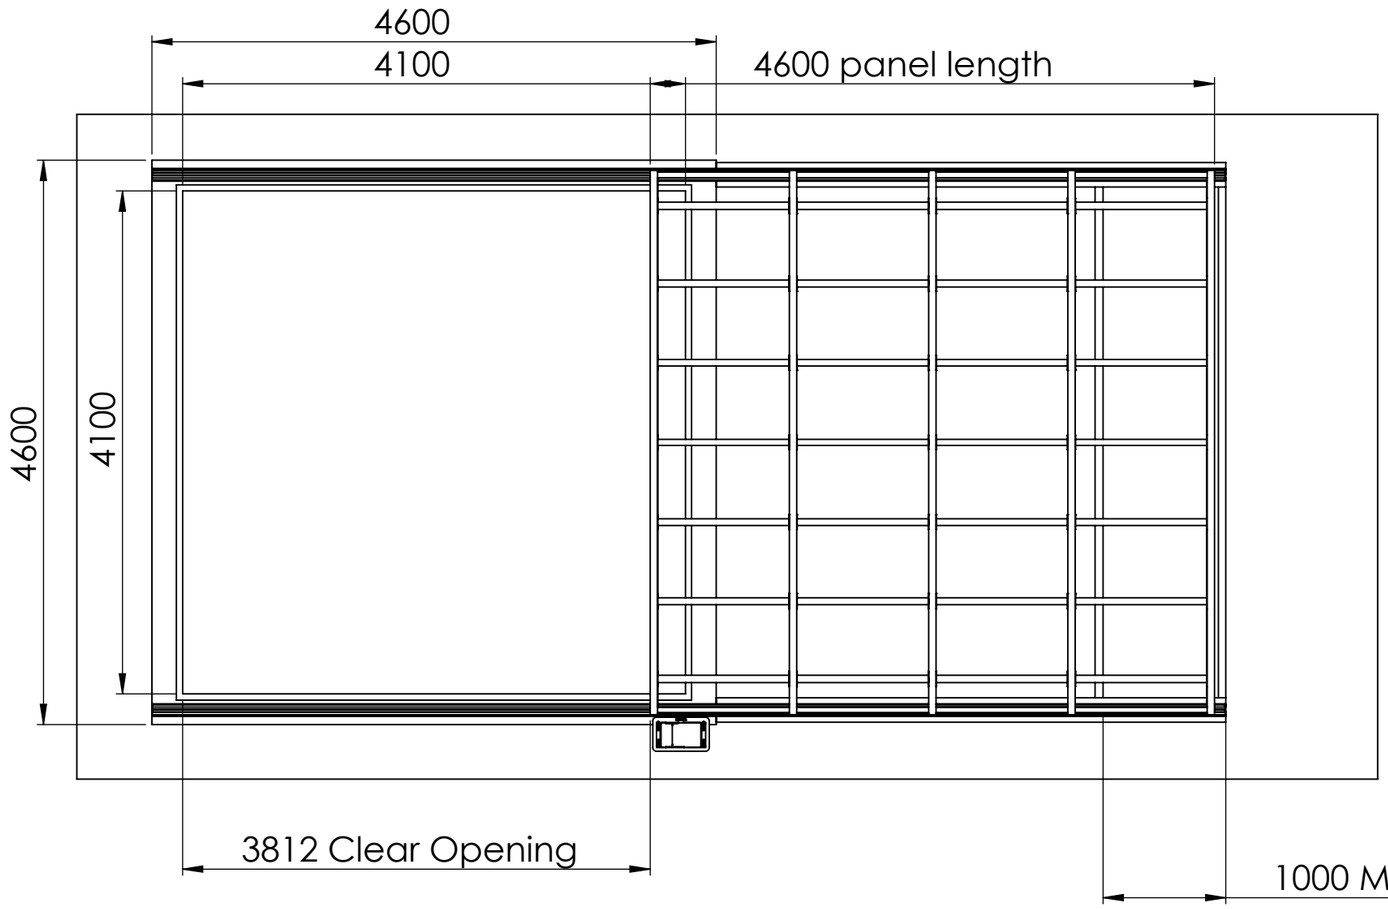
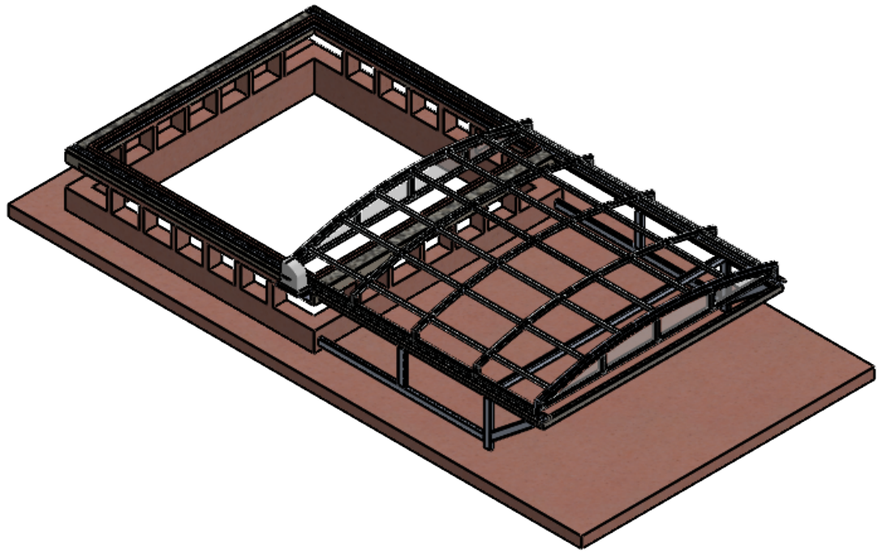
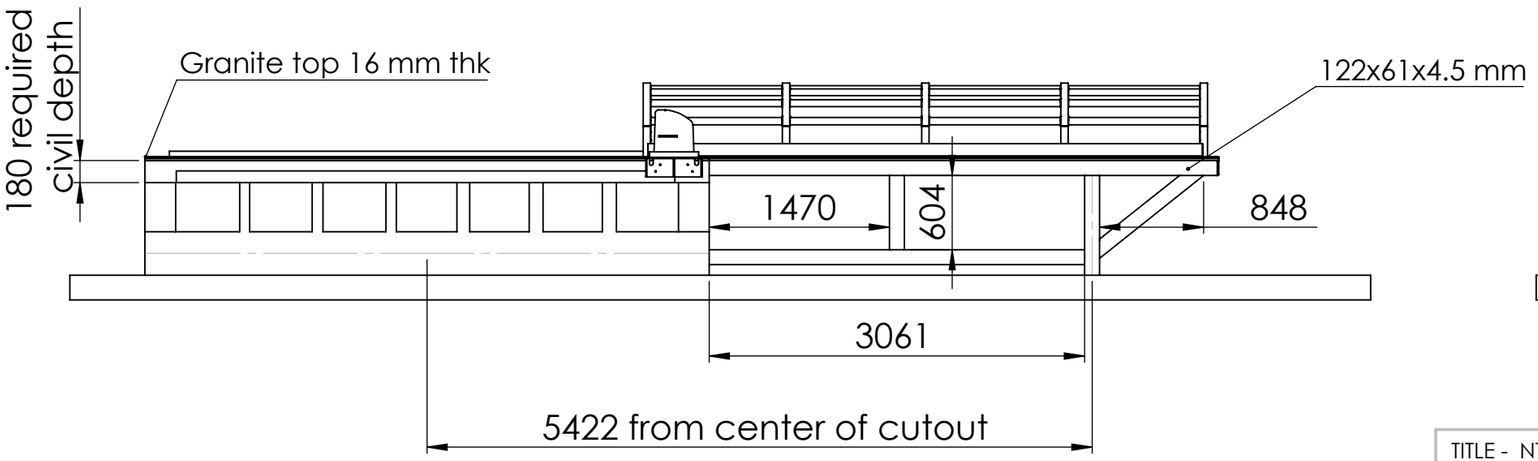


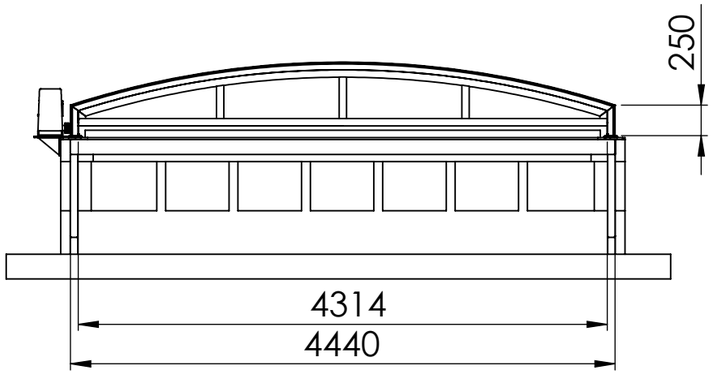


Note :
1) Top civil depth is shown as 100 mm in given autocad drawing and must be increased upto 180 mm for mounting of track
2) top surface shoud be of granite 16 mm thick
3) clear opening is 3812 mm
4) ms plate and granite top surface must be on same level for Track mounting

| TITLE - NTPL-183 UPDATED OPENING GA | | | | NIHVA TECHNOLOGIES PVT.LTD.PUNE<br>Website - www.nihva.com |
|---|---|---|---|---|
| | NAME | SIGNATURE | DATE | PROJECT NO - NTPL 183-HP |
| DRAWN | H.B. | | 08.08.2023 | PRODUCT - RETRACTABLE ROOF |
| CHK'D | P.M. | | 08.08.2023 | SITE LOCATION - Ahmedabad |
| APPV'D | V.T. | | 08.08.2023 | |
| if any queries contact - supportautomation@nihva.com | | | | REVISION - |
| ALL DIMENSION ARE IN mm | | A3 | | SCALE - SHEET 1 OF 1 |