


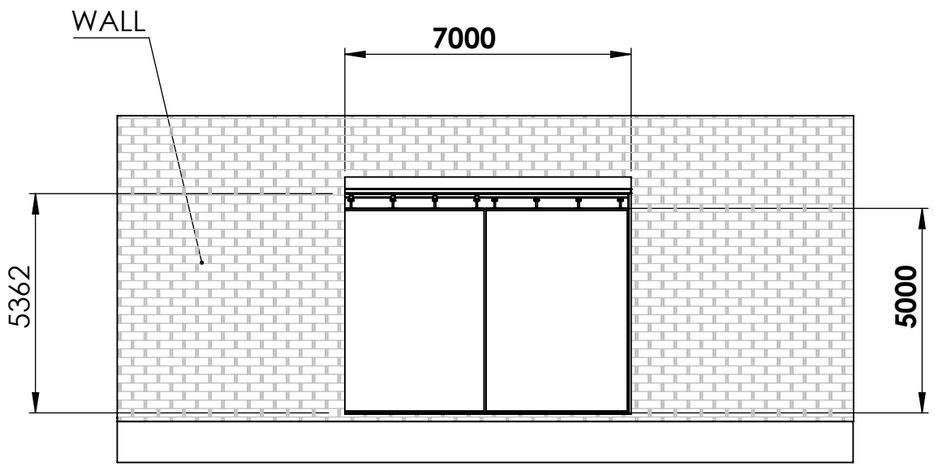


CLOSE POSITION

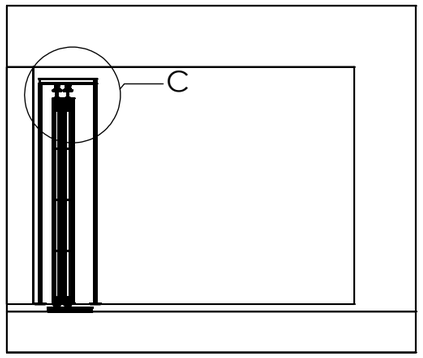


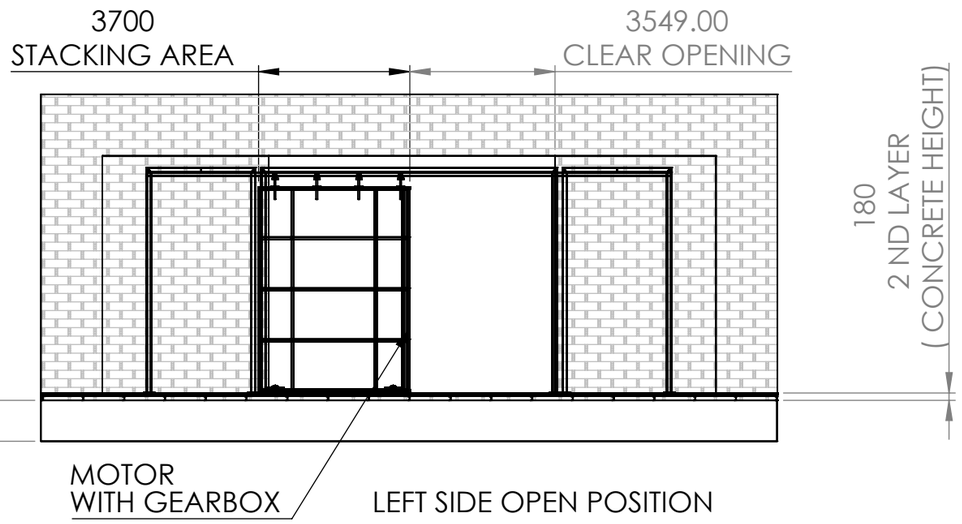

LEFT SIDE OPEN POSITION

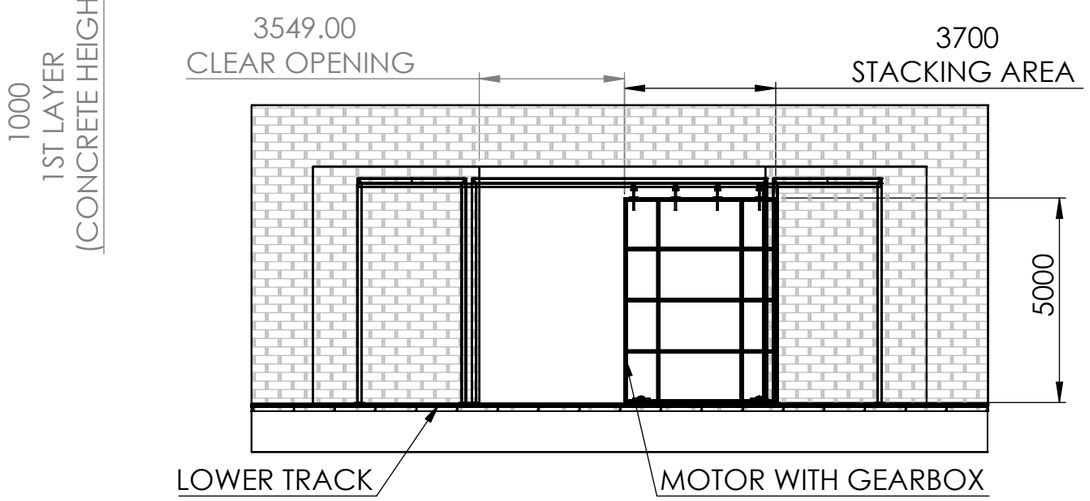

RIGHT SIDE OPEN POSITION

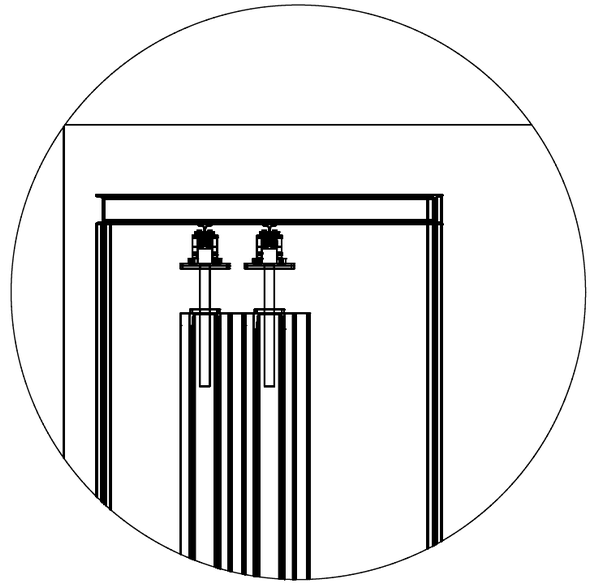

DETAIL C
SCALE 1 : 25

TITLE :	**HANGING SLIDING DOOR 7000 WIDTH X 5000 HEIGHT MM**		
	NAME	**SIGN**	**DATE**
DRAWN	BHARATI SABALE		10-01-2025
CHK'D	SURAJ WARALE		10-01-2025
APPV'D	VIJAY T.		10-01-2025
	DIMENSIONS ARE IN MILLIMETERS		

NIHVA Technologies Pvt. Ltd.

NIHVA TECHNOLOGIES PVT LTD

CLIENT NAME : ISRO

PRODUCT NAME : HANGING SLIDING DOOR

SITE LOCATION : ALUVA, KERALA

DWG NO. GA — A3

REVISION : 0

SCALE: — SHEET 1 OF 1