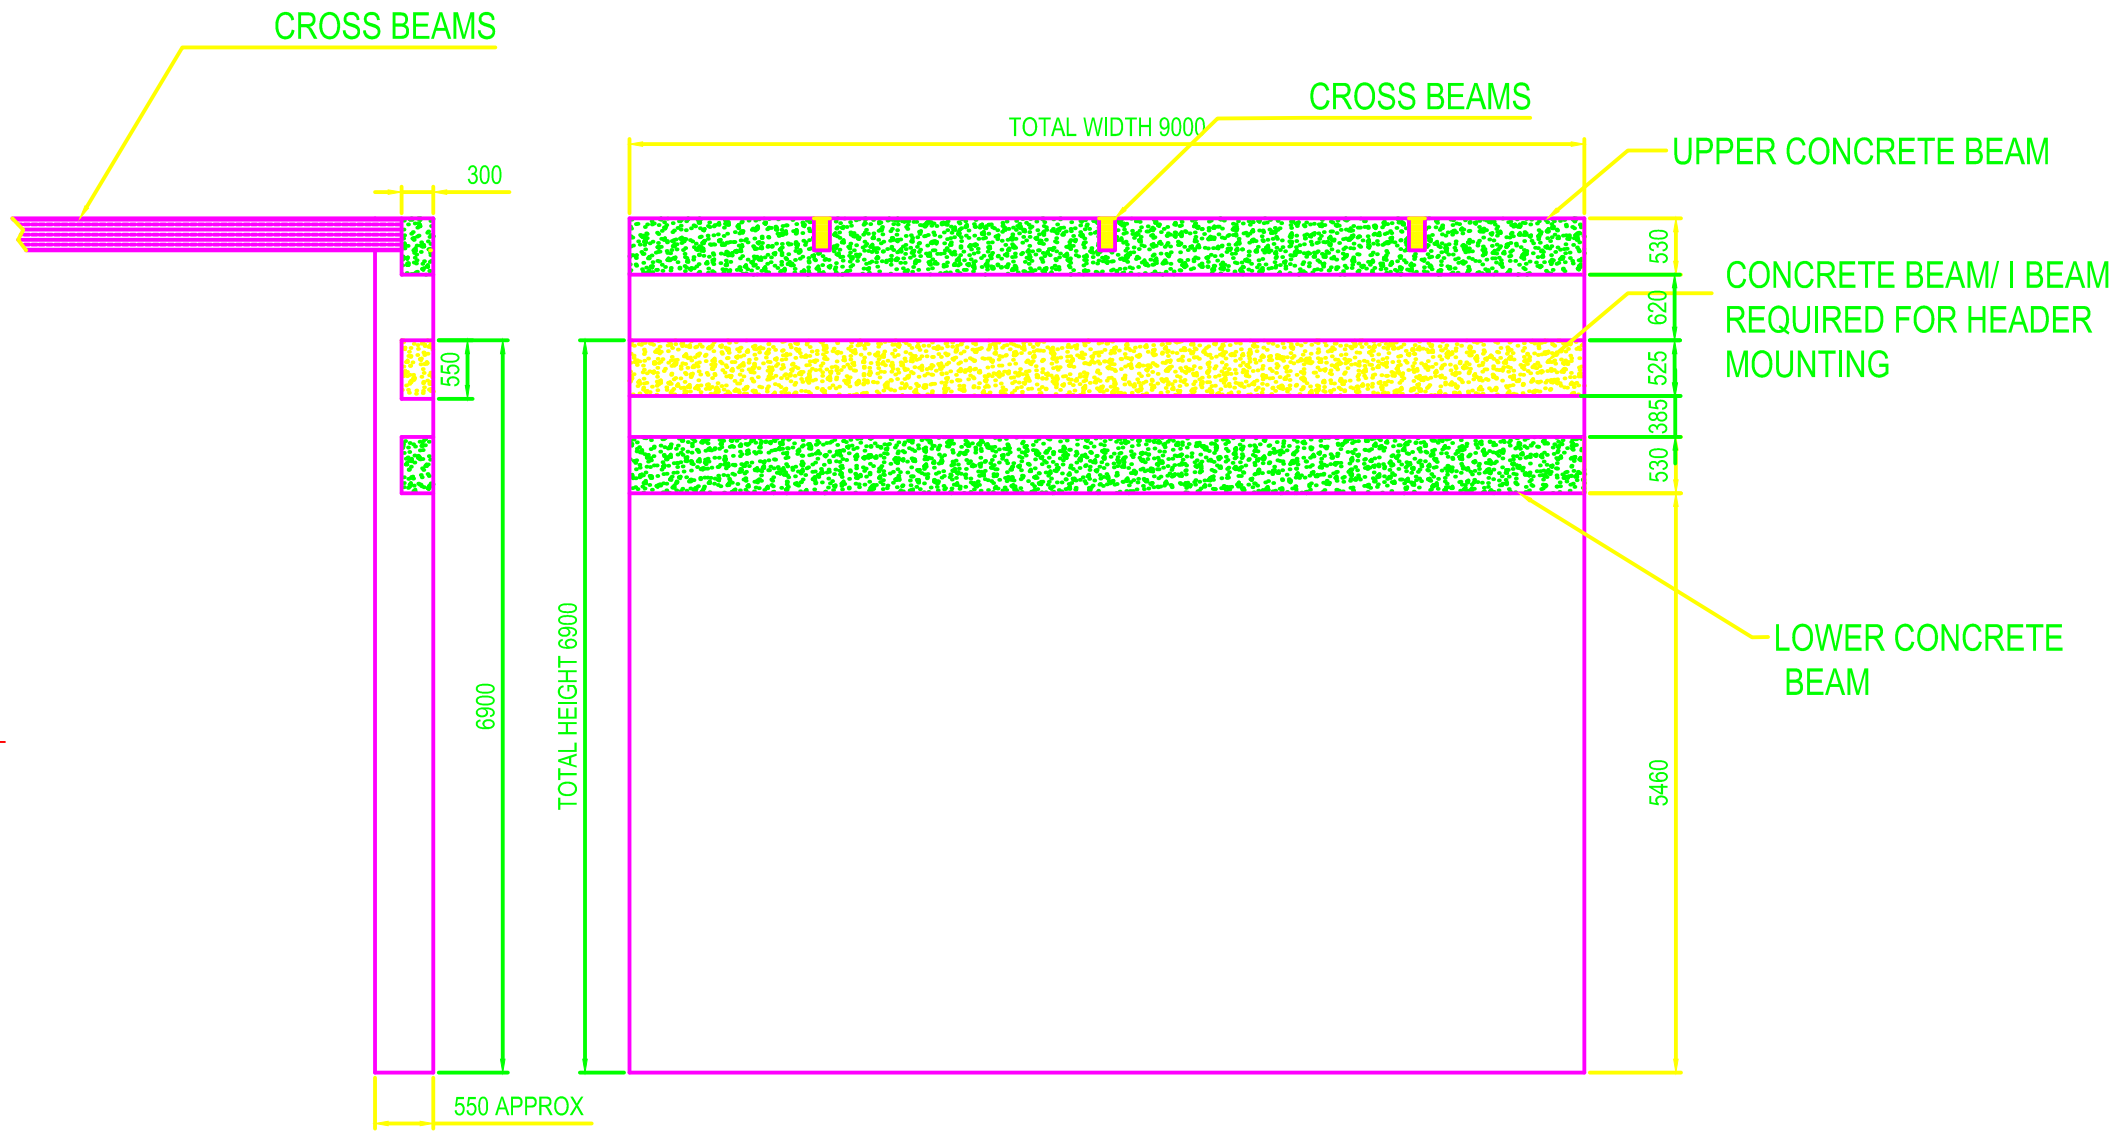


BEAM STRUCTURE AT SITE TERMINAL 4

OLD BUILDING : ARFF 4
CLEAR OPENING : 5400 X 9000
QTY : 2 NOS

This drawing & design is the property of NIHVA TFC – NOIDCIFS. Not to be sold or copied to any other person

TITLE				
MEGA DOOR 5400 X 9000 (ARFF4)				NIHVA TECHNOLOGIES PVT. LTD. PUNE Tel : 020 66304033 Email:- info@nihva.com Website:- www.nihva.com
	NAME	SIGN	DATE	
DRAWN	G.P.		21.08.2021	CLIENT -DIAL- L&T
CHECK	A.K.		21.08.2021	LOCATION - DELHI
APPRD.	V.T.		21.08.2021	PRODUCT - MEGA DOOR - 5400 X 9000
If any queries contact : design@nihva.com				NIHVA\20-21\0217 / REV- 0
ALL DIMENSION ARE IN mm				SCALE: NTS / SHEET: 02 OF 02

This document is the property of ASSA ABLOY Entrance Systems AB and shall not be reproduced or disclosed to any third party or used for any other unauthorized purpose.