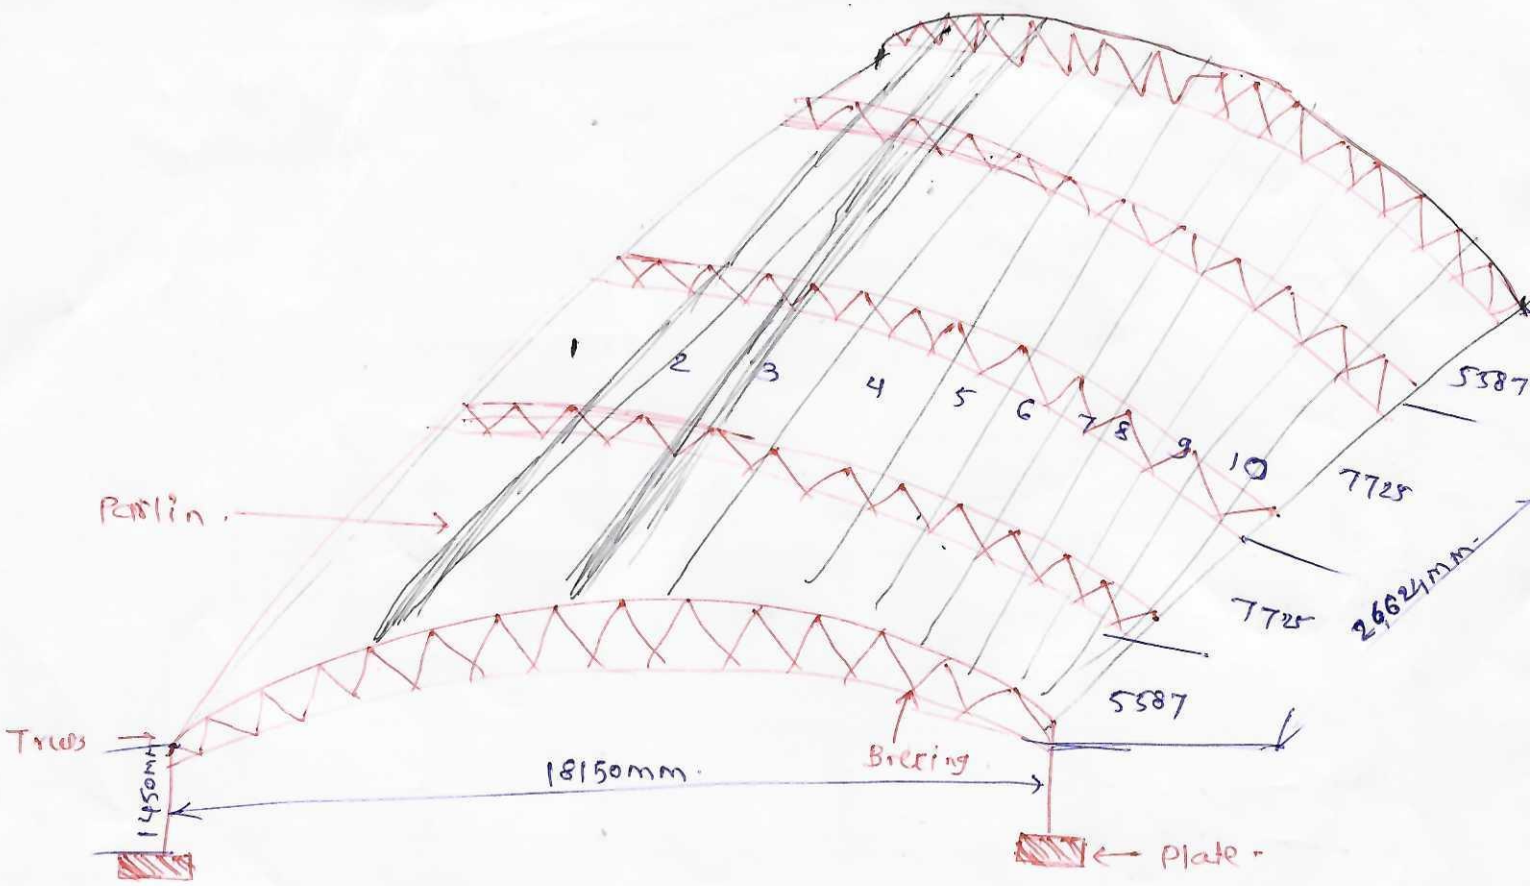


⇒ Parlin - RHS 145X82X3.2 ~~122X61X4.5~~mm = ~~11.88~~ 17.74 kg/mtr.

~~11.88~~ = ~~11.88~~ Total Mtr = 26.6 X 12 Nos.
= 319.2 mtr.

⇒ Trws - RHS 122X61X4.5mm = 12.94 11.88 kg/mtr.

Total mtr = (20X2) X 5 Nos
= ~~10X2~~ 200 mtr.

plate - 500X250X8 X20 Nos.

Verticle 122X61X4.5 = 11.88 kg/mtr. = 1.450 X 20 Nos = 29 mtr.

⇒ Bracing - 65X65X6 = 12.26 kg/mtr = (Tie) 200 mtr.
40X40X4 = 4.2 kg/mtr. = 32X5 part X 2mtr = 320 mtr.
122X61X4.5 = 11.8 kg/mtr = 10X5X2mtr = 100 mtr.

⇒ Bracing Joining 90X90X8 'L'Angle = 400mm each Bracing X ~~44~~ X5
= 88 mtr.