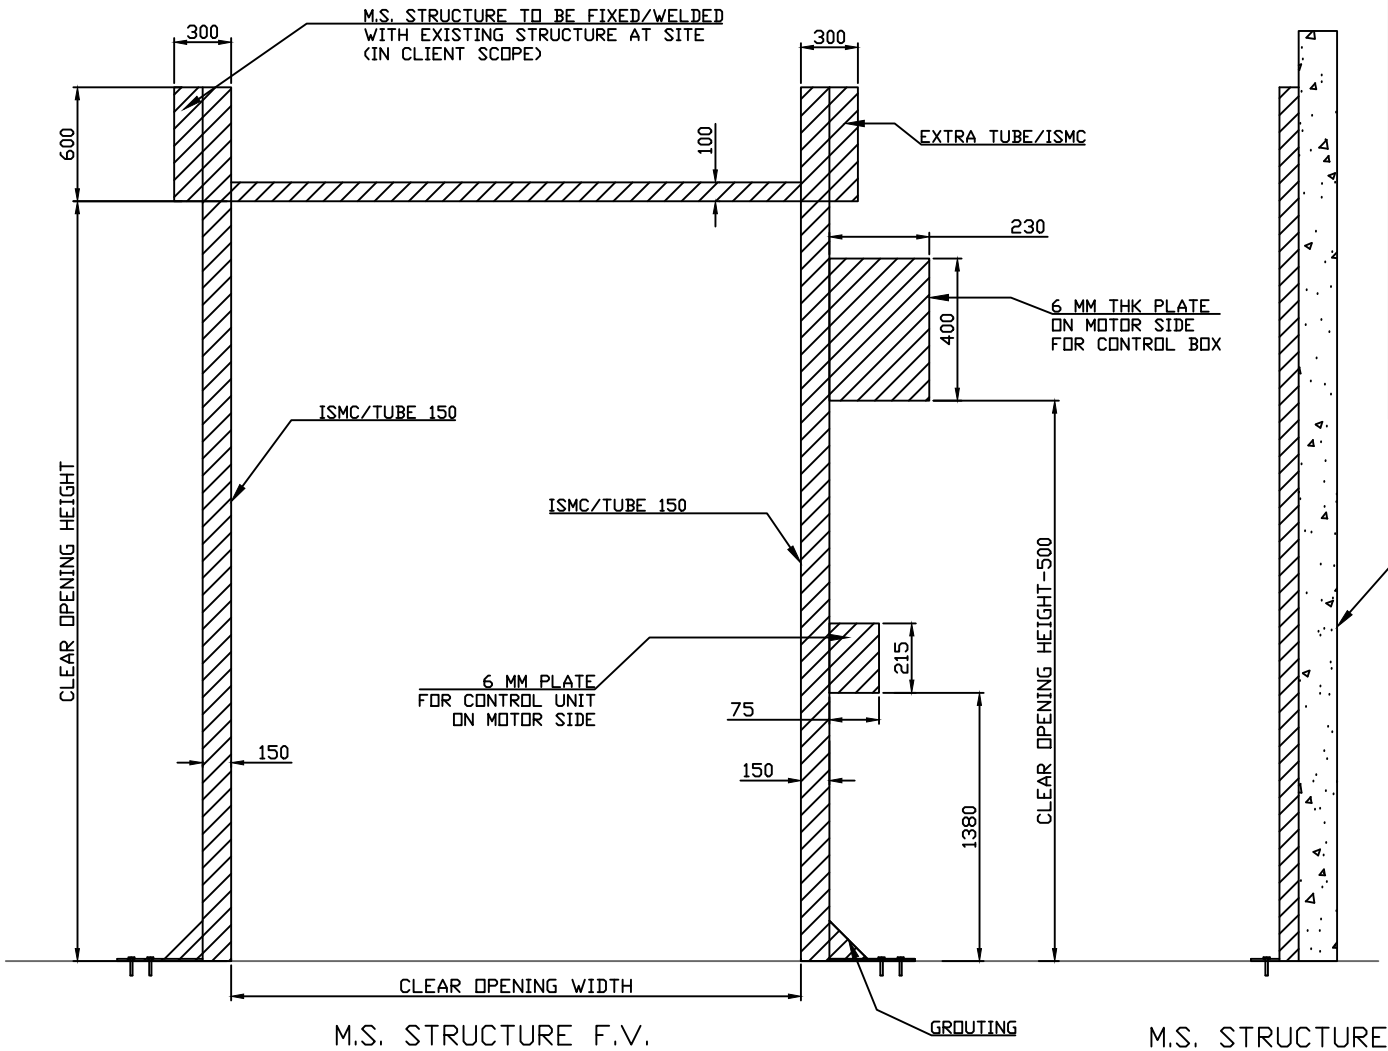


NOTES-

1. REQUIRED M.S. STRUCTURE , FITTING & ALL CIVIL WORK IS IN CLIENT SCOPE .
2. HIGH SPEED DOOR WILL BE INSTALLED AFTER READINESS OF STRUCTURE AS PER DRAWING .
3. M.S. STRUCTURE SHOULD BE RIGID & NEED TO BE FIXED/WELDED WITH EXISTING STRUCTURE AT SITE .
4. KINDLY WELD PLATES FOR CONTROL BOX & PENDANT TO THE MOTOR SIDE AS PER DRAWING.

SR NO	CLEAR OPENING WIDTH	CLEAR OPENING HEIGHT	QTY	LOCATION	MOTOR SIDE
1	1950	3900	1	PROCESS AREA ENTRY	RH
2	2500	4000	1	KINDER JOY TUNNEL	LH
3	3000	3900	1	KSBC PARKING	LH
4	1950	2500	1	ROCHER PACKING	RH
5	2850	3700	1	KINDER JOY PACKING	RH
6	2200	3500	1	SYRUP TUNNEL	RH
7	2400	2600	1	KINDER JOY ENTRY TUNNEL	LH

This drawing & design is the property of NIHVA TECHNOLOGIES. Not to be sold or copied to any other concern.

TITLE - RR300 PLUS ALU HSD M.S. STRUCTURE

NIHVA TECHNOLOGIES PVT. LTD. PUNE
Tel : 020 66304033
Email:- info@nihva.com
Website:- www.nihva.com

	NAME	SIGN	DATE
DRAWN	S.M.S.		8.2.2021
CHECK	A.G.		8.2.2021
APPROVED			

CLIENT - FERRERO INDIA PVT. LTD

PROJECT -

LOCATION - BARAMATI

If any queries contact:sales@nihva.com

DWG. NO. -NIHVA/20-21/0155 REV- 0

ALL DIMENSION ARE IN mm

SCALE: NTS WT: SHEET: