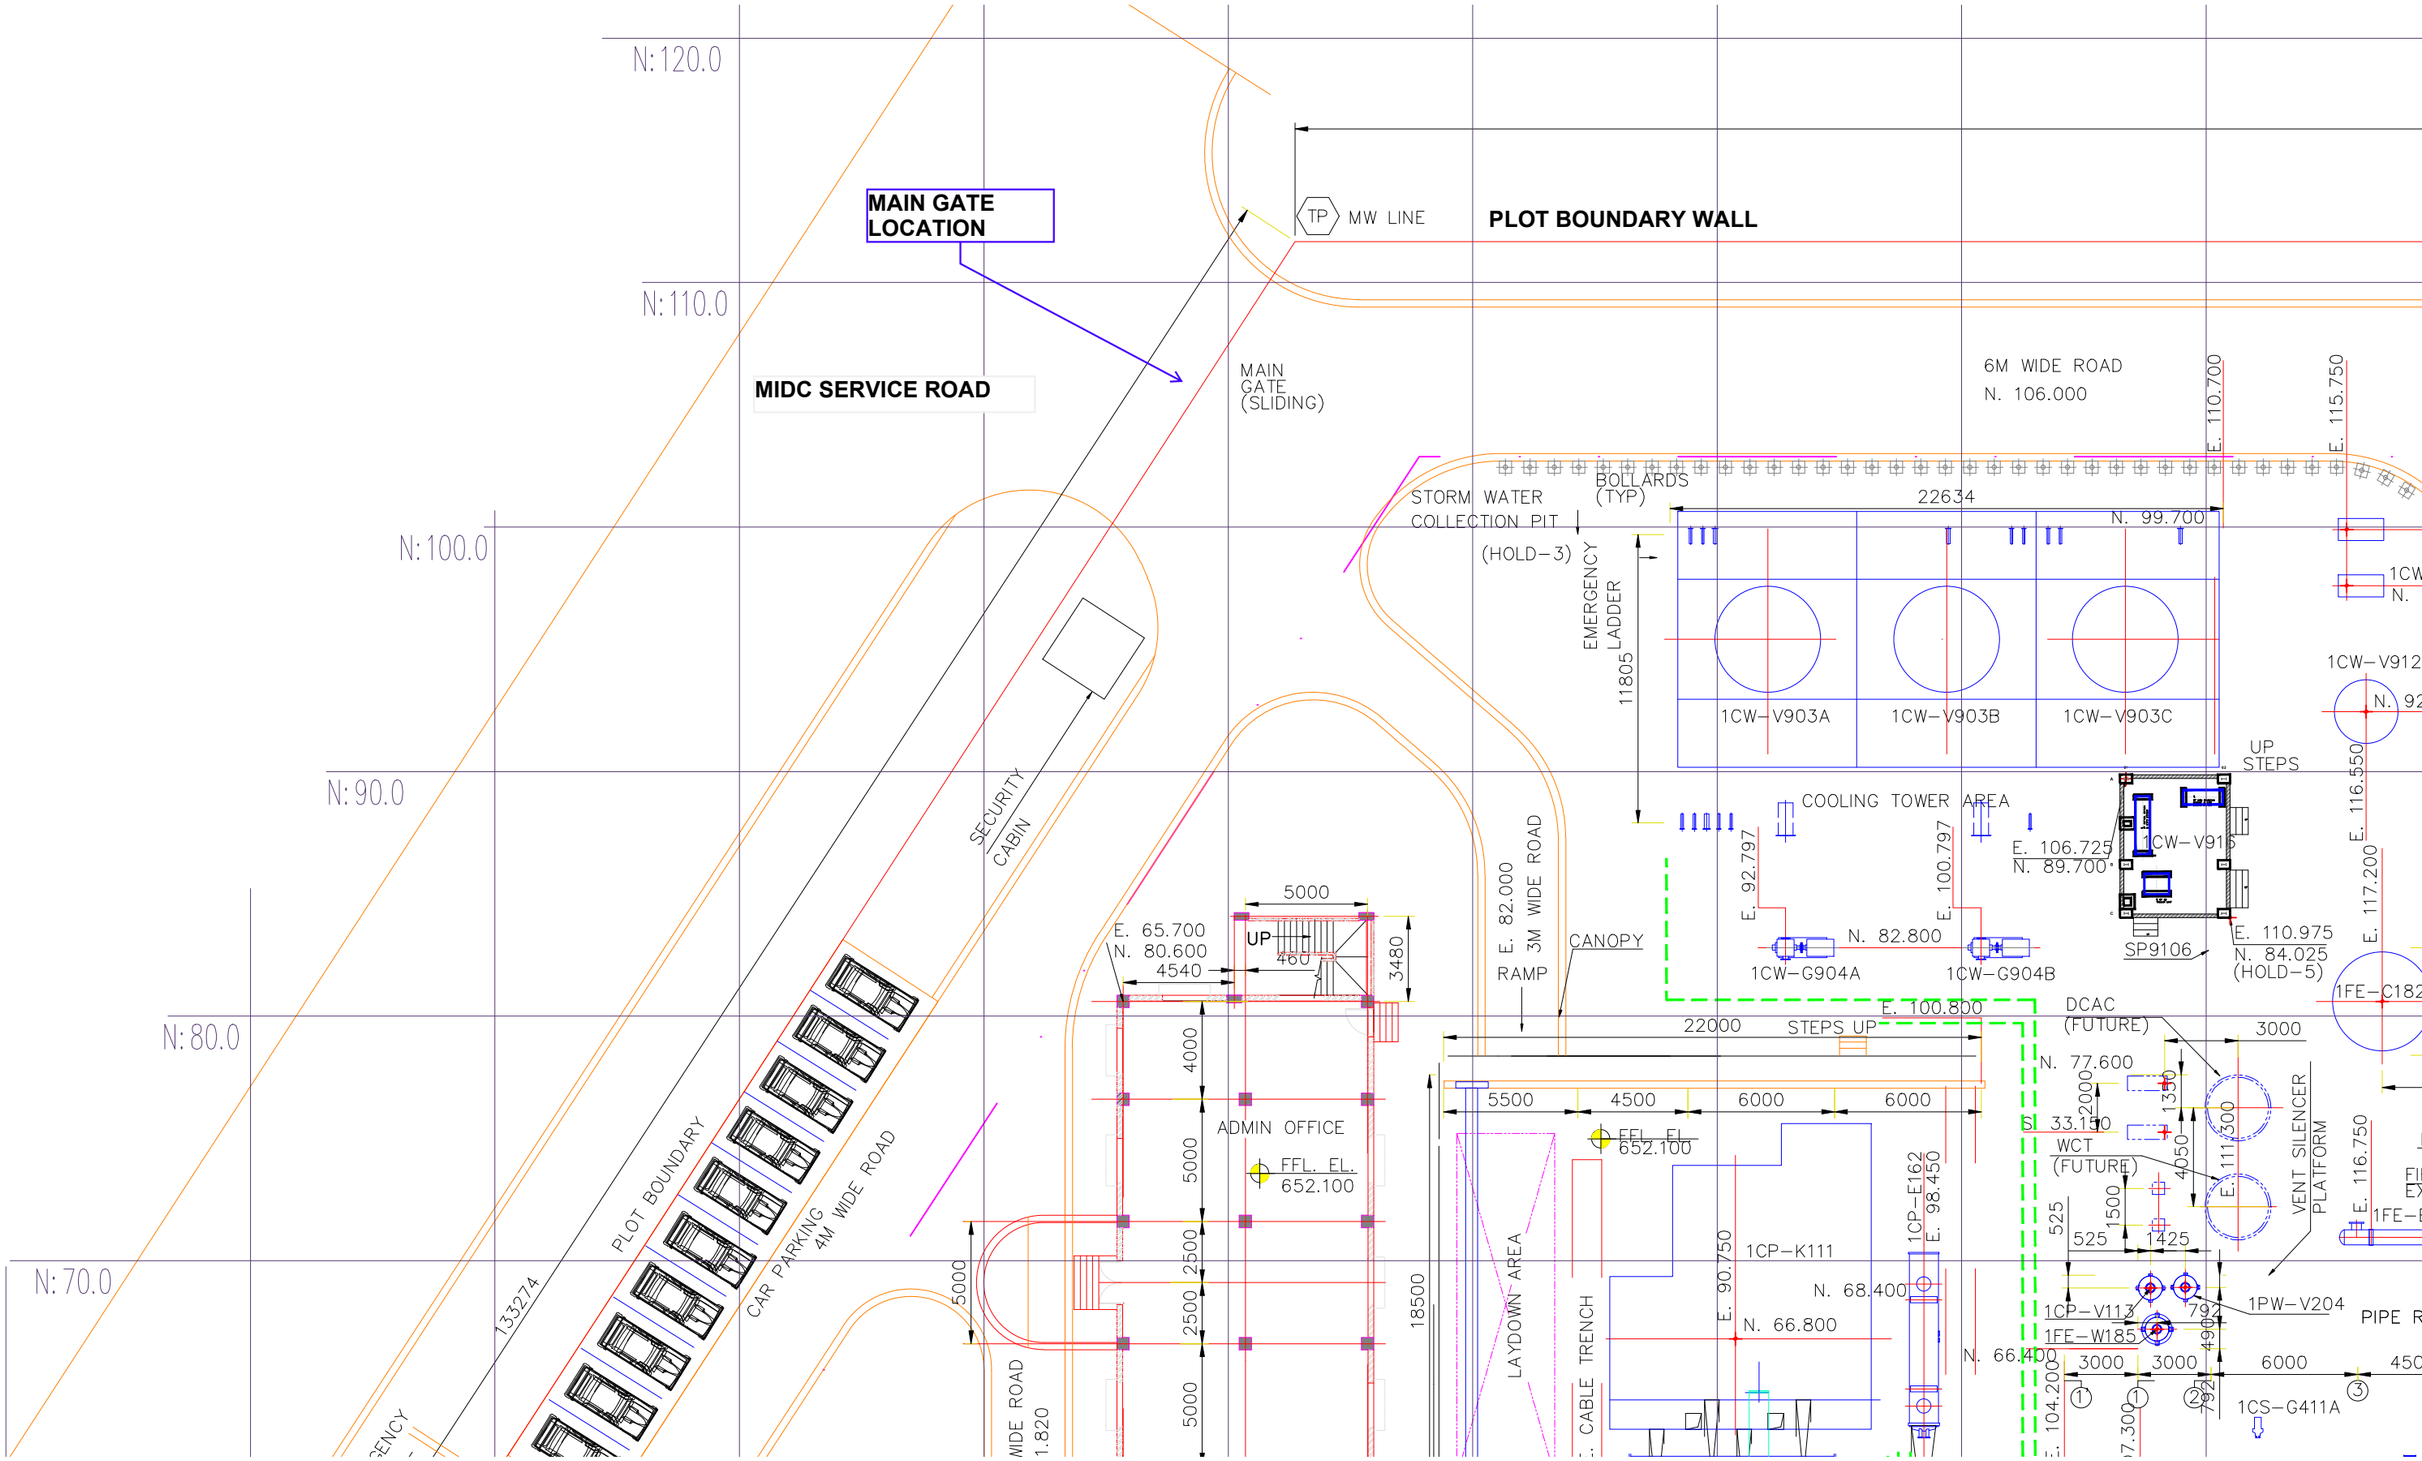

N: 120.0
N: 110.0
N: 100.0
N: 90.0
N: 80.0
N: 70.0
MAIN GATE LOCATION
MIDC SERVICE ROAD
TP
MW LINE
PLOT BOUNDARY WALL
MAIN GATE (SLIDING)
6M WIDE ROAD
N. 106.000
E. 110.700
E. 115.750
BOLLARDS (TYP)
STORM WATER COLLECTION PIT
(HOLD-3)
22634
N. 99.700
EMERGENCY LADDER
11805
1CW-V903A
1CW-V903B
1CW-V903C
UP STEPS
COOLING TOWER AREA
E. 92.797
E. 100.797
E. 106.725
N. 89.700
1CW-V915
E. 116.550
E. 117.200
N. 82.800
1CW-G904A
1CW-G904B
SP9106
E. 110.975
N. 84.025
(HOLD-5)
1FE-C182
E. 82.000
3M WIDE ROAD
RAMP
CANOPY
E. 100.800
22000
STEPS UP
DCAC (FUTURE)
3000
N. 77.600
E. 111.500
E. 116.750
SI 33.150
WCT (FUTURE)
VENT SILENCER PLATFORM
1FE-E
5500
4500
6000
6000
FFL EL 652.100
1CP-K111
1CP-E162
E. 98.450
E. 90.750
N. 68.400
N. 66.800
N. 66.400
1CP-V113
1PW-V204
1FE-W185
PIPE R
3000
3000
6000
1CS-G411A
E. 104.200
E. 107.300
5000
E. 65.700
N. 80.600
4540
UP
460
3480
4000
5000
2500
2500
5000
ADMIN OFFICE
FFL. EL. 652.100
18500
5000
LAYDOWN AREA
CABLE TRENCH
SECURITY CABIN
PLOT BOUNDARY
133274
CAR PARKING
4M WIDE ROAD
1.820