


Outer structure in single frame

TOP VIEW

SECTION X-X

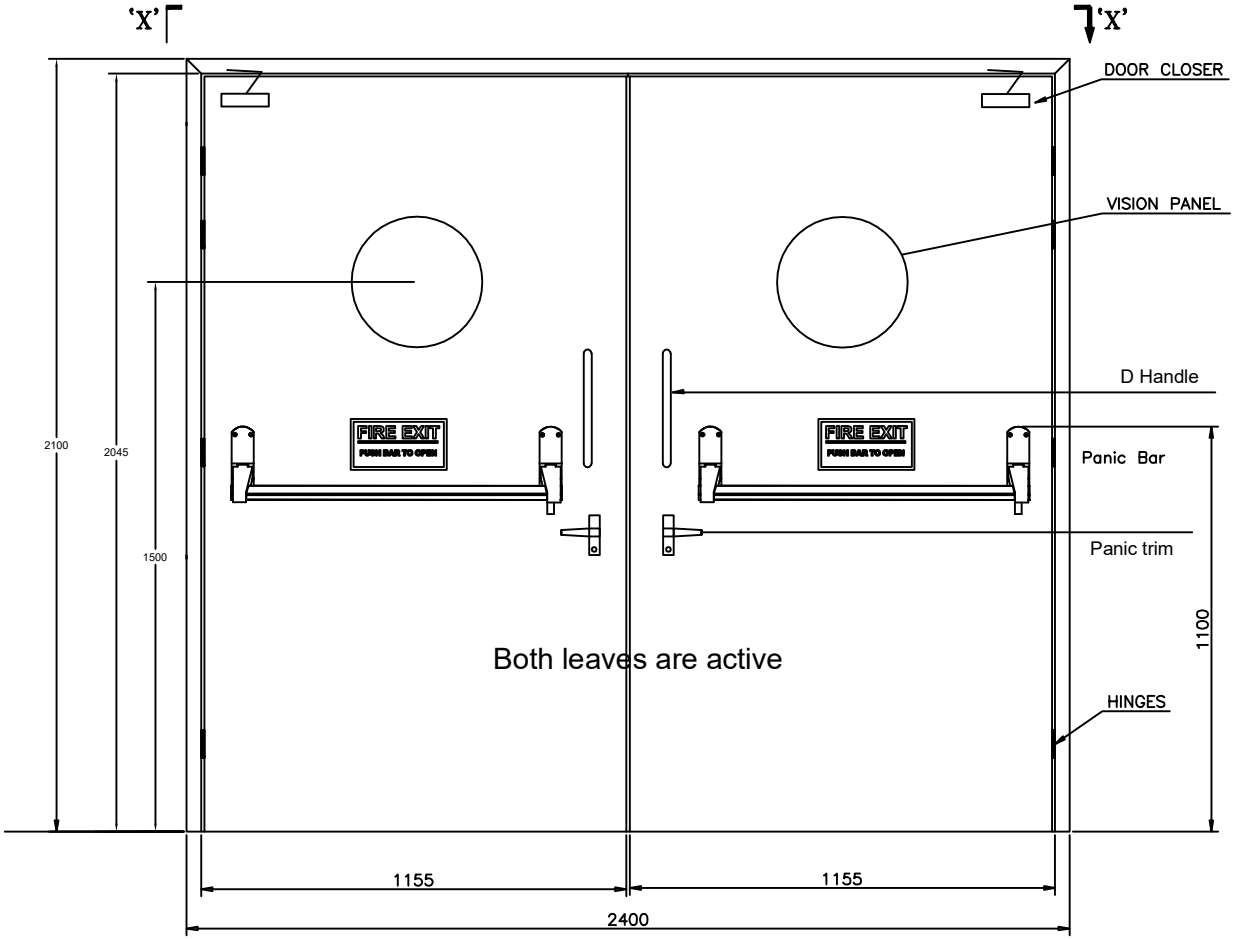

Both leaves are active

ELEVATION VIEW

DOUBLE LEAF FIRE DOOR

NOTE :-

1. This drawing is only for reference.
2. Dimensions may change as per site condition & product.
3. Accessories Geze make.

Sr.	Technical Specification
1	S.S.Ball Bearing Hinges 102X76X3mm
2	Panic Exit Device
3	External Trim Bar (Panic Latch)
4	S.S. " D " Type Handle
5	Heavy Duty Door Closer
6	Vision Panel With Fire Rated Class Of Size - Ø300 mm (6mm Thick Float Glass)

Revision	Date	Details	Revised By
R4	16/01/2024	Vision window Dia. 256 changed to Dia.300	Jayesh
R3	04/01/2024	Vision window changed Square to Round Dia 256	Jayesh
R2	02/01/2024	Accessories Added	Jayesh
R1	30/11/2023	Window size 200 x 300 changed to 300 x 200	Jayesh

This drawing & design is the property of NIHVA TECHNOLOGIES. Not to be sold or copied to any other concern.

TITLE - DOUBLE LEAF FIRE DOOR

NIHVA TECHNOLOGIES PVT. LTD. PUNE
Tel : 020 66304033
Email:- info@nihva.com
Website:- www.nihva.com

	NAME	DATE	SIGN
DRAWN	S.J	03/11/2023	
CHECK	A.K	03/11/2023	
APPRD.	V.T	03/11/2023	

If any queries contact : design1@nihva.com

All dimesions are In mm

CLIENT - Smith Stuctures India Pvt. Ltd.

PRODUCT - FIRE DOOR

DWG NO - NIHVA/23-24/CLT/063 QTY:-01 NOS

FORMAT NO - NIHVA-DD-F-03 REV- 0

SCALE:NTS SCALE:- 1:1 SHEET:01 OF 01