


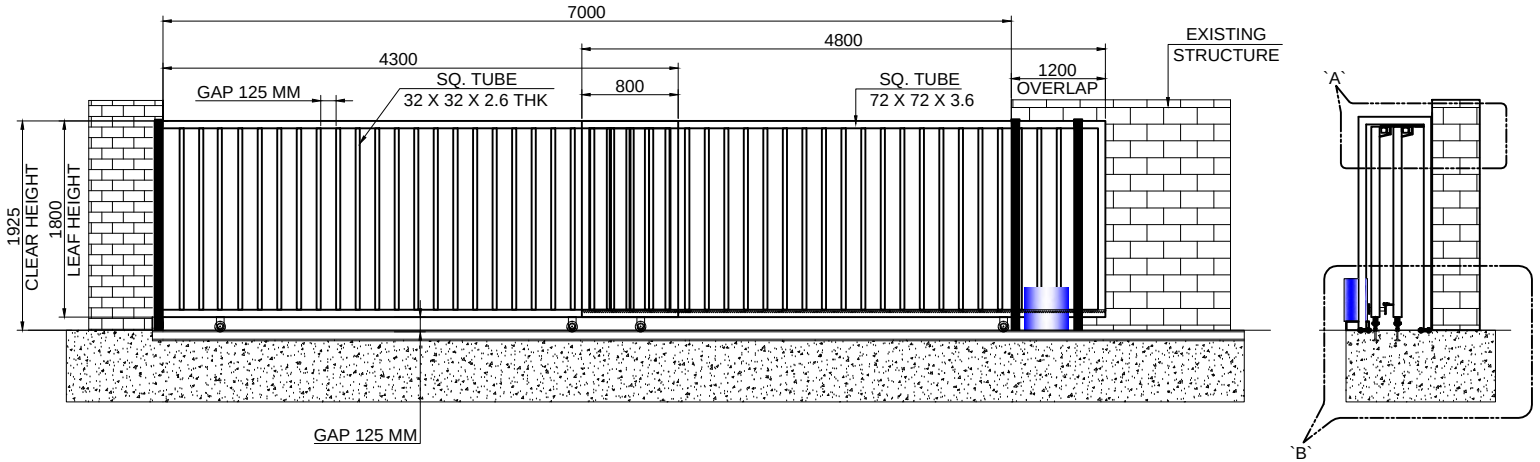


OPENING DIRECTION →

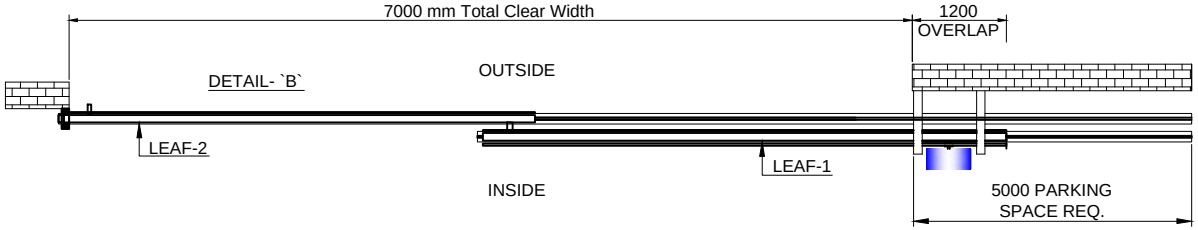

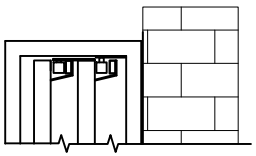

DETAIL -`A`

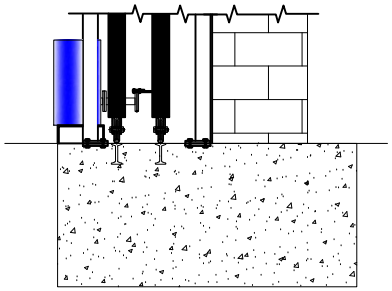

DETAIL- `B`

NOTE-
1. ALL REQUIRED CIVIL WORK WILL BE IN CLIENTS SCOPE.
2.GATE LEAF WILL BE IN TWO PARTS FOR TRANSPORTATION & WILL BE WELD TOGETHER ON SITE IF NECESSARY.
3.FLASHING LIGHT WITH ALARM.
4.ELE. SAFETY SENSOR (PHOTOCELL).

CLEAR WIDTH	CLEAR HEIGHT	QUANTITY
7000	1800	01 NO

TOLERANCE - ±10mm

This drawing & design is the property of NIHVA TECHNOLOGIES. Not to be sold or copied to any other concern.

TITLE
2 LEAF TELESCOPIC SLIDING GATE

	NAME	SIGN	DATE
DRAWN	P.A		22.11.2019
CHECK	G.J		22.11.2019
APPRD.			

If any queries contact : design@nihva.com

ALL DIMENSION ARE IN mm

NIHVA
NIHVA TECHNOLOGIES PVT. LTD.

NIHVA TECHNOLOGIES PVT. LTD. PUNE
Tel : 020 66304033
Email:- info@nihva.com
Website:- www.nihva.com

CLIENT - DEVI GROUP
PROJECT - CONTINENTAL
SITE LOCATION - PUNE
DWG. NO. : NIHVA/19-20/0158 | REV- R00
SCALE: NTS | WT: | SHEET: 01 OF 01