




DWG.NO: SALT_1714_STR_02_R0

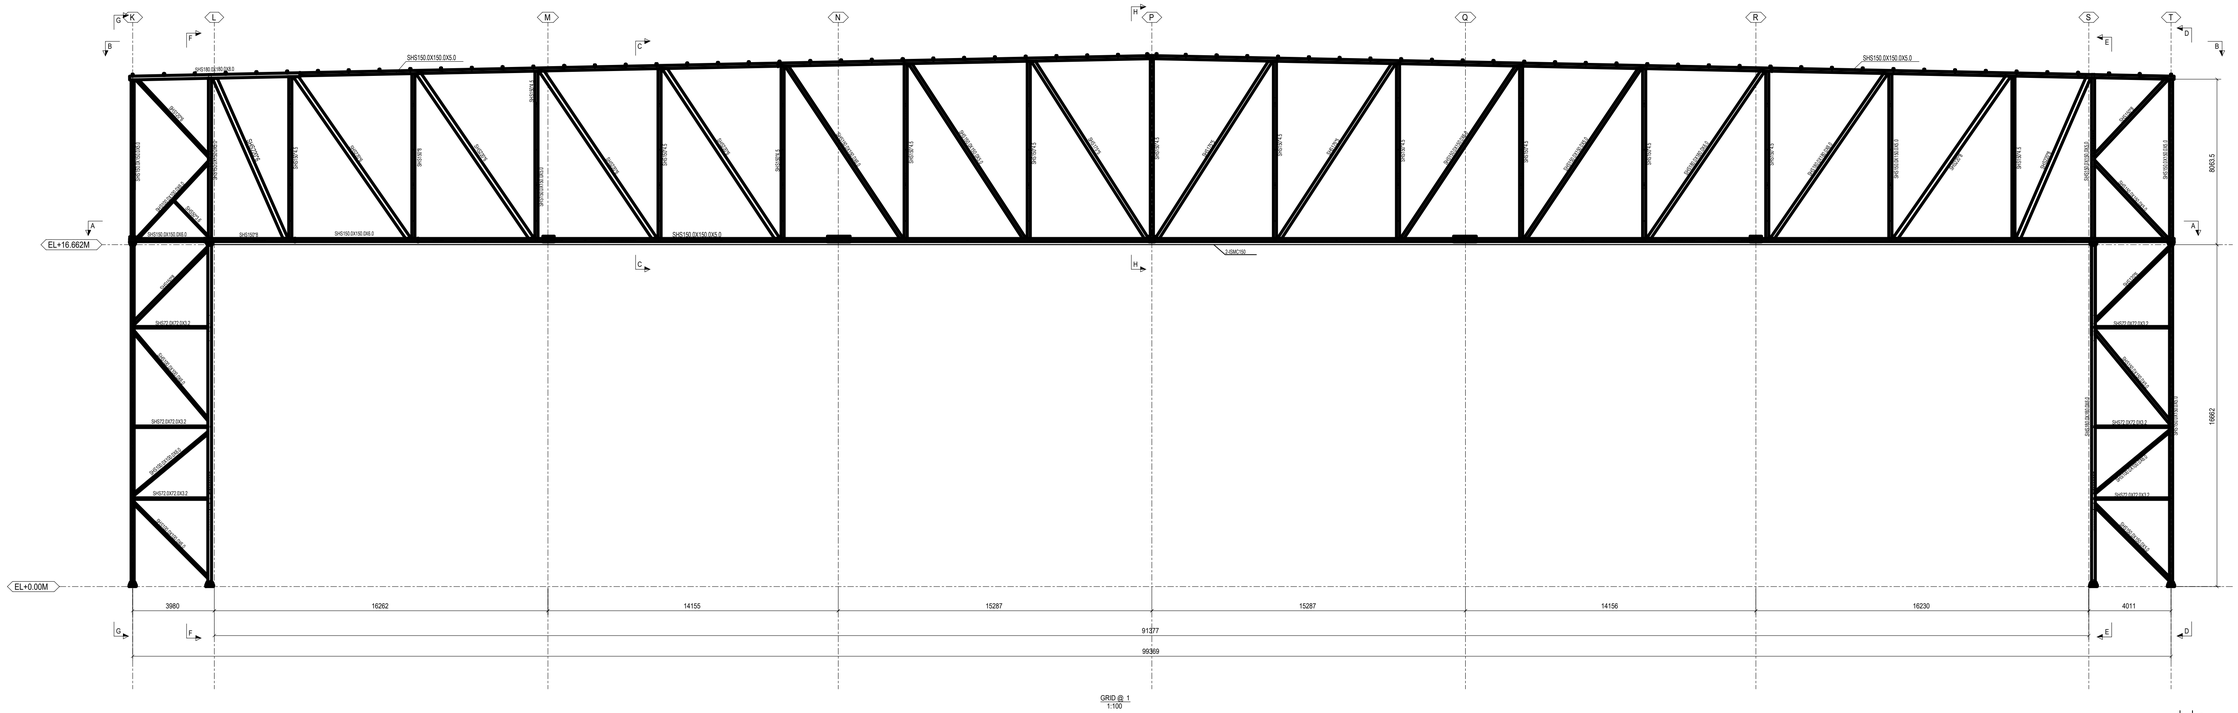

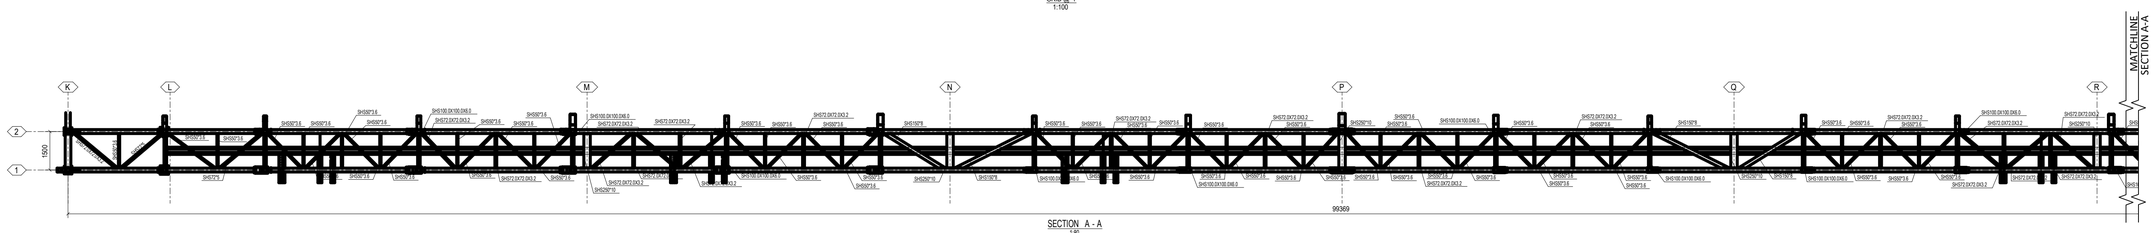

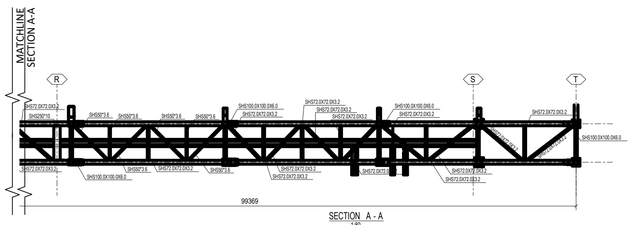

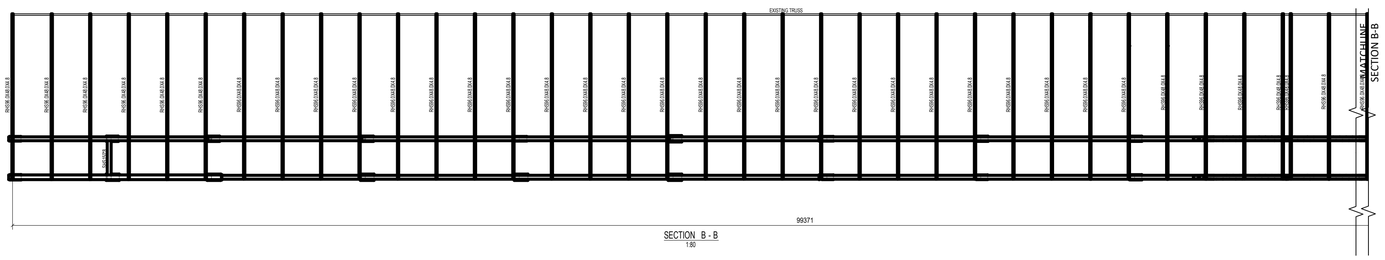

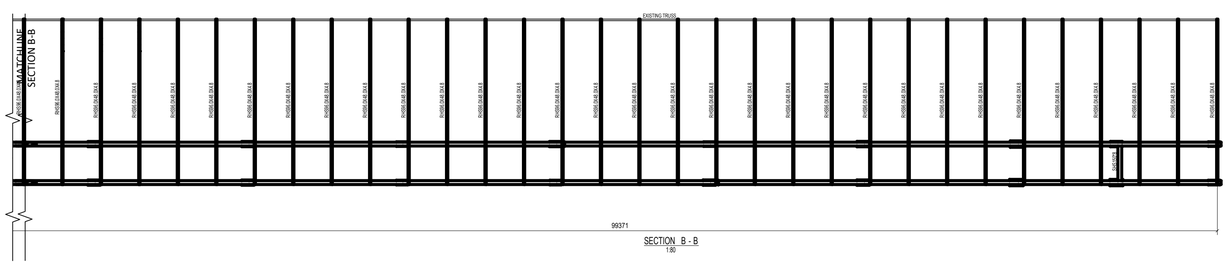

REV.NO.	DESCRIPTION.	REV.DATE	DRAWN.	CHKD.	APPD.
0					

DWG.TITLE :- STRUCTURAL DRAWING FOR DOOR FRAME

PROJECT	HANGAR DOOR
CLIENT	GMR

SALT Design Services

SALT DESIGN SERVICES
4-PUSHKAR NIRZAR, SBI COLONY,
NEAR ICICI BANK, KOTHRUD, PUNE-411038.

DRAWN :CDD	CHECKED : HAB	SCALE: 1:100
APPROVED : HAB	JOB CODE. : 1714	DATE: 22.10.2022

DWG.NO: SALT_1714_STR_02_R0 (SH-1OF2) REV. - R0 SIZE. - A0

A0 [841 x 1189]