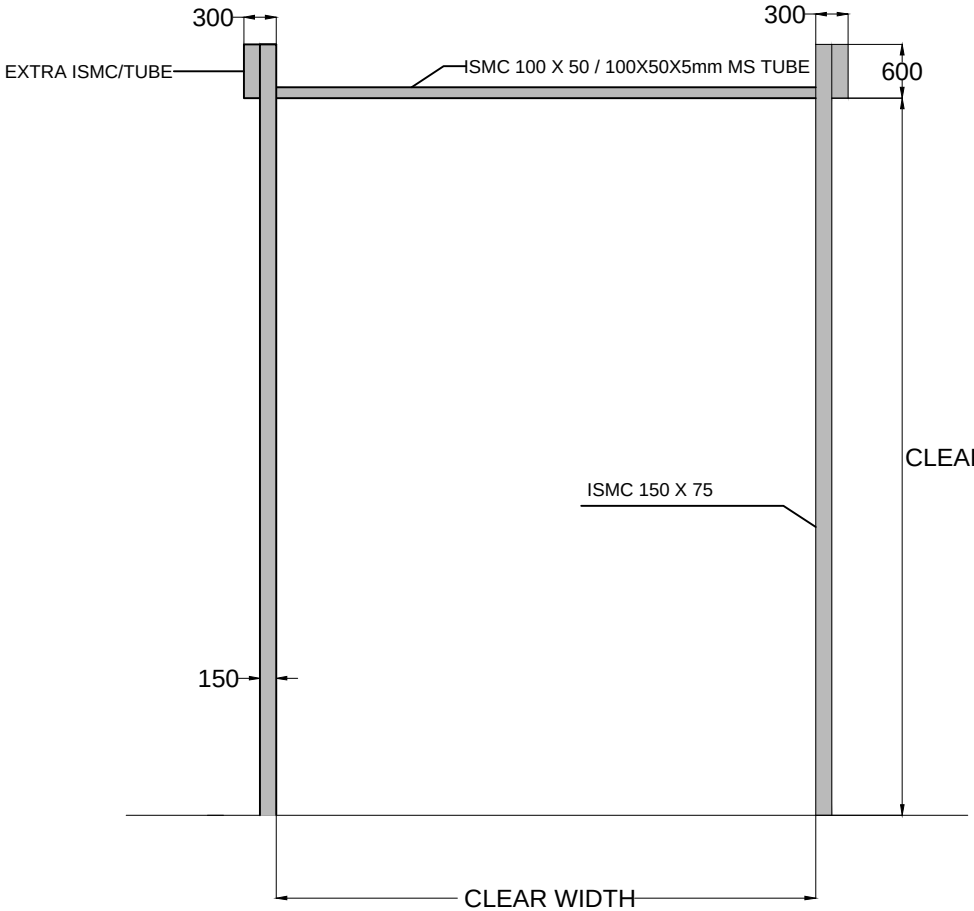


STRUCTURE FOR MOTORIZED ROLLING SHUTTER.

NOTE :

1. MATERIAL FOR ALL STRUCTURE = M.S
2. ALL CIVIL WORK WILL BE IN CLIENT SCOPE.
3. REQUIRED STEEL STRUCTURE IN CLIENT SCOPE.

CLEAR WIDTH	CLEAR HEIGHT	QTY.
5000	3000	01NO
3000	3000	03 NOS
5000	7000	02 NOS

TOLERANCE - ±10mm

This drawing & design is the property of NIHVA TECHNOLOGIES. Not to be sold or copied to any other concern.

TITLE: STRUCTURE FOR GEAR OPERATED ROLLING SHUTTER

	NAME	SIGN	DATE
DRAWN	P.V.A		25.03.2019
CHECK	V.M.T		25.03.2019
APPRD.			

If any queries contact : design@nihva.com

ALL DIMENSION ARE IN mm

NIHVA TECHNOLOGIES PVT. LTD.
NIHVA TECHNOLOGIES PVT. LTD. PUNE
Tel : 020 66304033
Email:- info@nihva.com
Website:- www.nihva.com

CLIENT - UNITED ARCHITECT

PROJECT - A RAYMOND

SITE LOCATION - CHAKAN

DWG. NO. : NIHVA/18-19/0315 | REV- 00

SCALE: NTS | WT: | SHEET: 01 OF 01