
SR NO	DESCRIPTION	QTY
01	ISMC 75 X 40 X 1800L	2 NOS
02	ISMC 75 X 40 X 888l	2 NOS
03	PROFILE 75 X 12 THK X 86L	4 NOS
04	BEND 400 X 5 X 900L	1 NO
05	RIB 70 X 5 THK X 290L	2 NOS
06	PIPE OD27 X 2.65 THK X 2600L	1 NO
07	FLAT 100 X 16 THK X 160L	2 NOS
08	NYLON WHEEL DIA 150 X 50 MEDIUM DUTY WITH BRAKE & SW CASTOR BRACKET	2 NOS
09	NYLON WHEEL DIA 150 X 50 MEDIUM DUTY WITH FIX BKT	2 NOS
10	GRUB SCREW M6 X 20L	2 NOS
11	M10 X 50L	16 NOS
12	PIPE ELBOW DIA 27	02 NOS
13	PIPE OD 27 X 2.65 THK X 145L	04 NOS

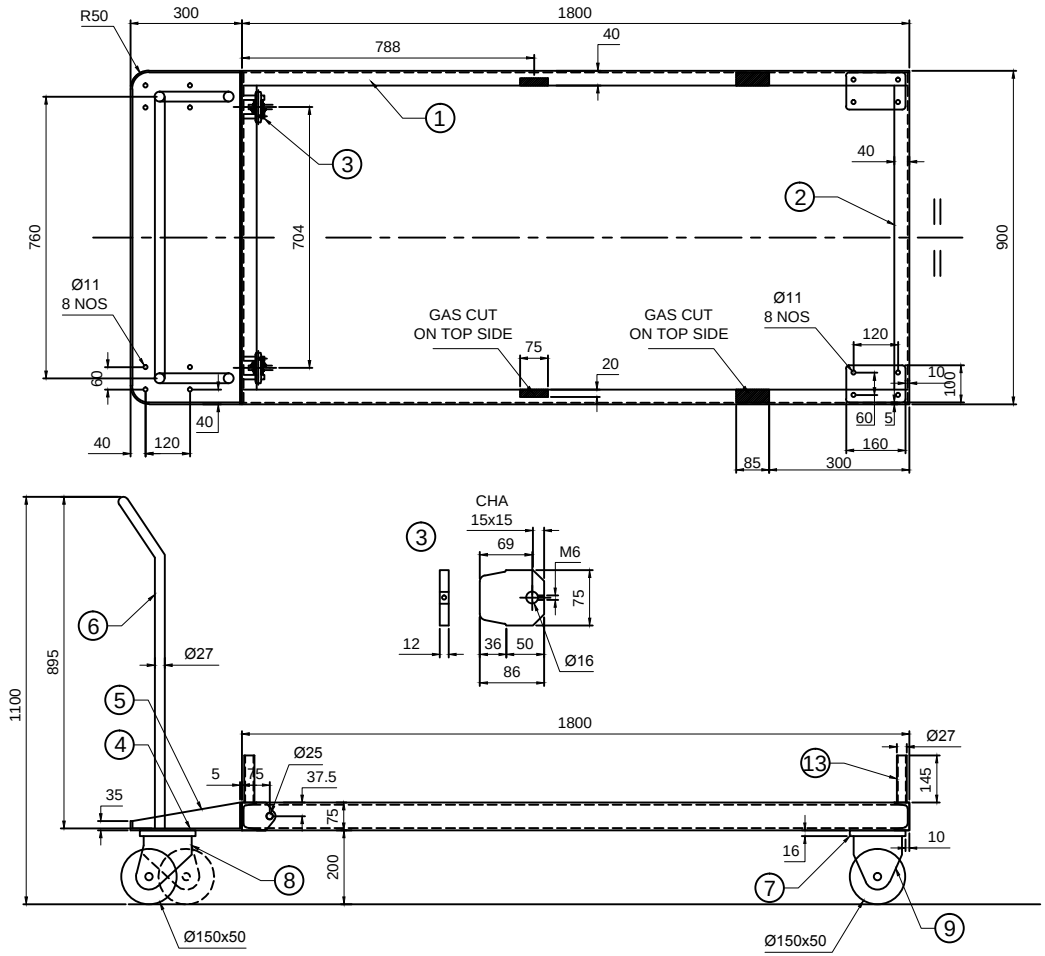

This drawing & design is the property of NIHVA TECHNOLOGIES. Not to be sold or copied to any other concern.

TITLE

BASE FRAME ASSLY

	NAME	SIGN	DATE
DRAWN	P.A		03.12.18
CHECK	P.A		03.12.18
APPRD.	R.D		03.12.18

If any queries contact : design@nihva.com

ALL DIMENSION ARE IN mm

NIHVA TECHNOLOGIES PVT. LTD.

NIHVA TECHNOLOGIES PVT. LTD. PUNE
Tel : 020 66304033
Email:- info@nihva.com
Website:- www.nihva.com

CLIENT -

PROJECT -

SITE LOCATION -

DWG. NO. : NIHVA/18-19/MFG/NSL1003/01 | REV- 0

SCALE: NTS | WT: | SHEET: 01 OF 01