



SIDE VIEW

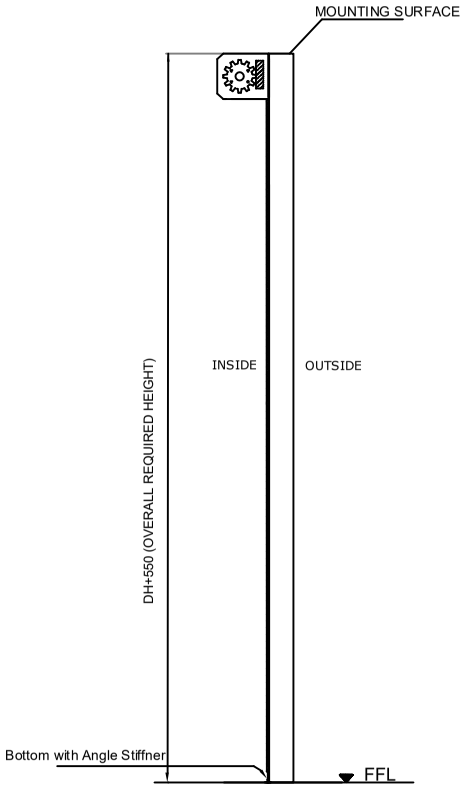

OUTSIDE ELEVATION

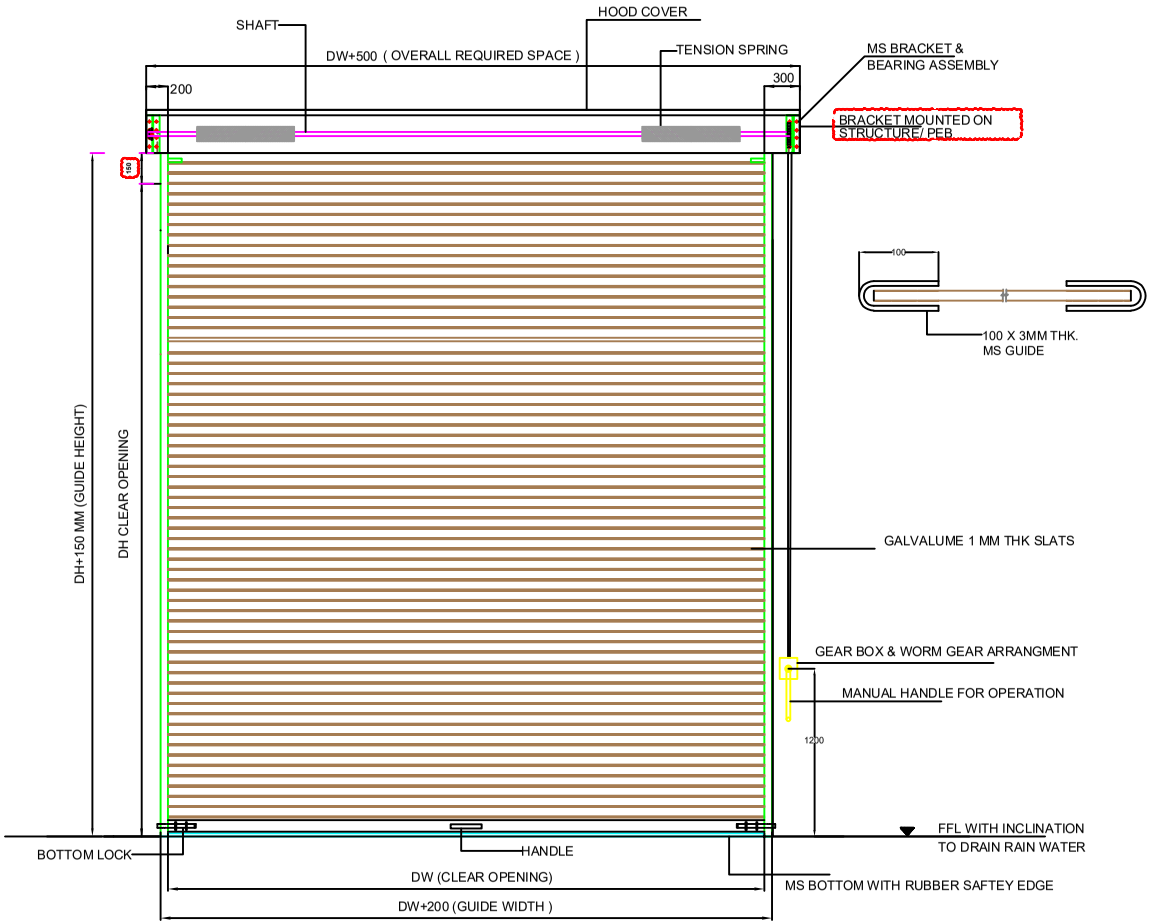

PLAN

TECHNICAL SPECIFICATION:-

SR.	SPECIFICATION	DETAILS
1.	Description & Drive	Gear Operated Rolling Shutter
2.	Location Area	Inside / Outside
3.	Mounting Surface	Side Brackets: Optional = On Concrete
4.	Slat	Galvalume - 1.0mm thick
5.	Bottom Profile	MS Plate 100 x 2.5 mm thick
6.	Guide Profile	M.S." U" Shaped profile 100 x 3 mm thick
7.	Hood Cover	Made of GI Sheet Thickness 0.9 mm

NOTE:-

1. ALL DIMENSION ARE IN MM
2. ALL CIVIL WORK WILL BE IN CLIENT SCOPE.
3. MOUNTING: MS STRUCTURE MOUNTING WILL BE IN CLIENT SCOPE

CLEAR WIDTH (DW)	CLEAR HEIGHT (DH)	QTY
3000 mm	3000 mm	2 nos

This drawing & designing is the property of NIHVA TECHNOLOGIES. Not to be sold or copied to any other concern.

TITLE :-
GEAR OPERATED ROLLING SHUTTER

NIHVA TECHNOLOGIES PVT. LTD.
Tel : 020 66304033
Email:- info@nihva.com
Website:- www.nihva.com

	NAME	DATE
DRAWN	S.J	12/01/2024
CHECK	A.K.	12/01/2024
APPROVAL	V.T.	12/01/2024

CLIENT - KSH Infra Park 4 Private Limited
PROJECT -ROLLING SHUTTER
DWG. NO. : NIHVA/SO/23-24/062
REV-01

If any queries contact : design@nihva.com
SCALE: NTS | QTY:02 NO. | SHEET: 01 OF 01
ALL DIMENSION ARE IN mm