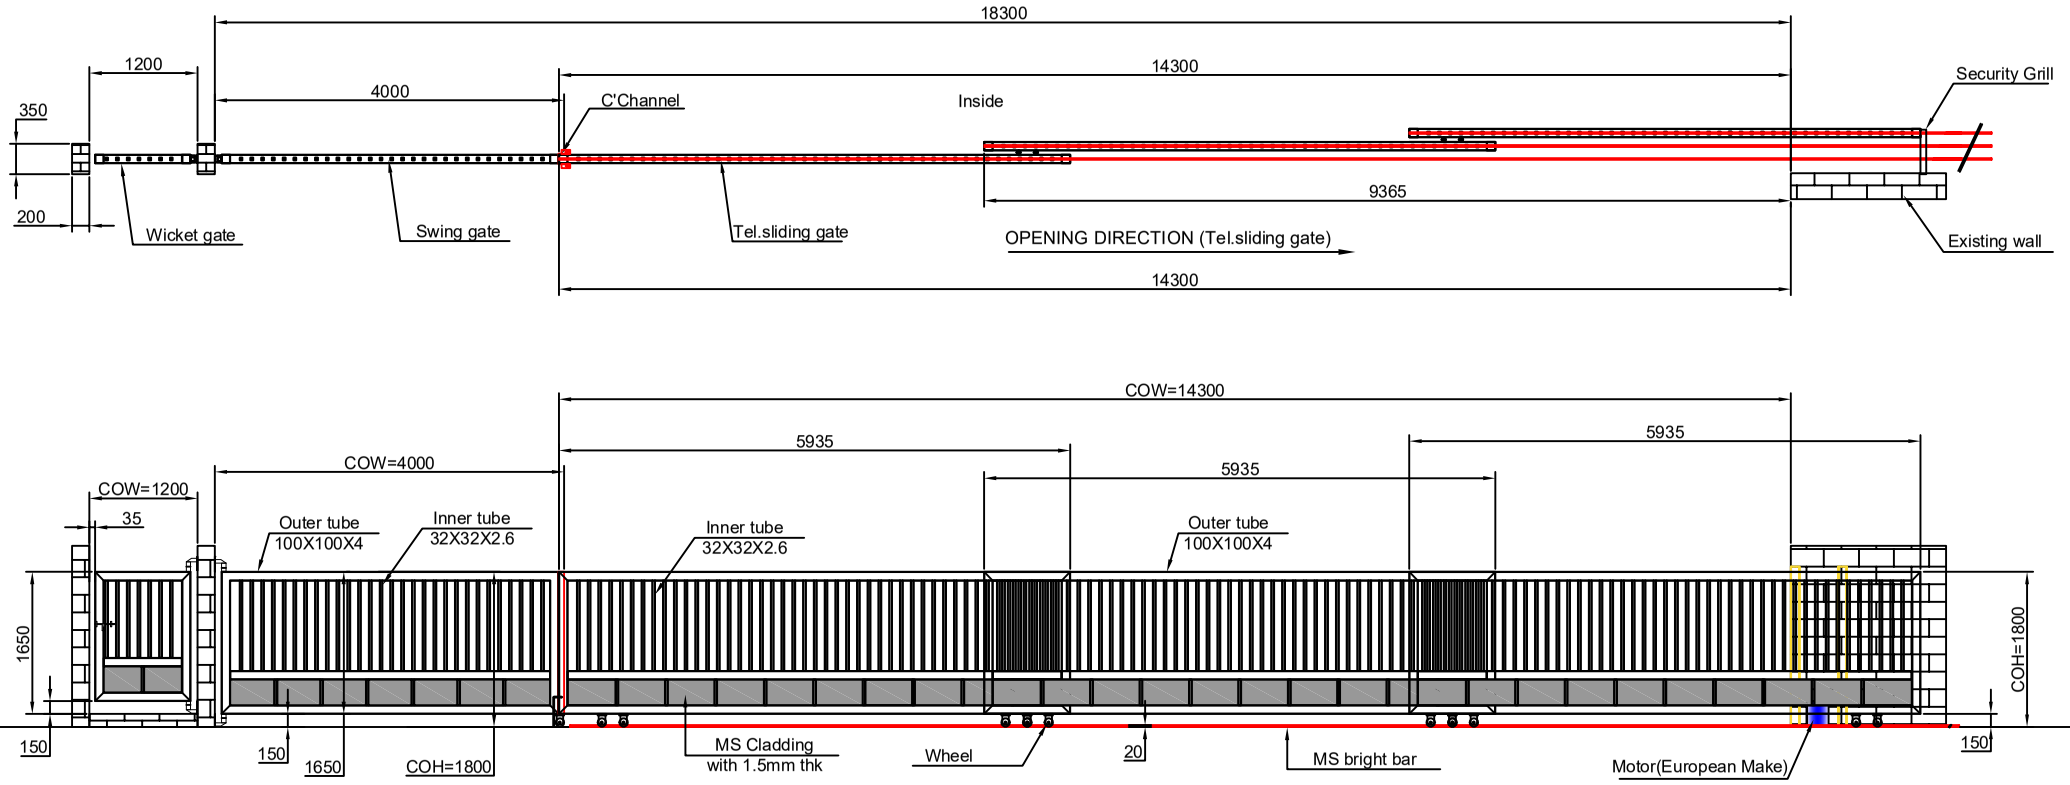


Note-

1. All dimension are in mm.
2. All civil work is under client scope.
3. 3" PVC pipe in the foundation to be provided by client.
4. Paint: 2 Coats of EPOXY polyamide based enamel finish of approved Colour
5. COW=Clear opening width
6. COH=Clear opening Height

This drawing & design is the property of NIHVA TECHNOLOGIES. Not to be sold or copied to any other concern.

TITLE:- GATE				NIHVA TECHNOLOGIES PVT. LTD. PUNE Tel : 020 66304033 Email:- info@nihva.com Website:- www.nihva.com
	NAME	DATE	SIGN	
DRAWN	SUJATA.B	31/01/2022		CLIENT - Fanidhar Mega Food Park Private Limited
CHECK	G.PATIL	31/01/2022		LOCATION - GUJARAT
APPRD.	A.K	31/01/2022		PRODUCT - GATE
If any queries contact : design@nihva.com				DWG NO:-NIHVA/21-22/CLT/0298 REV- 2
ALL DIMENSION ARE IN mm				SCALE: NTS SCALE:-- 1:1 SHEET: 01 OF 01

Rev No.	Revision	Date	Revised By