
LOCATION AREA :- SEZ 1 C - GROUND FLOOR- EXIT

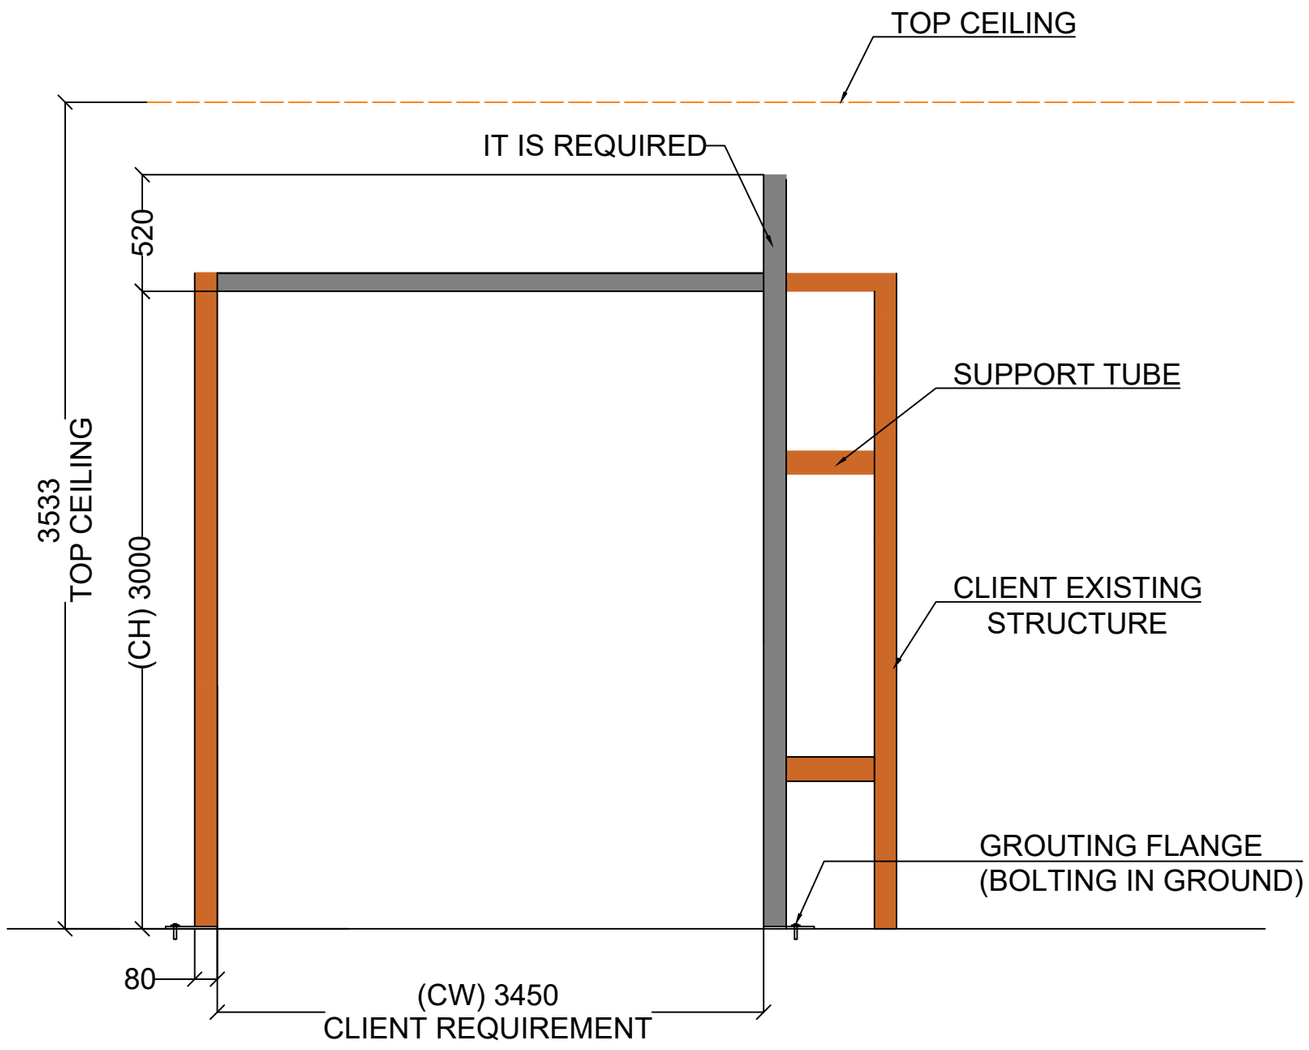

M.S. STRUCTURE DETAILS

Clear Width (CW)	Clear Height (CH)	QTY
3450	**3000**	01

NOTE :-

1. ALL DIMENSIONS ARE IN MM
2. THIS DRAWING IS SOLELY MEANT TO BE UNDERSTOOD.
3. REQUIRED HEIGHT & ACTUAL HEIGHT PLEASE CONFIRM BY CLIENT

This drawing & design is the property of NIHVA TECHNOLOGIES. Not to be sold or copied to any other concern.

TITLE:- HIGH SPEED DOOR STRUCTURE DRAWING				NIHVA TECHNOLOGIES PVT. LTD. PUNE Tel : 020 66304033 Email:- info@nihva.com Website:- www.nihva.com	
	NAME	SIGN	DATE		
DRAWN	S.J		14.11.2024	CLIENT - SERUM INSTITUTE OF INDIA PVT.LTD	
CHECK	S.W.		14.11.2024	PROJECT - HIGH SPEED DOOR ST.	
APPRD.	V.T		14.11.2024	FORMAT NO - NIHVA-DD-F-03	
If any queries contact : projectsupport@nihva.com				DWG. NO. : NIHVA/24-25/SM/24100401	REV- R00
ALL DIMENSION ARE IN mm				SCALE: NTS	WT: SHEET: