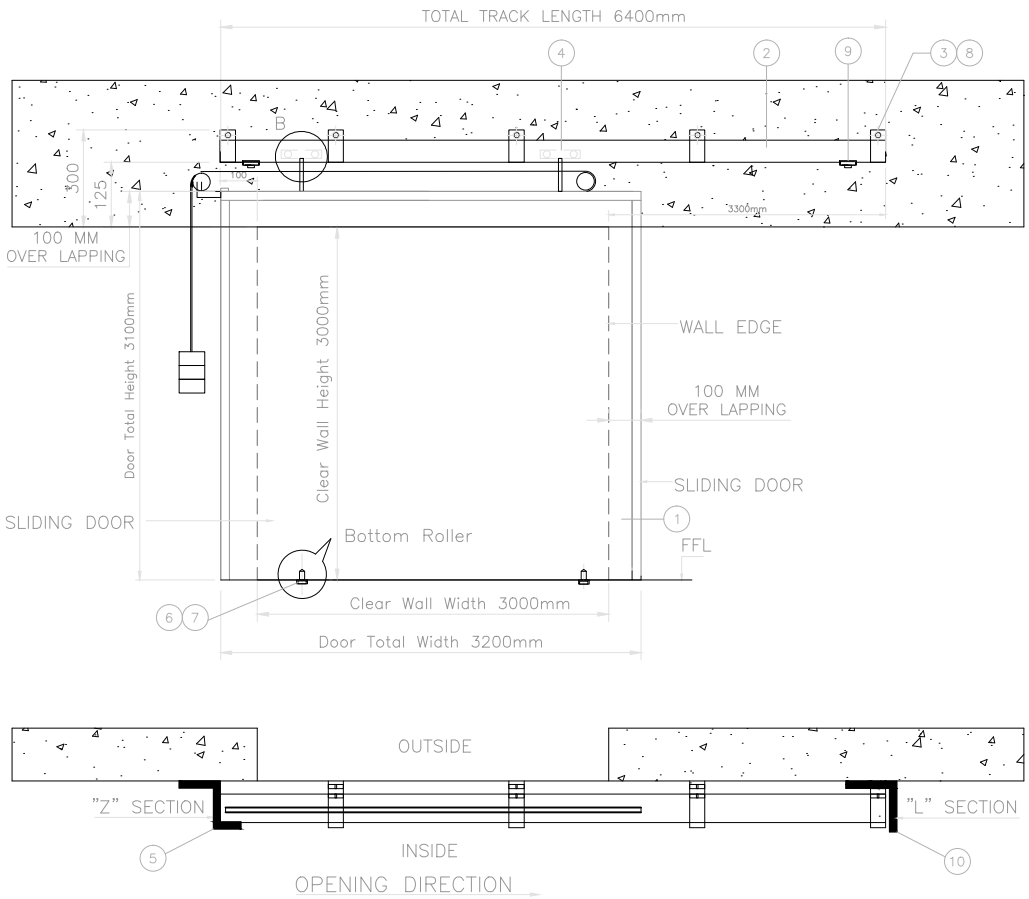

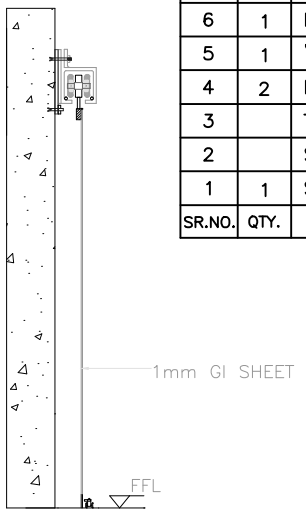

SR.NO.	QTY.	DESCRIPTION
10	1	'L' SECTION
9	1	STOPPER (FOR HANGER ASSLY.)
8	1	COVER (FOR TRACK BKT.)
7	1	BOTTOM ROLLER MTG. FLAT (BOTTOM ROLLER BKT.)
6	1	BOTTOM ROLLER ASSLY.
5	1	'Z' SECTION
4	2	HANGER ROLLER ASSLY.
3		TRACK BRACKET
2		SLIDING TRACK
1	1	SLIDING DOOR & FRAME / BACK SUPPORT SQ. TUBE

DOOR DIMENSION	
CLEAR WIDTH	CLEAR HEIGHT
3000mm	3000mm

NOTE : DOOR OVERLAPING 100mm AT RH & LH AND TOP SIDE
ALL DIMENSIONS ARE IN MM.
CLIENT SHOULD CONFIRM DOOR OPENING DIRECTION.

This drawing & designing is the property of NIHVA TECHNOLOGIES. Not to be sold or copied to any other concern.

TITLE: MANUAL SLIDING DOOR

NIHVA TECHNOLOGIES PVT. LTD. PUNE
Tel : 020 66304033
Email:- info@nihva.com
Website:- www.nihva.com

	NAME	SIGN	DATE
DRAWN	SURAJ		10/07/18
CHECK	R.D		10/07/18
APPROVAL	R.D		10/07/18

CLIENT - REWARD CONSTRUCTIONS PVT LTD.
PROJECT - REWARD CONSTRUCTIONS PVT LTD.
SITE - RANJANGAON MIDC.

If any queries contact : design@nihva.com
DWG. NO. : NIHVA/18-19/0053 REV- 0
ALL DIMENSION ARE IN mm
SCALE: NTS WT: SHEET: 01 OF 01