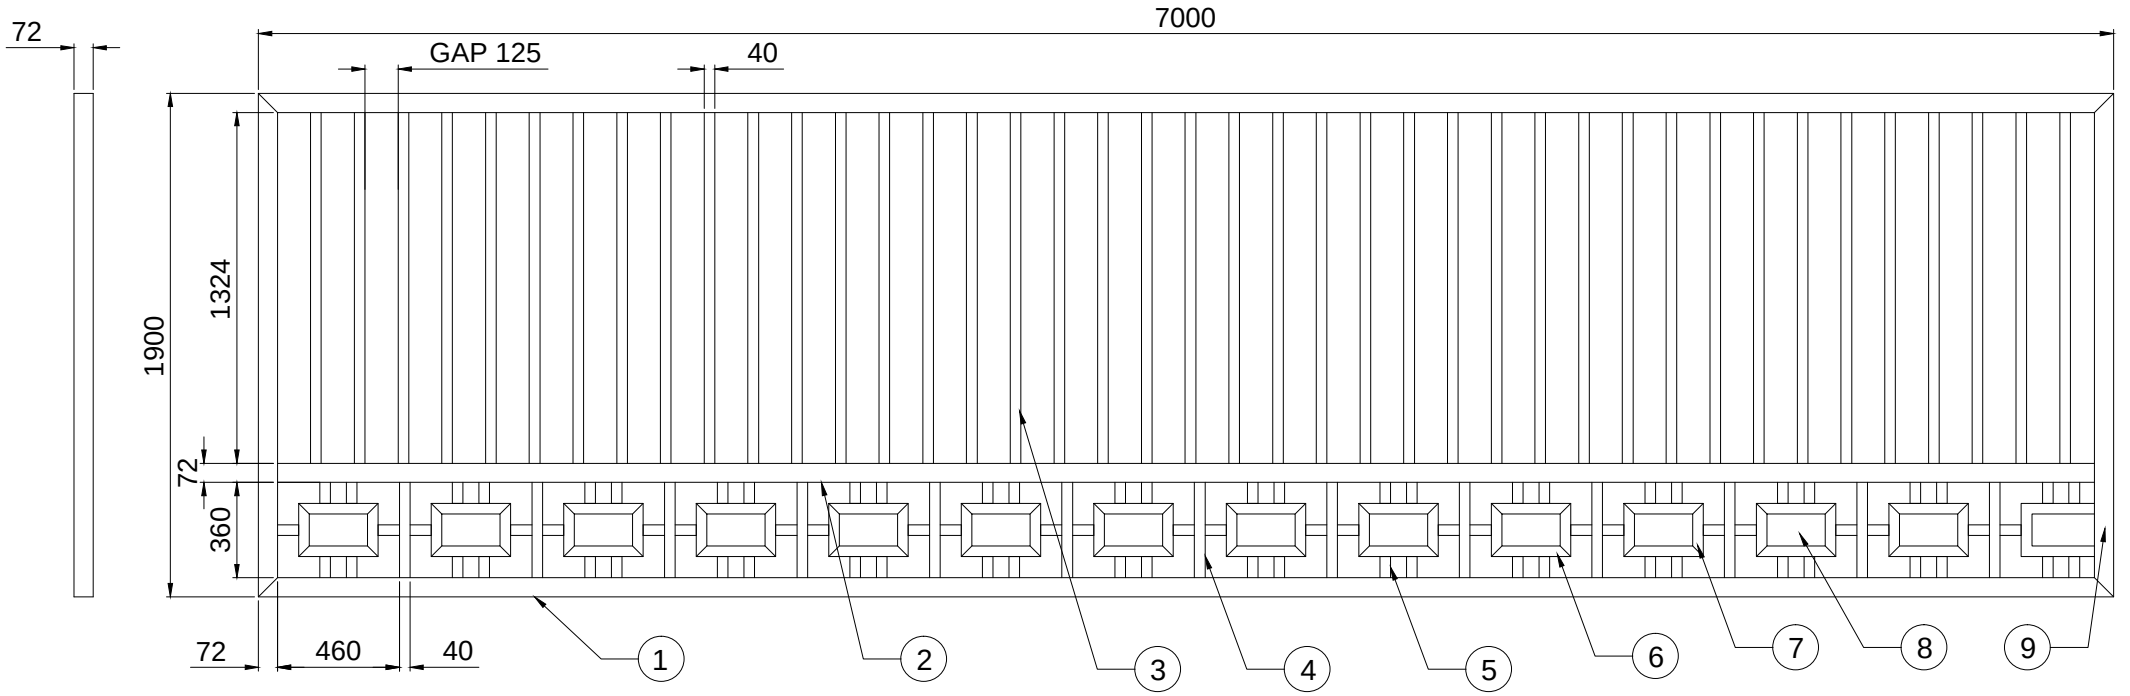


SR NO	DESCRIPTION	SPECIFICATION	QTY
9	SQ.TUBE	72 X 72 X 3.2 THK X 1900L	2 NOS
8	M.S SHEET	180 X 2 X 280L	14 NOS
7	SQ.TUBE	40 X 40 X 2.6 X 200L	28 NOS
6	SQ.TUBE	40 X 40 X 2.6 X 300L	28 NOS
5	SQ.TUBE	40 X 40 X 2.6 X 80L	84 NOS
4	SQ.TUBE	40 X 40 X 2.6 X 360L	13 NOS
3	SQ.TUBE	40 X 40 X 2.6 X 1324L	42 NOS
2	SQ.TUBE	72 X 72 X 3.2 THK X 6855L	1 NO
1	SQ.TUBE	72 X 72 X 3.2 THK X 7000L	2 NOS

TOLERANCE - ±2mm

This drawing & design is the property of NIHVA TECHNOLOGIES. Not to be sold or copied to any other concern.

TITLE: LEAF DRAWING

NIHVA TECHNOLOGIES PVT. LTD. PUNE
Tel : 020 66304033
Email:- info@nihva.com
Website:- www.nihva.com

	NAME	SIGN	DATE
DRAWN	P.V.A		26.09.2019
CHECK	G.J		26.09.2019
APPRD.			

CLIENT -

PROJECT -

SITE LOCATION -

If any queries contact : design@nihva.com

DWG. NO. : NIHVA/19-20/VDR/156 REV- 0

ALL DIMENSION ARE IN mm

SCALE: NTS WT: SHEET: 01 OF 01