



GALVANISED STEEL GUIDE RAIL

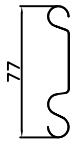

SHUTTER SLAT

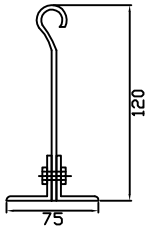


BOTTOM BAR

SHUTTER TYPE	FIRE RATED ROLLING SHUTTER
SHUTTER SLATS	ZINCALUME STEEL
FINISHING OF SLATS	POWER COAT STANDARD RAL COLOUR
GUIDE RAIL	GALVANISED SURFACE MOUNTED
BOX DESIGN	MILD STEEL SECTION FRAME DESIGN
BOX COVER PLATE	08MM ZINCALUME STEEL SHEET
OPERATION	MOTORISE WITH MANUAL OVERRIDE CHAIN
MOTOR POWER SOURCE	230 VOLTS,1 PHASE,50HZ


LOCATION	SHUTTER NO.	CLEAR WIDTH	CLEAR HEIGHT	QUANTITY
	FRS	4000MM	4500MM	8

REMARKS :-


PEB STRUCTURE MUST ABLE TO WITHSTAND THE SHUTTER WEIGHT 30KG/M2 (MINIMUM 300KGS)

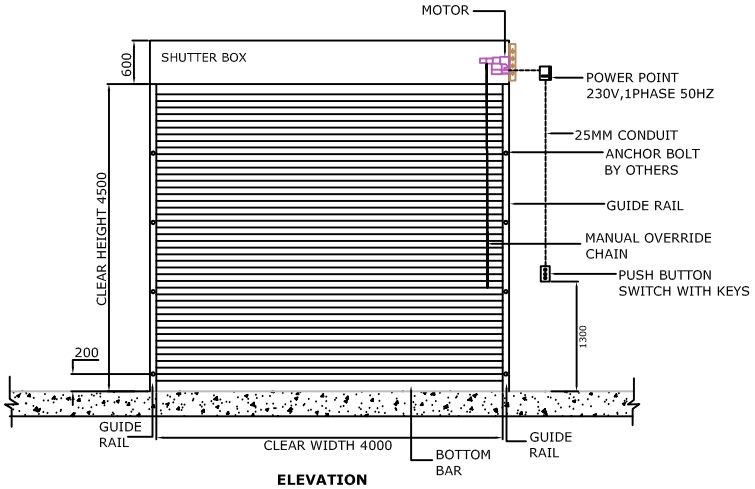

ELEVATION

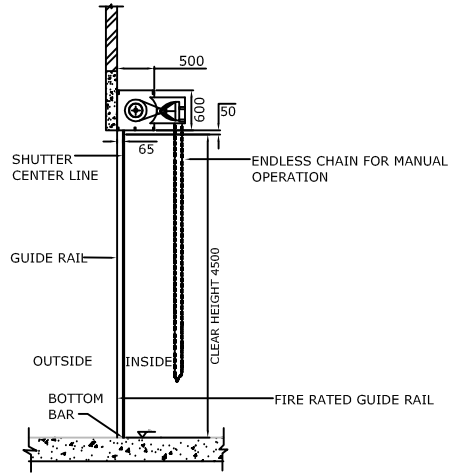

SIDEVIEW

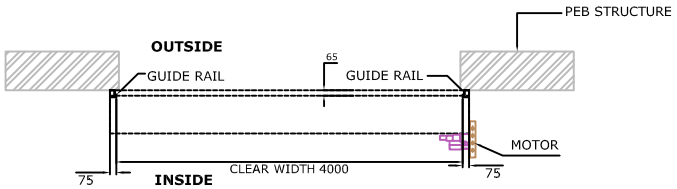

PLAN

FIRE RATED SHUTTER SIZE:- 4000(W) X 4500 (H)

SHUTTER QTY :- 08 NO

TITLE: FIRE RATED ROLLING SHUTTER	DO NOT SCALE DRAWING			
		SIGN	DATE	
CLIENTS APPROVEL:–	DRAWN ANIL		21–04–14	
	CHECK VT		21–03–14	CLIENT:
	ENG			PROJECT / SITE:
	APPRD.			PRODUCT NAME: FIRE.RATED–ROLLING.SHUTTER
UNLESS & OTHERWISE SPECIFIED DIMENSION ARE IN M.M.	PROD			DWG. NO.:
	MFG			REV.: 0
If any queries CONTACT: projects@avians.co.in	Ref. No.			SCALE: NTS WT: SHEET: 1 OF 1