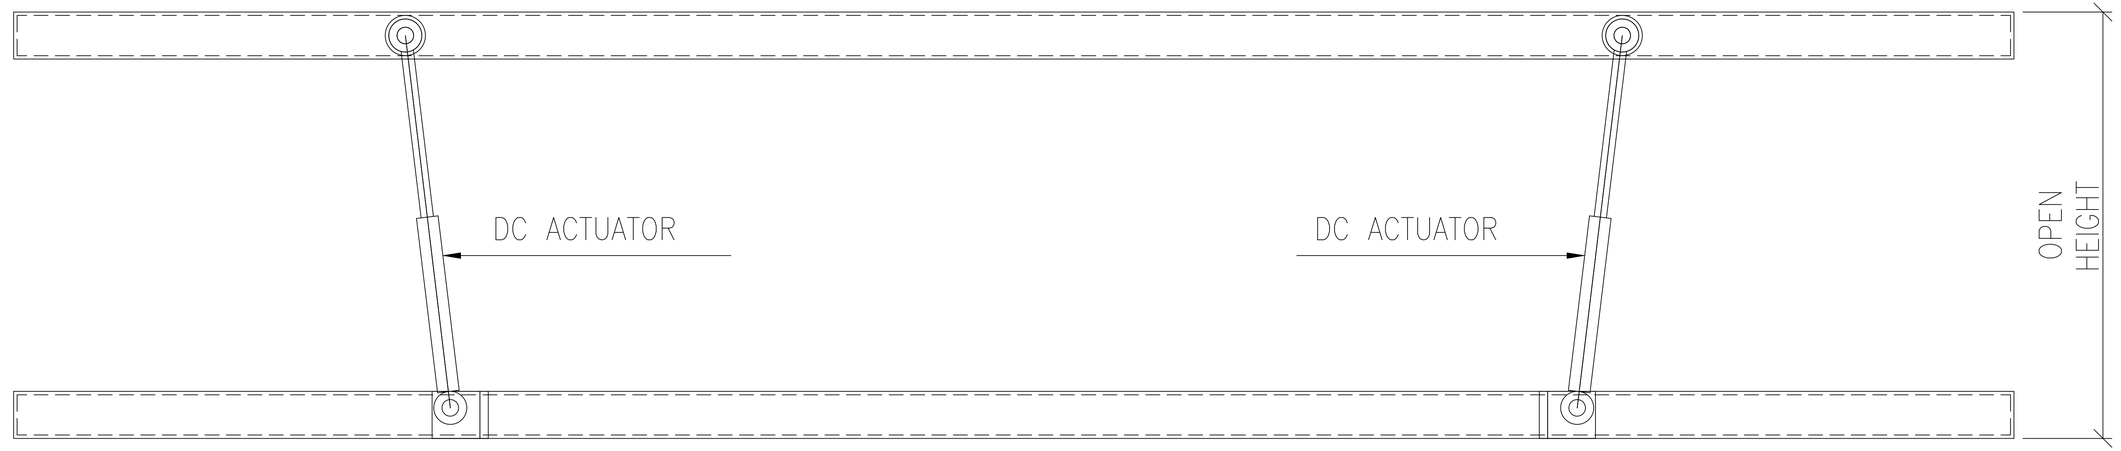
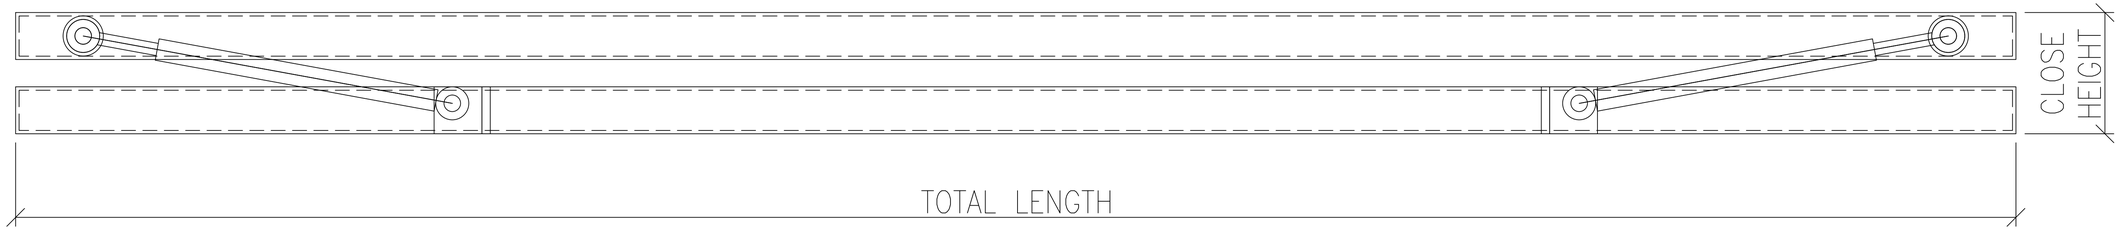



NOTE :–

TOTAL ACTUATORS : 2 NOS
STROKE LENGTH : 450MM OR ABOVE
ACTUATOR LIFTING CAPACITY : 500 KGS (EACH)

TOLERANCE :- ± 5mm

This drawing & design is the property of NIHVA TECHNOLOGIES. Not to be sold or copied to any other concern.

TITLE
CRANE DOOR

| | NAME | SIGN | DATE |
|---|---|---|---|
| DRAWN | P.V.A | | 09.09.19 |
| CHECK | V.M.T | | 09.09.19 |
| APPRD. | | | |

NIHVA
NIHVA TECHNOLOGIES PVT. LTD.
Website:- www.nihva.com
NIHVA TECHNOLOGIES PVT. LTD. PUNE
Tel : 020 66304033
Email:- info@nihva.com

CLIENT -
PROJECT -
SITE LOCATION -

If any queries contact : design@nihva.com
DWG. NO. : NIHVA/19-20/ REV- 00
ALL DIMENSION ARE IN mm
SCALE: NTS WT: SHEET: 01 OF 01