


SIDE VIEW

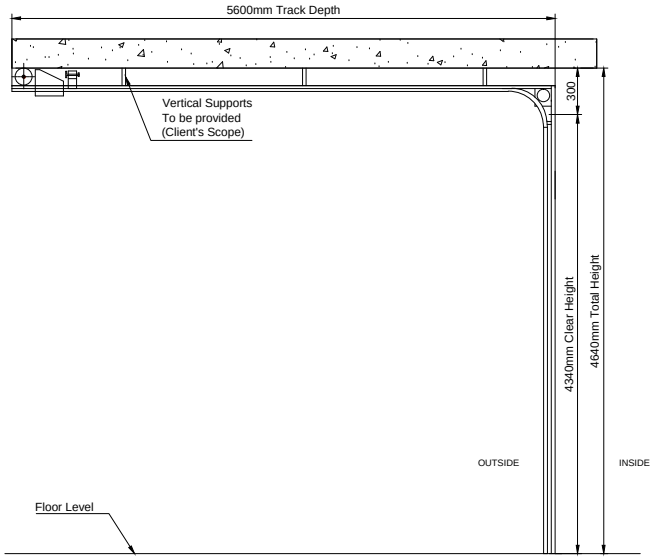


OUTSIDE ELEVATION




TRACK DETAILS

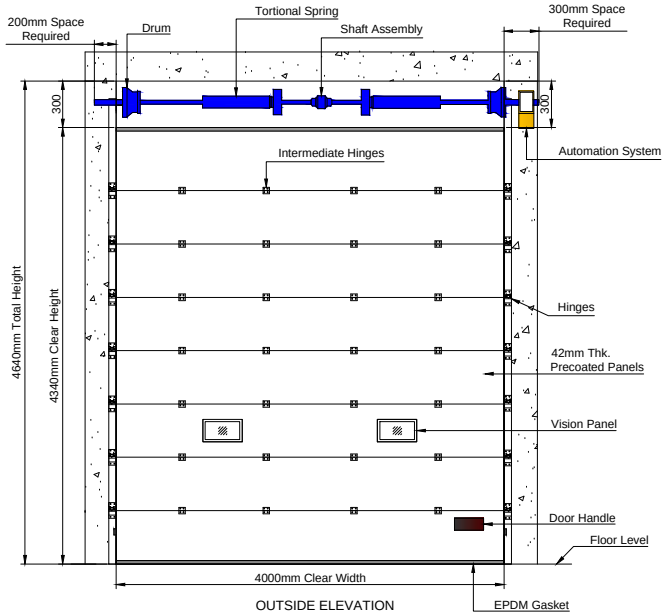


PLAN

| SR NO | REVISION | DESCRIPTION |
|---|---|---|
| 1 | REV 0 | INITIAL DRAWING |
| 2 | REV 1 | DOOR WILL BE MOUNTED FROM OUTSIDE |

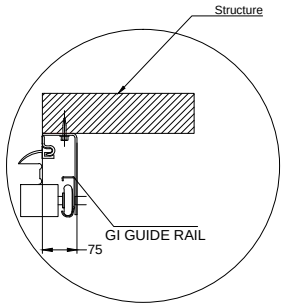DIMENSION :

| CLEAR WIDTH | CLEAR HEIGHT | QUANTITY |
|---|---|---|
| 4000 mm | 4340 mm | 4 |

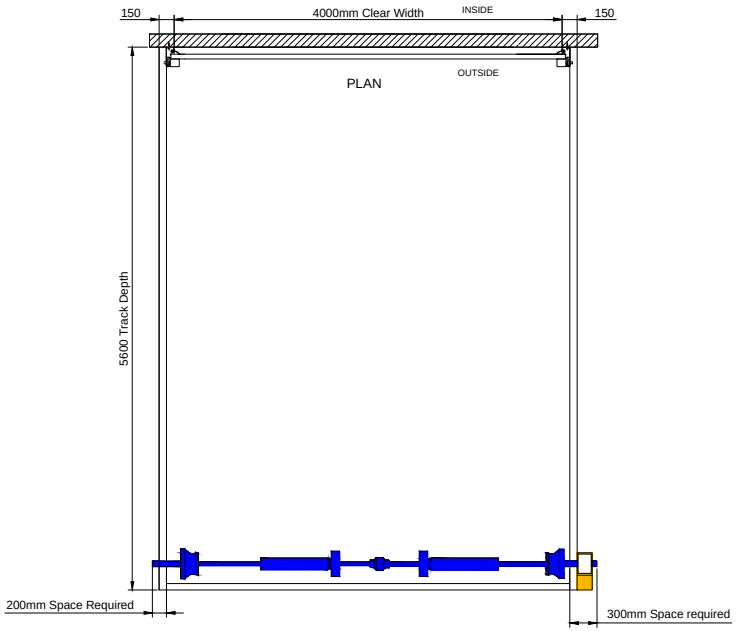TECHNICAL DATA :

| COMPONENTS | MATERIALS | SPECIFICATIONS |
|---|---|---|
| DOOR PANELS | GI & PUF | 42mm CFC- FREE POLYURETHANE WITH 0.5mm THK, GI PRECOATED PANELS. |
| DOOR HINGE | —— | HEAVY DUTY HINGES FOR INTERLOCKING OF PANELS |
| SHAFT ASSEMBLY | STD. | TORSIONAL SPRING WITH SHAFT & BEARING PLATES |
| FINISH | | ENAMEL PAINT WITH APPROVED SHADE |

ACCESSORIES-
1. SAFETY PHOTOCELL- 1 PAIR /DOOR

IMPORTANT NOTES:

1. REQUIRED STRUCTURE FOR DOOR SHALL BE IN CLIENT'S SCOPE.
2.SINGLE PHASE POWER SUPPLY REQUIRED AT DOOR LOCATION.
3.ALL CIVIL WORK SHALL BE CLIENT'S SCOPE.

NIHVA TECHNOLOGIES PVT. LTD. PUNE
Email:- info@nihva.com
Website:- www.nihva.com

TITLE:

SECTIONAL DOOR LL (MOTORIZED)

CLIENT'S APPROVAL :

CLIENT - MAVIN ARCHITECTURAL SOLUTIONS PVT. LTD.

PROJECT - CHENNAI TRADE CENTRE

SITE LOCATION - CHENNAI

DWG. NO. : NIHVA/17-18/0334/R01 | REV- 1

SCALE: NTS | WT: | SHEET:1 OF 1

DRAWN BY: OMKAR | DATE: 12-01-2018

CHECK BY: SHEKHAR | DATE: 12-01-2018

APPROVED BY : SHEKHAR | DATE: 12-01-2018

If any queries contact : design@nihva.com

NOTE: ALL DIMENSIONS ARE IN mm

THIS DRAWING & DESIGNING IS THE PROPERTY OF NIHVA TECHNOLOGIES. NOT TO BE SOLD OR COPIED TO ANY OTHER CONCERN.