

Abbrevation's:
WOW-Wall Opening Width
WOH-Wall Opening Height
CH- Clear Height
UC-Under Cut
FFL-Finished Floor Level

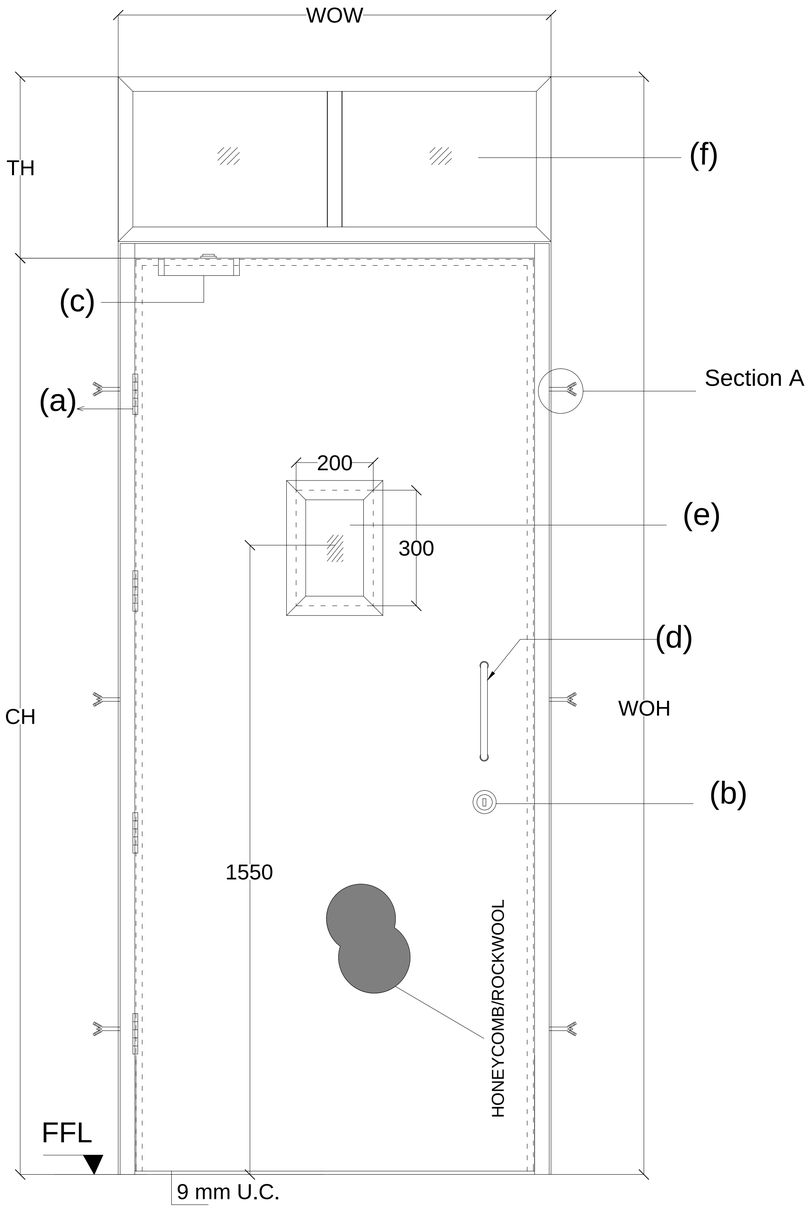


ELEVATION

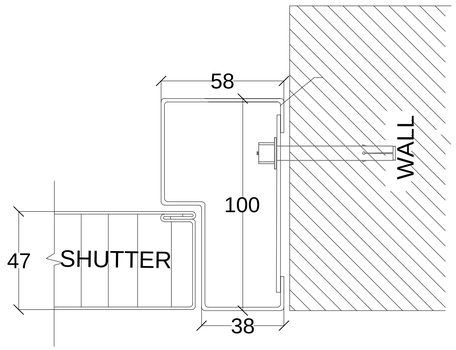

TOP VIEW




## ASSESORIES DETALES

(a) HINGES: SS hinges 100x75x3mm

(b) LOCK : Mortise dead Lock with cylinder(One side key & thumb turn on other side)with escutcheon.

(c) DOOR CLOSER : B4W

(d) HANDLE : D Handle (300x22) pair.

(e) VISION PANEL - 5mm THK. GLASS OF SIZE-200X300mm

(f) FIXED GLASS- 5mm THK. FIXED GLASS WITH FRAME.

Shutter thickness : 47 mm
Frame Sheet thick : 1.20mm
Shutter sheet thick : 0.80mm
Fixing : On Soliid Brick plasterd wall with Anchors

NOTE:- *All Dimensions are in mm.
*Tolerance:-All Linear Dimensions ±3mm,Others ±0.5mm.
*The Drawing Is For Location of Hardware only. Drawing Does Not Represent The Hardware For More Clarity, Please Go Through Hardware Broucher.

## Fire door size

| WOW | WOH | CH | TH | TYPE 1 | TYPE 2 | TYPE 3 | TYPE 4 | QUANTITY |
|---|---|---|---|---|---|---|---|---|
| 1192 | 2985 | 2400 | 585 | | | | | 1 |

NOTE- CLIENT SHOULD SELECT DOOR TYPE FROM DOOR HANDLING SHEET & COLOR OF DOOR.

This drawing & designing is the property of NIHVA TECHNOLOGIES. Not to be sold or copied to any other concern.

TITLE
STEEL DOOR
WITH FIXED GLASS

NIHVA TECHNOLOGIES PVT. LTD.
NIHVA TECHNOLOGIES PVT. LTD. PUNE
Tel : 020 66304033
Email:- info@nihva.com
Website:- www.nihva.com

| | SIGN | DATE |
|---|---|---|
| DRAWN | OMKAR | 11/07/17 |
| CHECK | SHEKHAR | 11/07/17 |
| REV. | 00 | |
| APPROVAL | | |

If any queries contact : projects@nihva.com

ALL DIMENSION ARE IN mm

CLIENT - VAICHAL CONSTRUCTION
PROJECT - TAGMA CENTRE
SITE - CHAKAN
DWG. NO. : NIHVA/17-18/0130
SCALE: NTS | WT: | SHEET: 01 OF 01