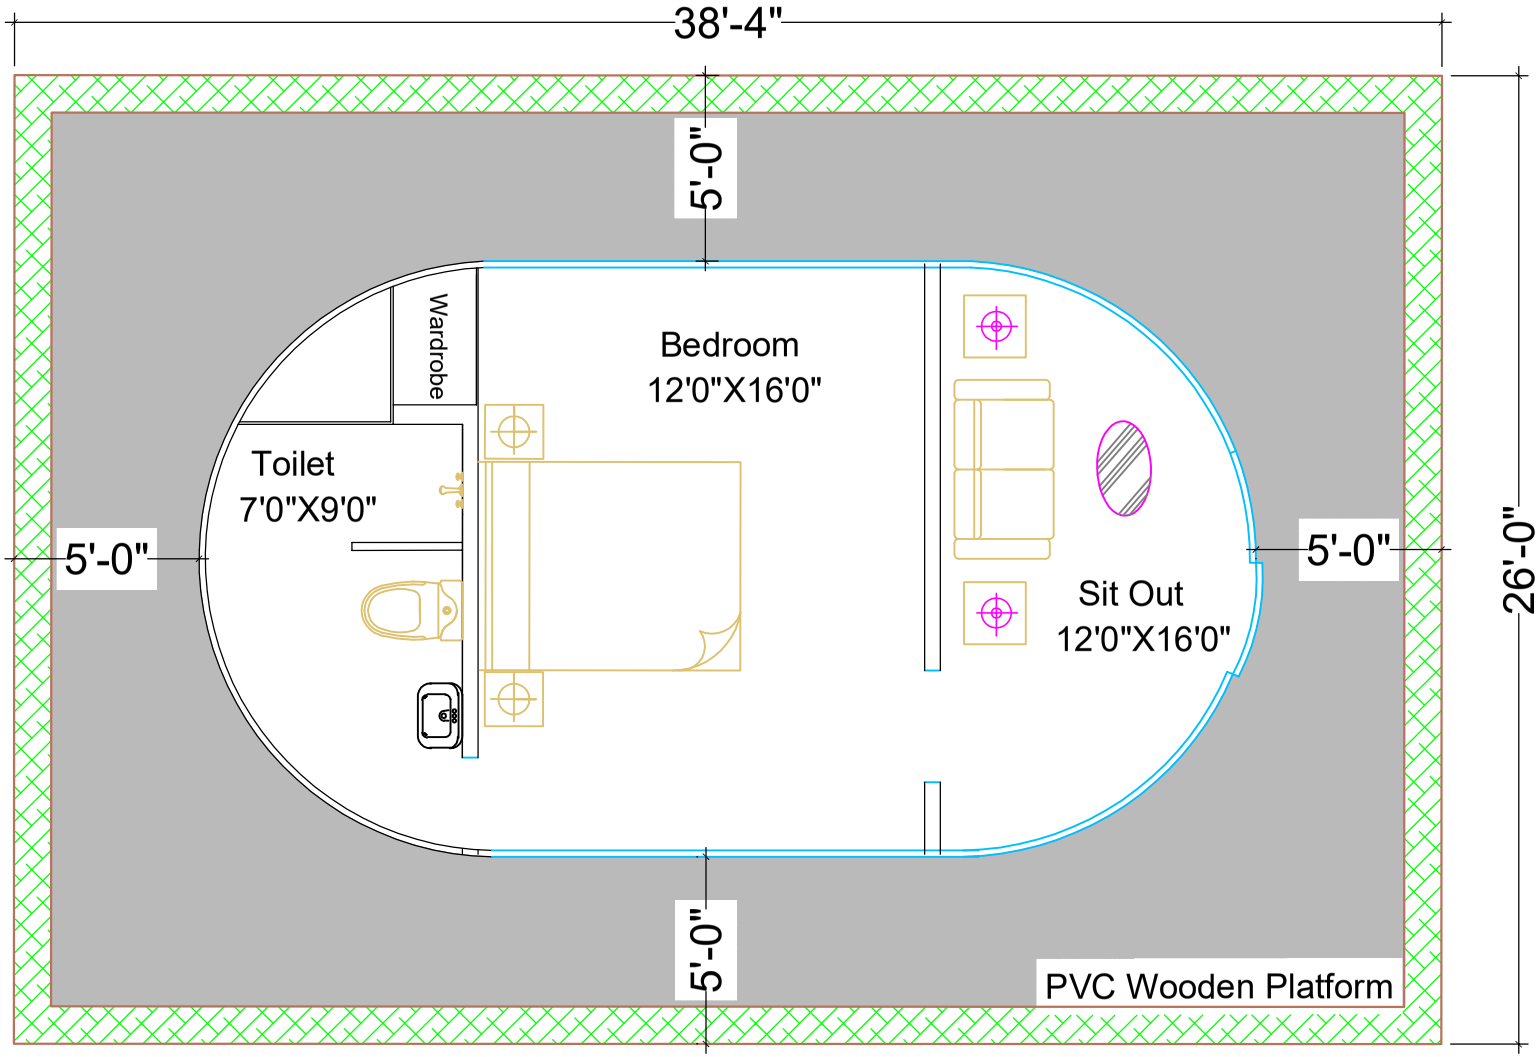


REV.	DESCRIPTION	DATE	BY
△			
△			
△			

NOTES:–

1. ALL DIMENSIONS AND LEVELS ARE IN FEET & FIGURED DIMENSIONS SHALL BE FOLLOWED.
2. ±0.00 LEVEL CORRESPONDS TO PLINTH LEVEL(P.L.) WHICH IS 1050mm IN ABSOLUTE GROUND LEVEL(G.L.).
3. ALL RCC WORK SHALL BE OF M25 GRADE CONCRETE.
4. BRICKWORK SHALL BE WITH 100A BRICKS IN CEMENT MORTAR 1:6.

PROJECT	PROPOSED DEVELOPMENT OF MAJHAR KUND SASARAM
DEPT.	ENVIRONMENT AND FOREST DEPARTMENT SASARAM RANGE, ROHTAS DIVISION
CONSULT.	SHAMAR STRUCTURE SOLUTIONS PVT. LTD. PATNA

CHECKED & APPROVED		Polycarbonate Dome House	
DESIGN BY	PRIYANKA		
DRAWN BY	KUNDAN		
SIZE-A3	SCALE 1:100	DATE - 10.05.2024	SHEET 15 / REV R=0