


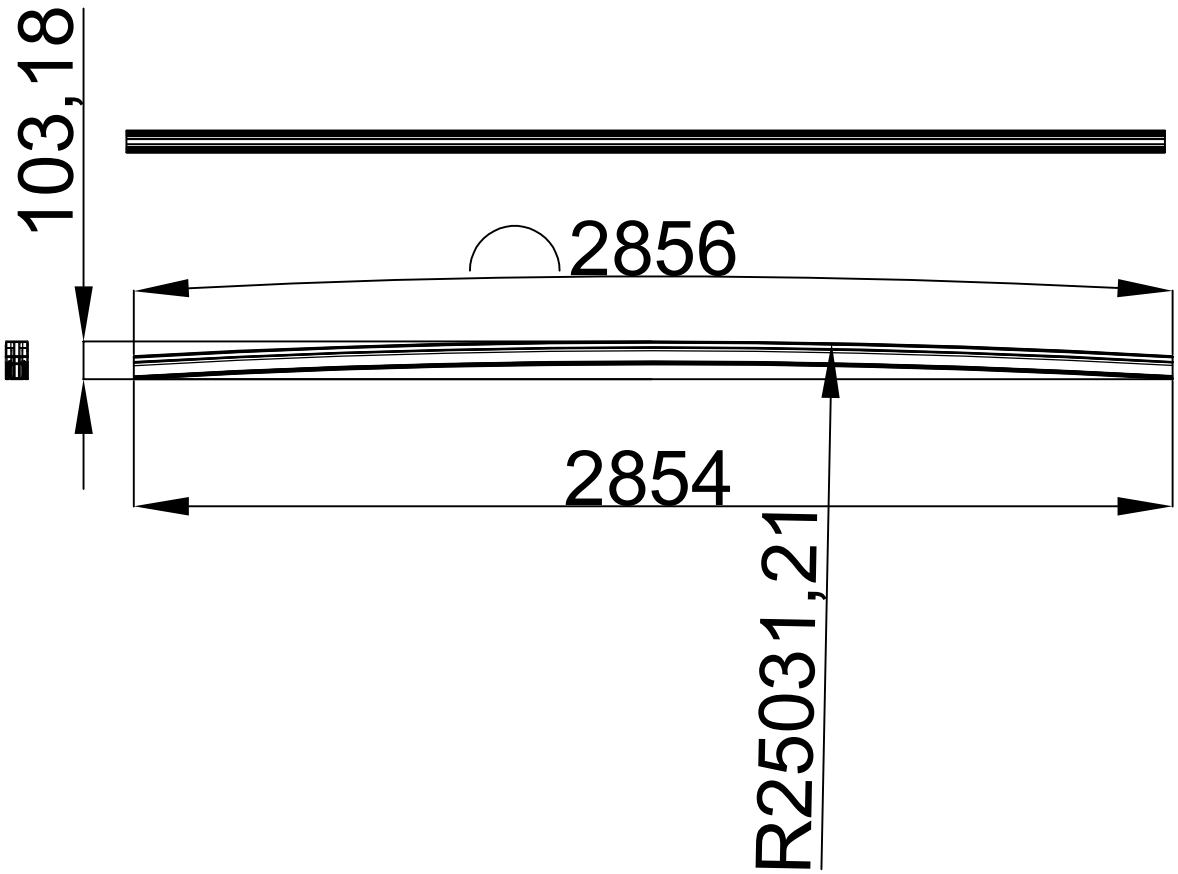

PROFILE-02 -02
MATL-ALUMINIUM
QTY-01
DRG NO-01-16

REV NO.	DESCRIPTION	Date	Revised By

TITLE:- BEND PROFILE -02

NIHVA TECHNOLOGIES PVT. LTD.

NIHVA TECHNOLOGIES PVT. LTD. PUNE
Tel : 020 66304033
Email:- info@nihva.com
Website:- www.nihva.com

	NAME	DATE	SIGN
DRAWN	KISHAN	27/07/22	
CHECK	M. SUTAR	27/07/22	
APPRD.	V. TARAK	27/07/22	

If any queries contact : design@nihva.com

ALL DIMENSION ARE IN mm

CLIENT - NIHVA TECHNOLOGIES PVT.LTD
LOCATION -
PRODUCT: RETRACTABLE ROOF
DWG NO:-NIHVA/22-23/MFG/0048 | REV- 0
SCALE: NTS | SCALE:-- 1:1 | SHEET: 01 OF 01