
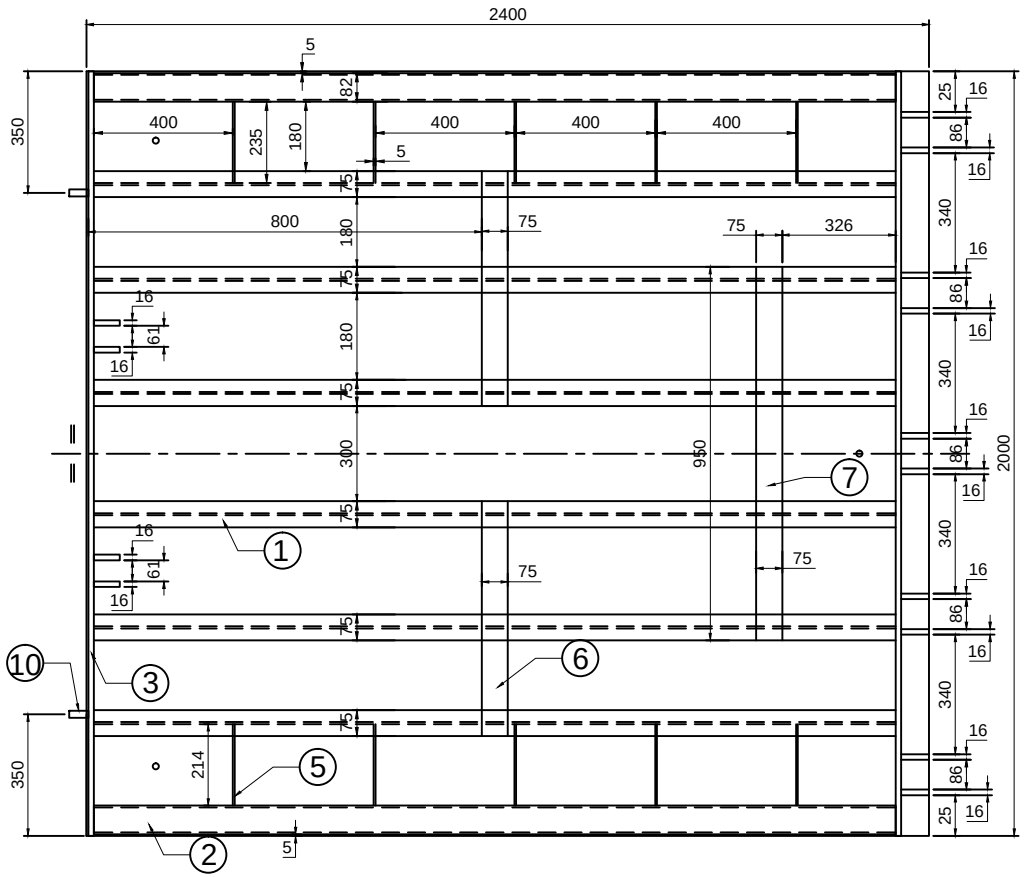


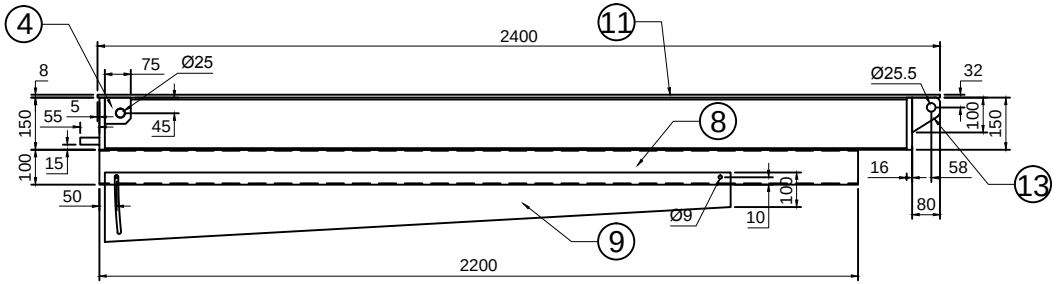

NOTE:~ MTL : MS

PART NO.	PART NAME	DESCRIPTION	QTY
1.	ISMB	150 X 75 X 2283L	6 NOS
2.	R.TUBE	145 X 82 X 5.4THK X 2283L	2 NOS
3.	FLAT	150 X 16 X 2000L	2 NOS
4.	PROFILE	75 X 16 X 75L	4 NOS
5.	FLAT	150 X 6 X 210L	10 NOS
6.	FLAT	75 X 6 X 580L	2 NOS
7.	FLAT	75 X 6 X 950L	1 NO
8.	BEND	100 X 3THK X 2200L	2 NOS
9.	SIDE COVER	275 X 3THK X 1950L	2 NOS
10.	LIP STOPER	Ø20 X 55L	4 NOS
11.	CHEQ.SHEET	2000 X 8 THK X 2400L	1 NO
12.	EYE BOLT	M16 WITH TAPPING PLATE	3 NOS
13.	PROFILE	80 X 16 X 100L	10 NOS

This drawing & design is the property of NIHVA TECHNOLOGIES. Not to be sold or copied to any other concern.

TITLE

DECK ASSLY

	NAME	SIGN	DATE
DRAWN	P.A		10.01.2020
CHECK	G.J		10.01.2020
APPRD.			

If any queries contact : design@nihva.com

ALL DIMENSION ARE IN mm

NIHVA TECHNOLOGIES PVT. LTD.

NIHVA TECHNOLOGIES PVT. LTD. PUNE
Tel : 020 66304033
Email:- info@nihva.com
Website:- www.nihva.com

CLIENT -

PROJECT -

SITE LOCATION -

DWG. NO. : NIHVA/19-20/VDR/280

SCALE: NTS | WT: | REV- 00