
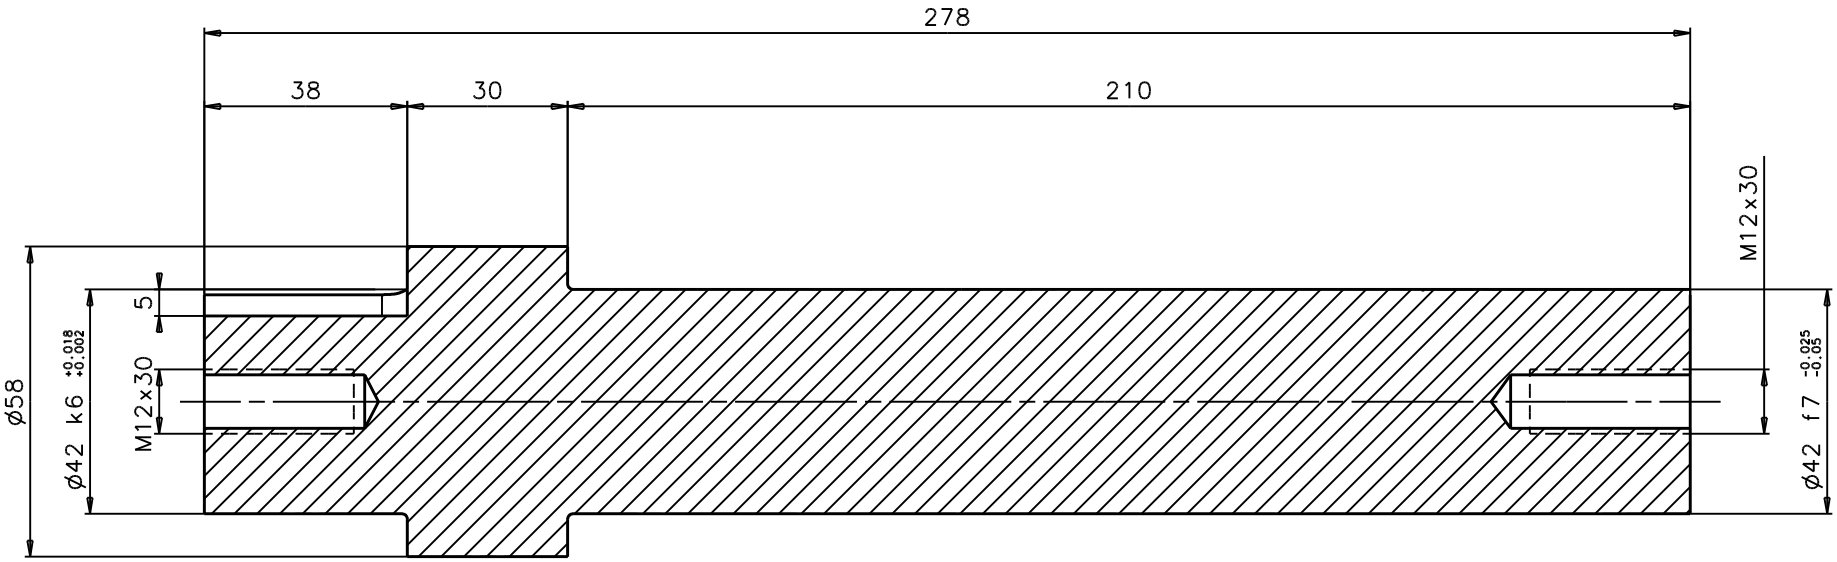


SEZ. A-A

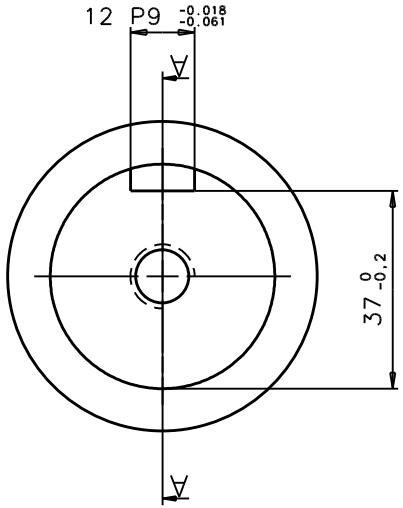

3.2

Smussi n.q. 1x45°
Raccordi n.q. R 0.5-1

INDICE MODIFICA	DESCRIZIONE MODIFICA	FIRMA	DATA
			XX

PMP PRO-MEC
PRODUZIONE MECCANICA DI QUALITA'
PRO-MEC SRL
33030 COSEANO (UD) - Via dell'Industria -Z.I. S. Andrea
Tel. 0432.861313 - Fax 0432.861333

DATA	DISEGNATO	CONTROLLATO	APPROVATO	MASSA
03/02/03	Sant I.	Pozzo L.		0.0 kg

DESCRIZIONE: ALBERO RIDUTTORE
BANCO RIBALTAMENTO PMB

MATERIALE: 39NiCrMo5

RIVESTIMENTO SUPERFICIALE

TRATTAMENTO TERMICO FINALE

PROFONDITA' TRATT. TERMICO

RESISTENZA

DUREZZA

SCALA 1/1 | FORMATO A3

SOSTIT.

DIS. GRZZO N.

DISEGNO N. -ATP.0246

SCOSTAMENTI LIMITE PER DIMENSIONI DI PARTI LAVORATE SENZA INDICAZIONI A DISEGNO (RIF. UNI EN 22768/1)

>	0	3	6	30	120	400	1000	2000
≤	3	6	30	120	400	1000	2000	4000
+/-	0.1	0.1	0.2	0.3	0.5	0.8	1.2	2.0

SCOSTAMENTI LIMITE PER DIMENSIONI ANGOLARI (RIF. UNI EN 22768/1)

>	0	10	50	120	400
≤	10	50	120	400	---
+/-	1°	0°30'	0°20'	0°10'	0°5'

TOLLERANZA DI FORMA O POSIZIONE: UNI 7226

LA PROPRIETA' DI QUESTO DISEGNO E' TUTELATA A TERMINI DI LEGGE. E' VIETATO RIPRODURLO E/O CEDERLO A TERZI SENZA LA NOSTRA AUTORIZZAZIONE SCRITTA