

DRAWING

REV DESCRIPTION	DATE	REV NO
	17-06-2026	REV 00
1. ROOF ORIENTATION CHANGES. ROOF SLINDING DIRECTION CHANGES	22-06-2026	REV 01

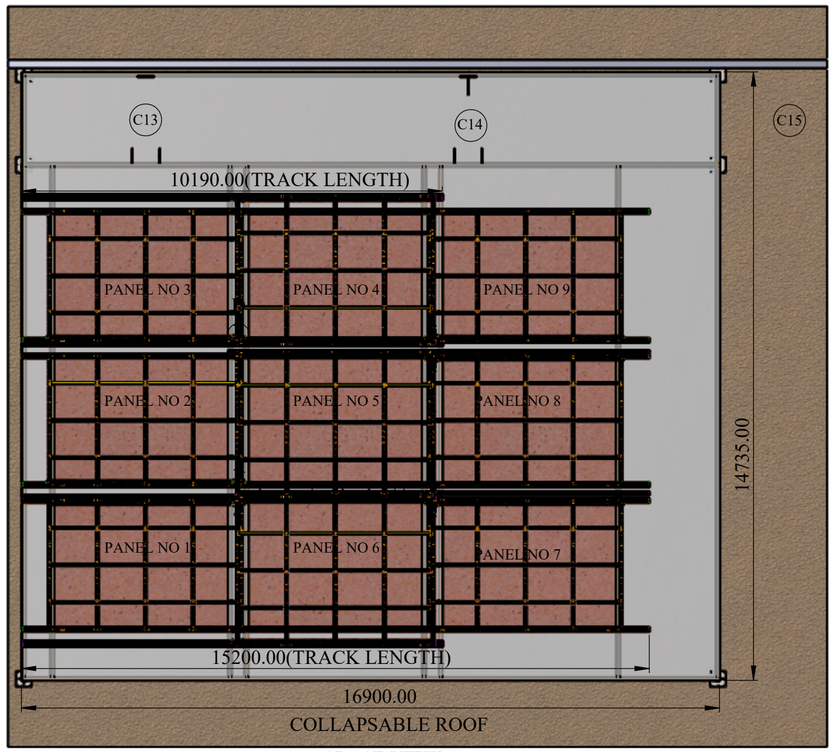


CLOSE VIEW

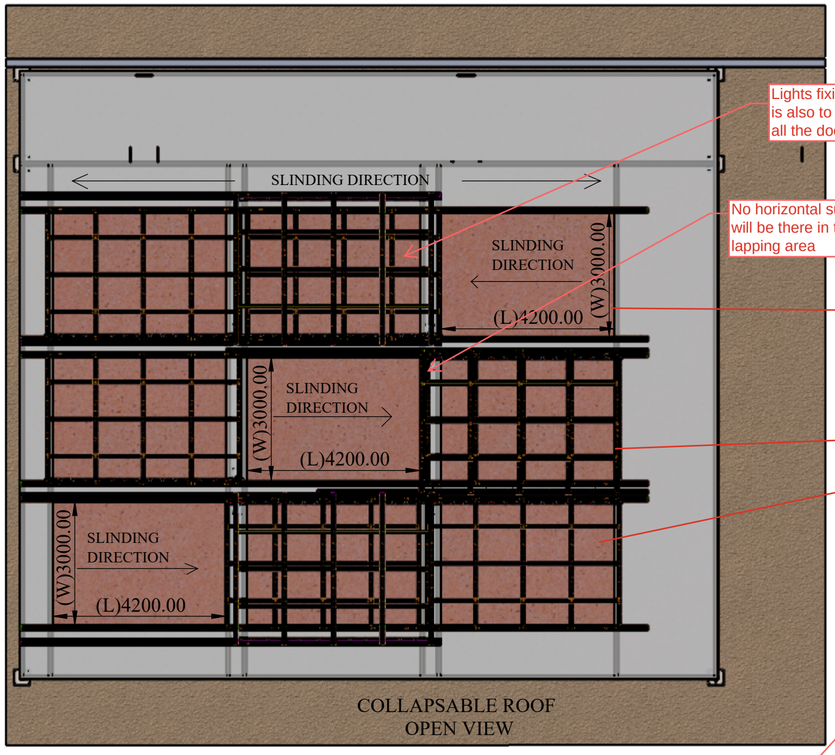



Lights fixing provision is also to be done for all the doors


No horizontal support will be there in the door lapping area

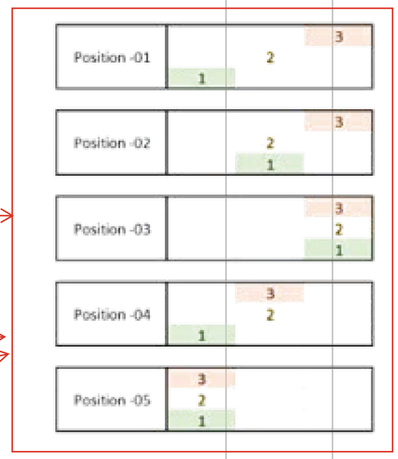

Check this Area in this area 3 layers off room will be there for our operation but it was shown only 2 nos

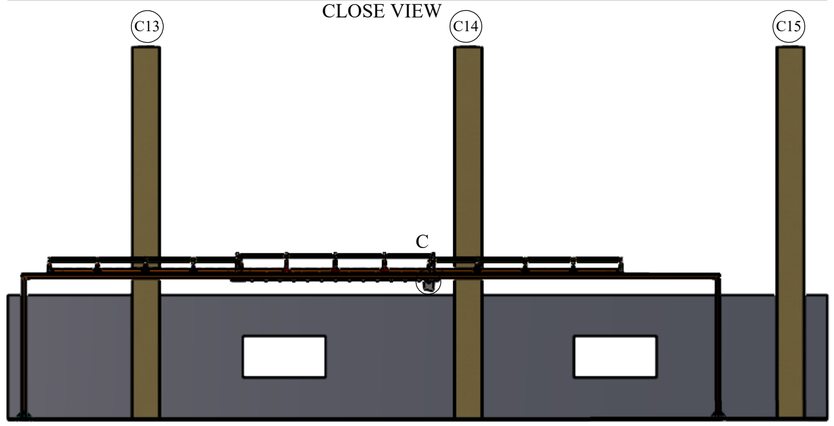

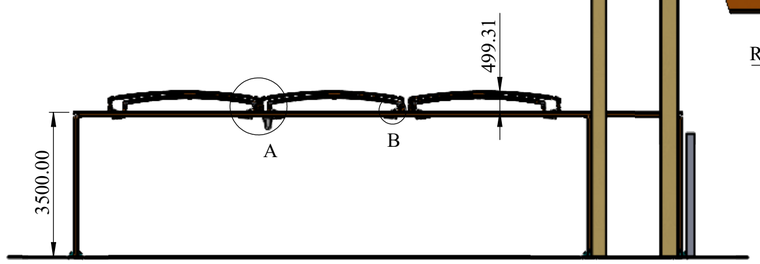

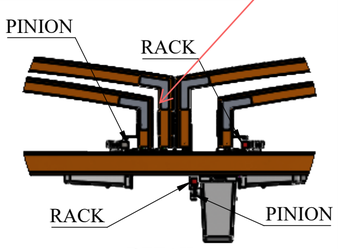


DETAIL A
SCALE 1 : 20
MOTOR ARRANGEMENT


SLINDING DIRECTION



DETAIL D
SCALE 1 : 15

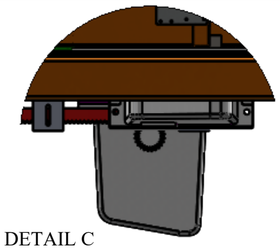

DETAIL C
SCALE 1 : 10

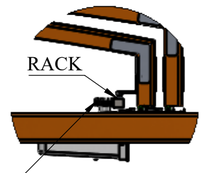

DETAIL B
SCALE 1 : 15
MOTOR ARRANGEMENT

NOTE :

THIS DRAWING IS FOR CLIENT APPROVAL
BASE STRUCTURE IN CLIENT SCOPE

SPECIAL INSTRUCTION'S :

This drawing & design is the property of NIHVA TECHONOLOGIES PVT. LTD. Not to be sold or copied to any other concern

TITLE - COLLAPSABLE CCA ROOF

DWG NO - NTPL-401-PM-04


NIHVA TECHNOLOGIES PVT.LTD.PUNE
Website - www.nihva.com

	NAME	SIGNATURE	DATE
DRAWN	V.W.		17-06-2026
CHK'D	S.P.		18-06-2026
APPV'D	V.T.		18-06-2026

PRODUCT - RETRACTABLE ROOF
CLIENT NAME - NEOTRAFO SOLUTIONS
SITE LOCATION - HYDRABAD
MATRIAL - QTY - 1
If any queries contact - info@nihva.com
PROJECTION METHOD:
SCALE :
ALL DIMENSION ARE IN mm A2
SHEET 1 OF 2

DRAWING


REV DESCRIPTION	DATE	REV NO
	17-06-2026	REV 00
1.		

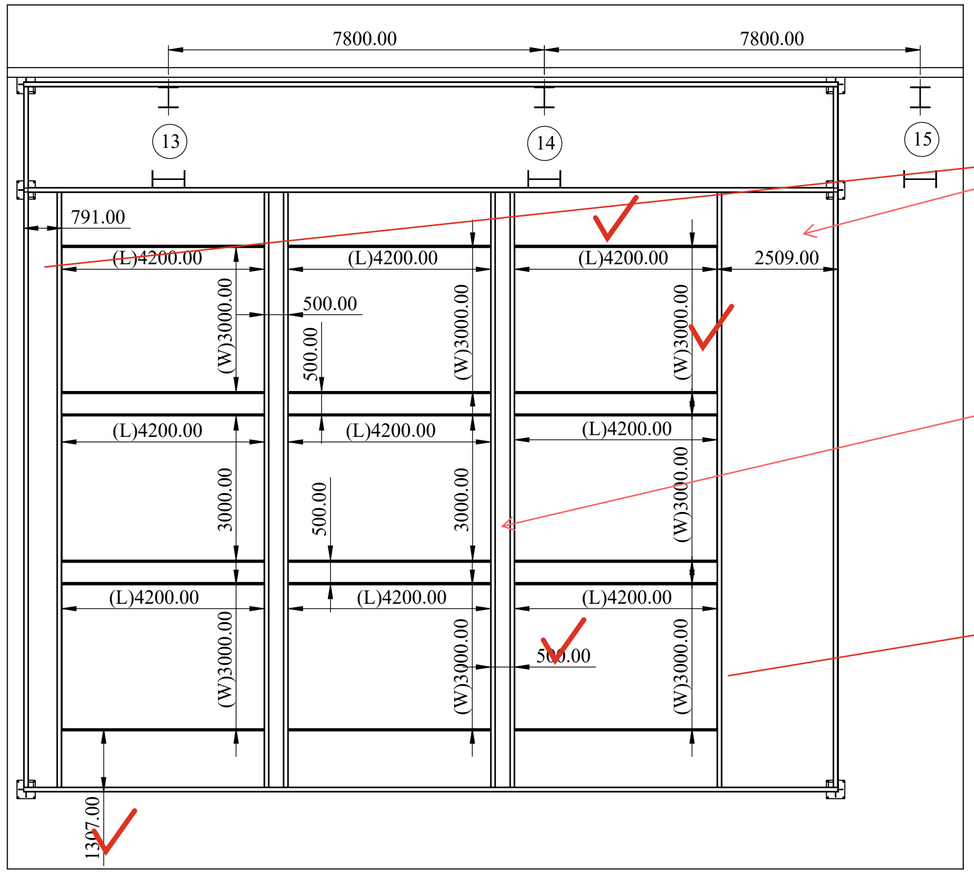


(2509+791)/2

position this doors in Room center

No horizontal support will be there in the door lapping area

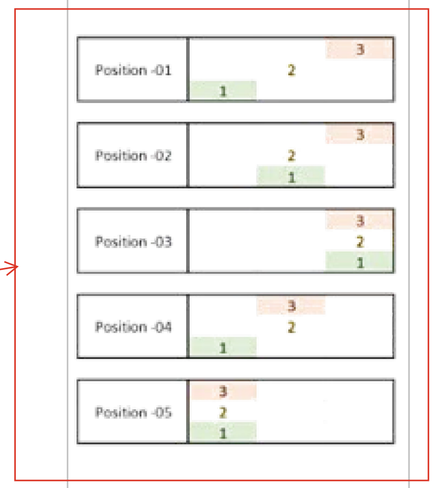

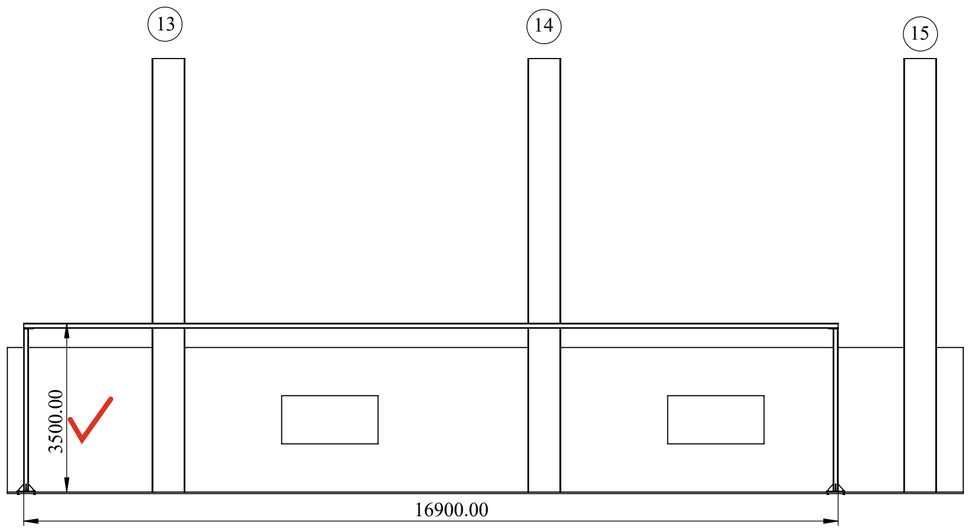

NOTE :

BASE STRUCTURE IN CLIENT SCOPE

SPECIAL INSTRUCTION'S :

This drawing & design is the property of NIHVA TECHONOLOGIES PVT. LTD. Not to be sold or copied to any other concern

TITLE - COLLAPSABLE CCA ROOF

DWG NO - NTPL-401-PM-04

NIHVA Technologies Pvt. Ltd.

NIHVA TECHNOLOGIES PVT.LTD.PUNE
Website - www.nihva.com

	NAME	SIGNATURE	DATE
DRAWN	V.W.		17-06-2026
CHK'D	S.P.		18-06-2026
APPV'D	V.T.		18-06-2026

PRODUCT - RETRACTABLE ROOF

CLIENT NAME - NEOTRAFO SOLUTIONS

SITE LOCATION - HYDRABAD

MATRIAL -

QTY - 1

If any queries contact - info@nihva.com

ALL DIMENSION ARE IN mm

A2

PROJECTION METHOD:

SCALE :