
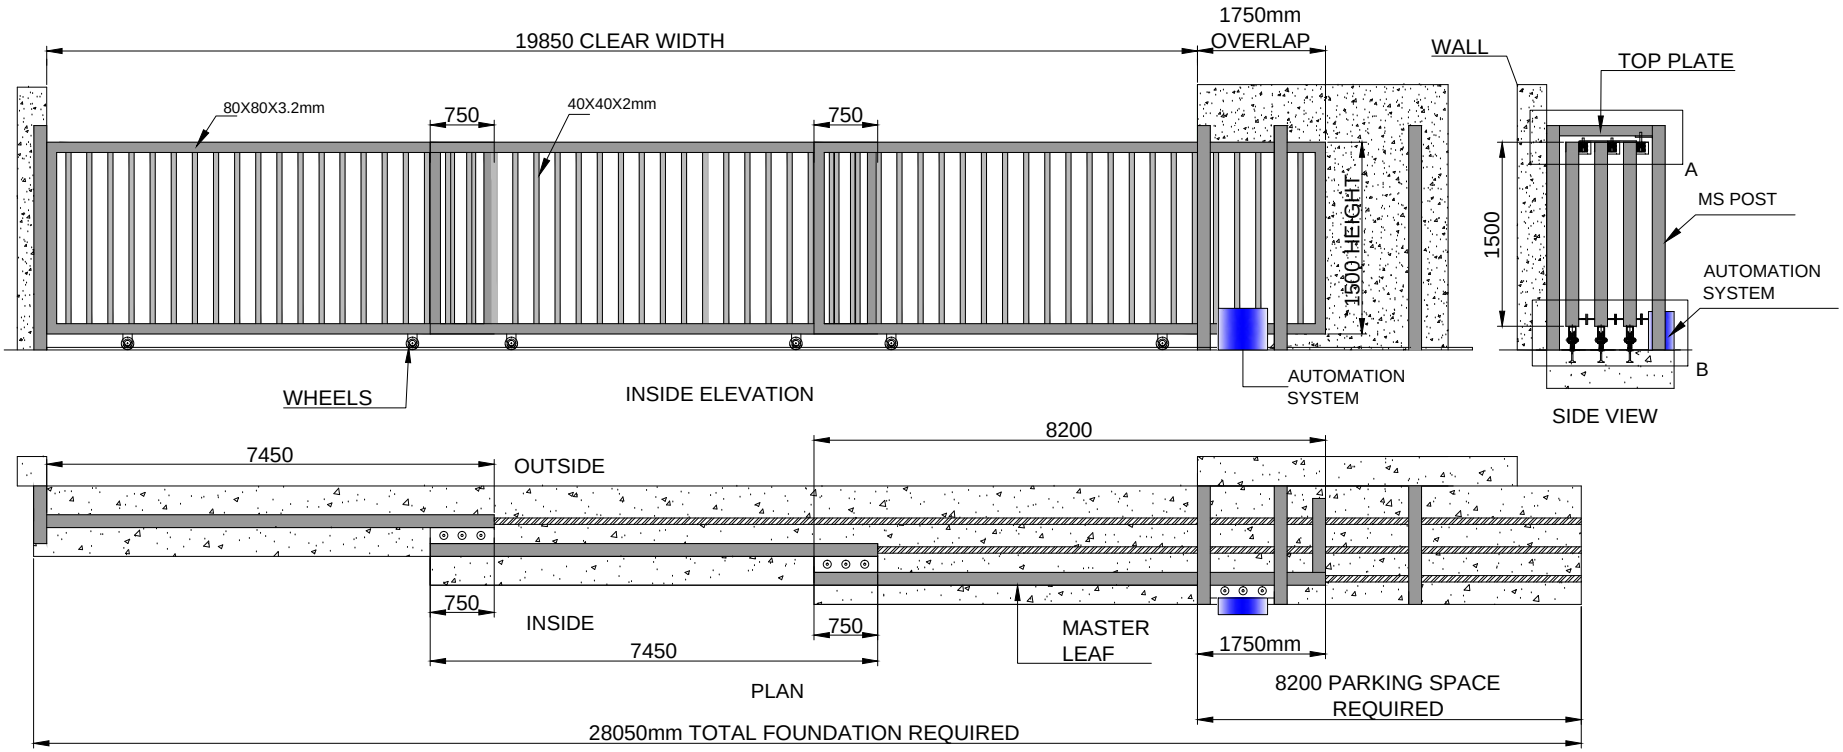


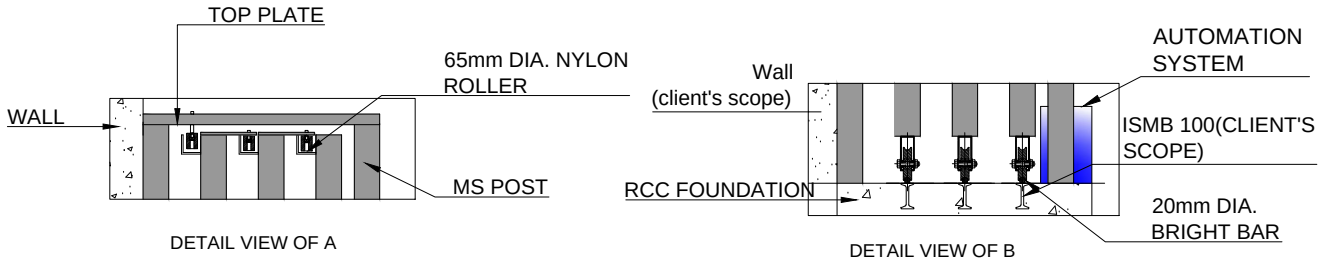

NOTE-
1. ALL REQUIRED CIVIL WORK WILL BE IN CLIENTS SCOPE.
2. ONE COAT OF RED OXIDE & TWO COAT OF APPROVED RAL SHADE WILL BE GIVEN TO THE GATE.
3.IF NECESSARY GATE LEAF WILL BE IN TWO PARTS FOR TRANSPORTATION & WILL BE WELD TOGETHER ON SITE.

GATE WIDTH	GATE HEIGHT	QUANTITY	LOCATION
19850mm	1500mm	1 NOS	- - - - -

This drawing & design is the property of NIHVA TECHNOLOGIES. Not to be sold or copied to any other concern.

TITLE
AUTOMATIC THREE LEAF TELESCOPIC GATE

	NAME	SIGN	DATE
DRAWN	SURAJ		19/12/17
CHECK	OMKAR		19/12/17
APPV'ED	SHEKHAR		19/12/17

If any queries contact : design@nihva.com

ALL DIMENSION ARE IN mm

NIHVA TECHNOLOGIES PVT. LTD.
NIHVA TECHNOLOGIES PVT. LTD. PUNE
Tel : 020 66304033
Email:- info@nihva.com
Website:- www.nihva.com

CLIENT - SUROJ BUILDCON
PROJECT - EMBASSY INDUSTRIAL PARKS PVT LTD.
SITE LOCATION - CHAKAN,PUNE.
DWG. NO. : NIHVA/17-18/0319 REV. :- 0
SCALE: NTS WT: SHEET: 01 OF 01