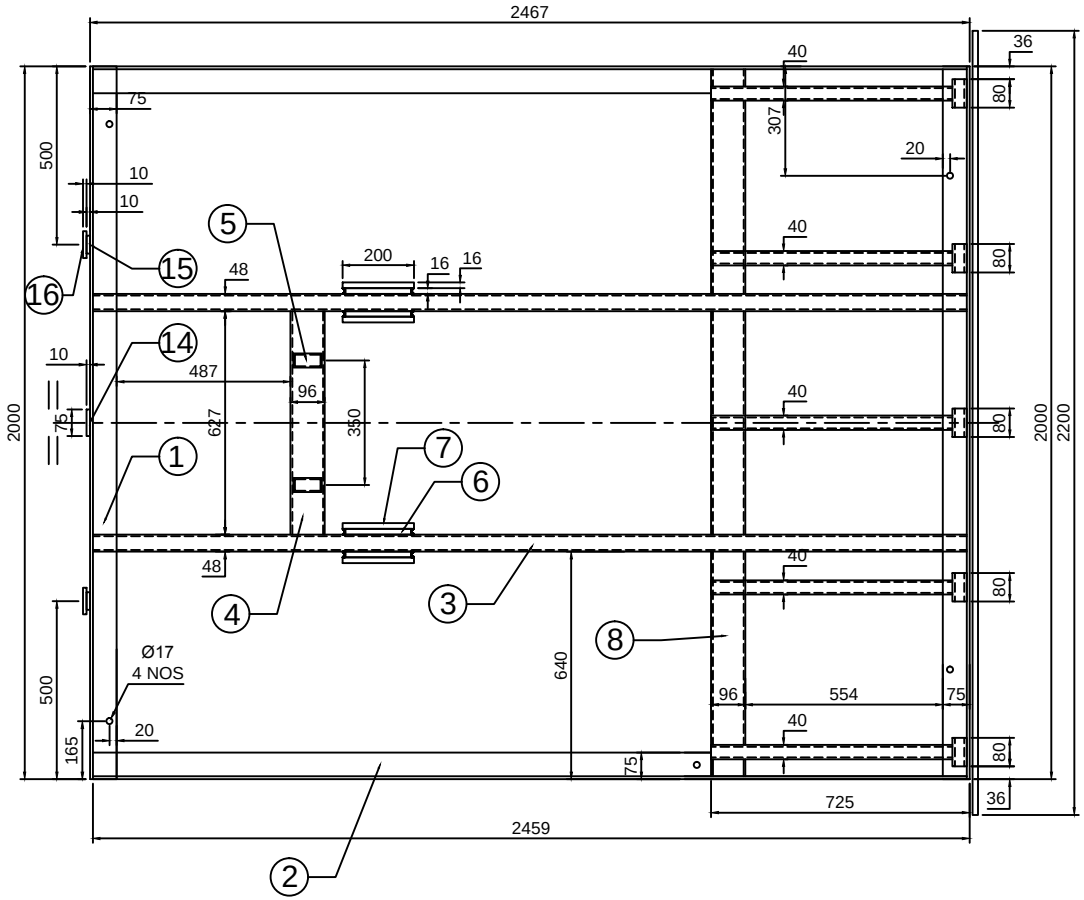
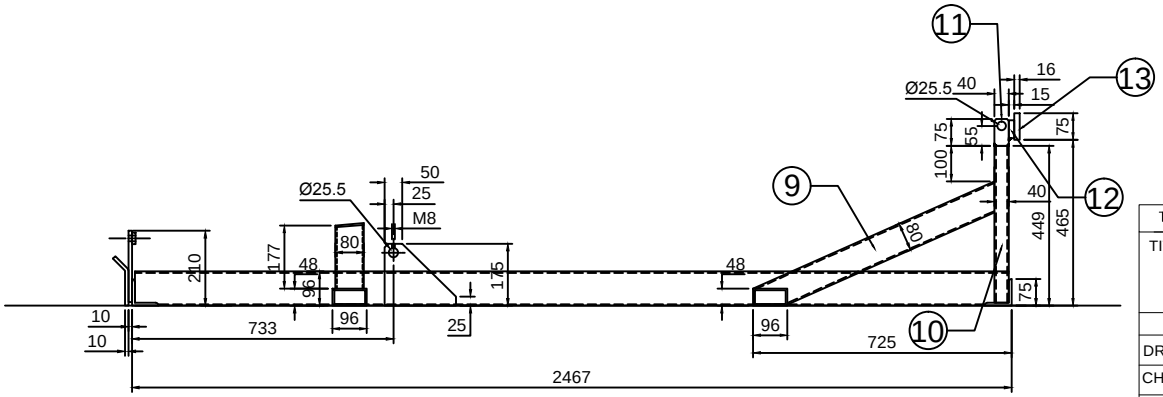



NOTE:~ MTL : MS

| PART NO. | PART NAME | DESCRIPTION | QTY |
|---|---|---|---|
| 1. | ISA | 75 X 75 X 8 X 2000L | 2 NOS |
| 2. | ISA | 75 X 75 X 8 X 2450L ( NOTCH ) | 2 NOS |
| 3. | R.TUBE | 96 X 48 X 4.8 THK X 2450L ( NOTCH ) | 2 NOS |
| 4. | R.TUBE | 96 X 48 X 4.8 THK X 625L | 2 NOS |
| 5. | R.TUBE | 80 X 40 X 4 THK X 180L | 2 NOS |
| 6. | FLAT | 80 X 16 X 180L | 4 NOS |
| 7. | FLAT | 175 X 16 X 200L | 4 NOS |
| 8. | R.TUBE | 96 X 48 X 4.8 THK X 630L ( NOTCH ) | 2 NOS |
| 9. | R.TUBE | 80 X 40 X 4 THK X 740L ( NOTCH ) | 5 NOS |
| 10. | R.TUBE | 80 X 40 X 4 THK X 440L | 5 NOS |
| 11. | SOLID | 75 X 40 X 100L | 5 NOS |
| 12. | FLAT | 50 X 16 X 70L | 5 NOS |
| 13. | FLAT | 75 X 16 X 2200L | 1 NO |
| 14. | FLAT | 75 X 10 X 210L | 1 NO |
| 15. | FLAT | 50 X 10 X 75L | 2 NOS |
| 16. | FLAT | 75 X 10 X 150L | 2 NOS |

This drawing & design is the property of NIHVA TECHNOLOGIES. Not to be sold or copied to any other concern.

TITLE

BASE FRAME ASSLY

NIHVA TECHNOLOGIES PVT. LTD.

NIHVA TECHNOLOGIES PVT. LTD. PUNE
Tel : 020 66304033
Email:- info@nihva.com
Website:- www.nihva.com

| | NAME | SIGN | DATE |
|---|---|---|---|
| DRAWN | P.V.A | | 07.08.2019 |
| CHECK | V.M.T | | 07.08.2019 |
| APPRD. | | | 07.08.2019 |

CLIENT -

PROJECT - DLIK1005

SITE LOCATION -

If any queries contact : design@nihva.com

DWG. NO. : NIHVA/19-20/VDR/125

ALL DIMENSION ARE IN mm

SCALE: NTS | WT: | REV- 00