



DWG.NO: SALT_1729_STR_11_R0

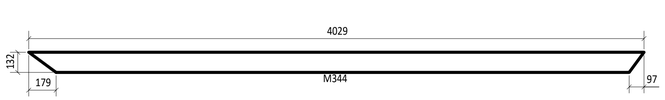


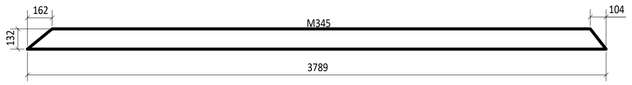


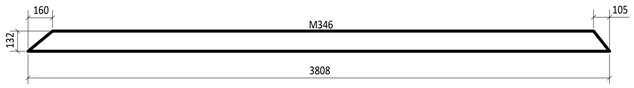




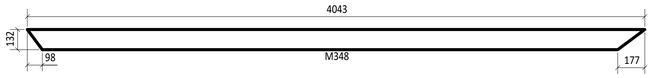


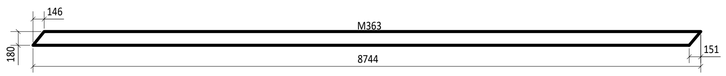


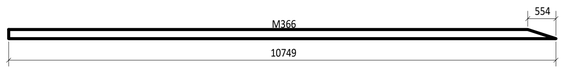





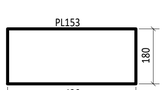


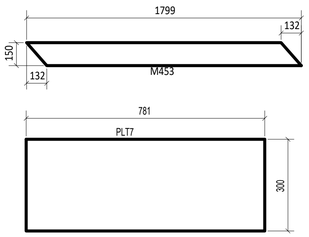


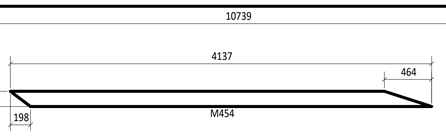


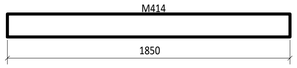

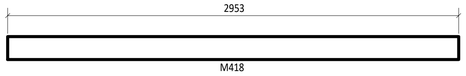


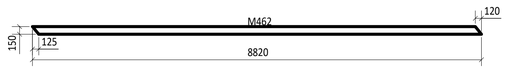


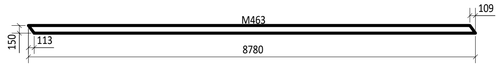

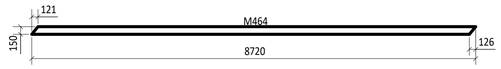



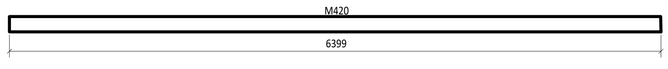


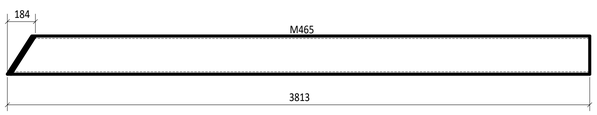










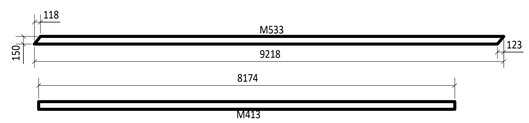


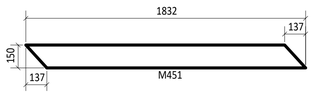


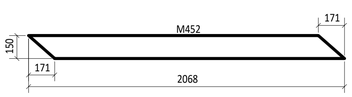


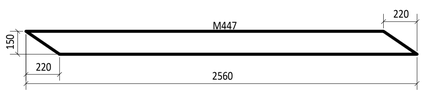




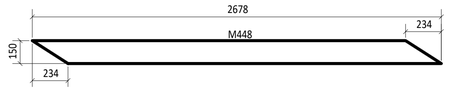


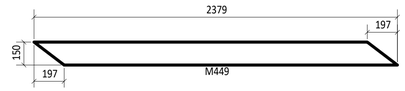


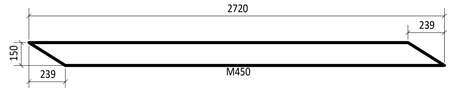


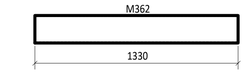





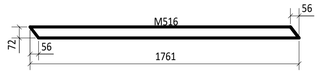

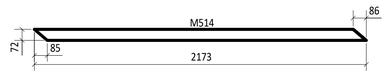


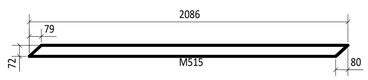


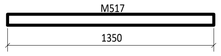


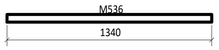





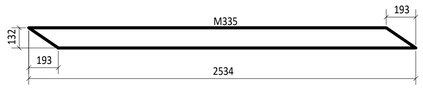


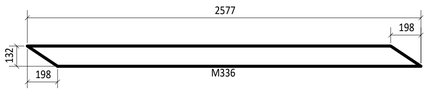


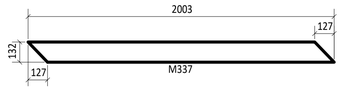


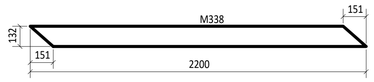


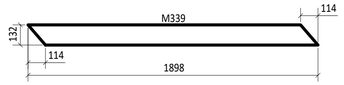


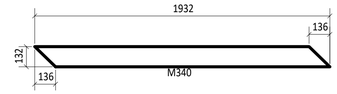

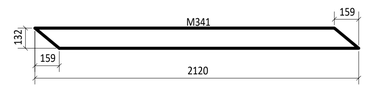


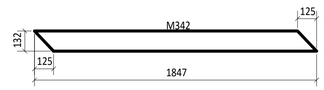


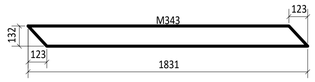


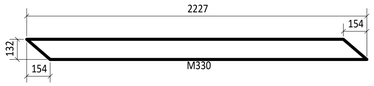





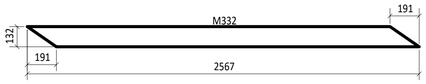


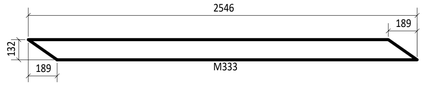


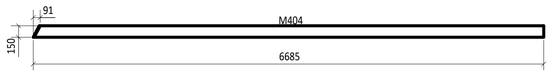


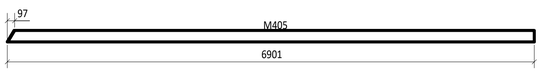


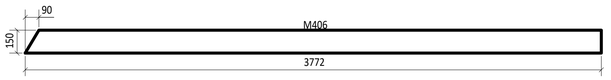

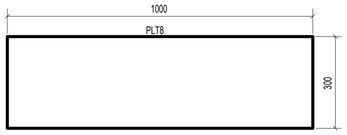


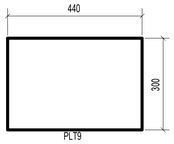


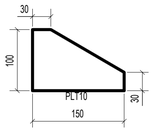


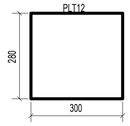





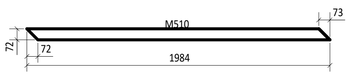


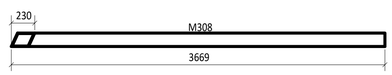


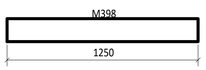

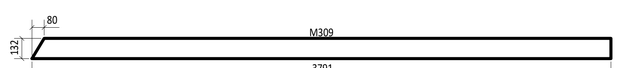


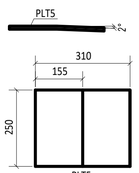


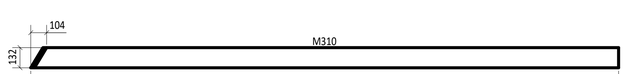


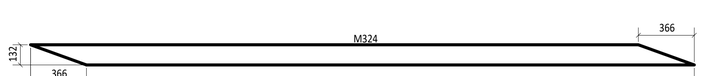





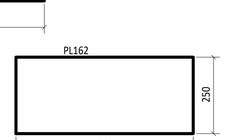

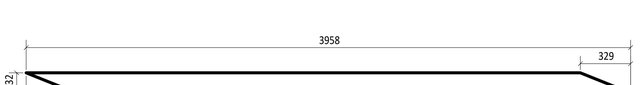

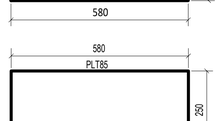


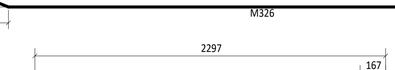


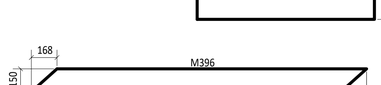








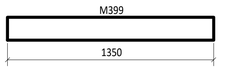

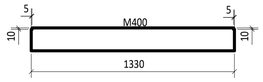

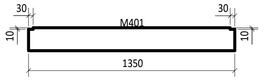

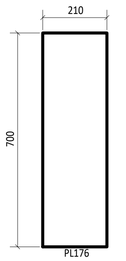

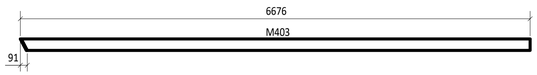

0	DRAWING FOR APPROVAL	29.12.22	AAK	HAB	HAB
REV.NO.	DESCRIPTION.	REV.DATE	DRAWN.	CHKD.	APPD.

DWG.TITLE :- CUTTING DETAILS MTO FOR 84.00M TRUSS

PROJECT	MEGADOOR INSTALLATION AT HYDRABAD AIRPORT
CLIENT	GMR

SALT Design Services
NIHVA NIHVA TECHNOLOGIES PVT. LTD.
SALT DESIGN SERVICES
NIHVA TECHNOLOGIES PVT. LTD. PUNE
Tel : 020 66304033
Email:- info@nihva.com
Website:- www.nihva.com

DRAWN :AAK	CHECKED : HAB	SCALE: 1:100
APPROVED : HAB	JOB CODE. : 1729	DATE: 29.12.2022
DWG.NO: SALT_1729_STR_11_R0	(SH-1OF1)	REV. - R0
		SIZE. - A0

A1 [841 x 594]