



DRAWING

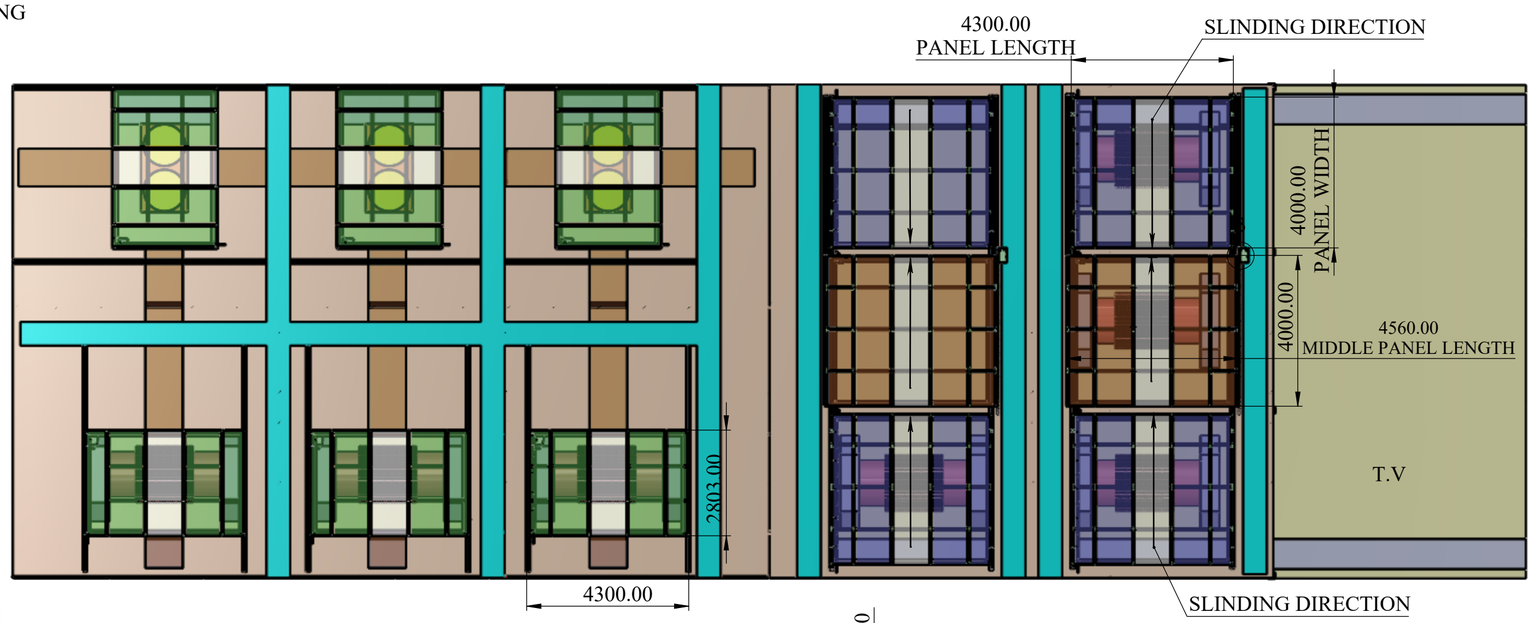

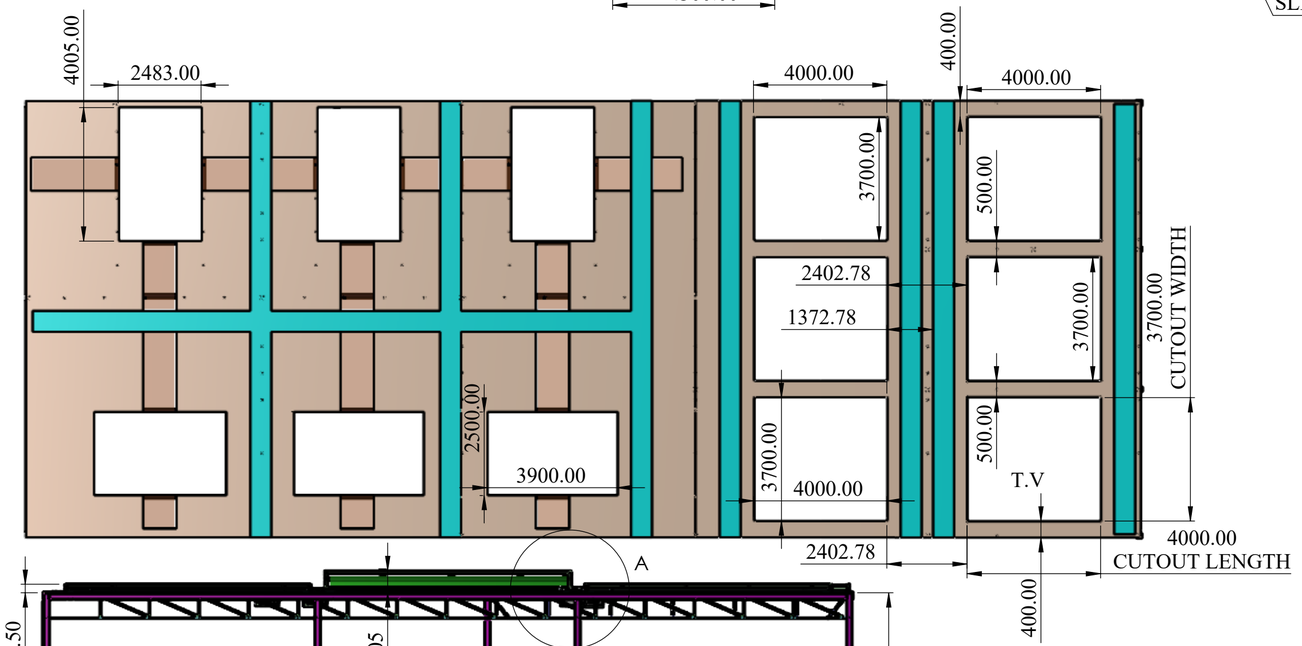


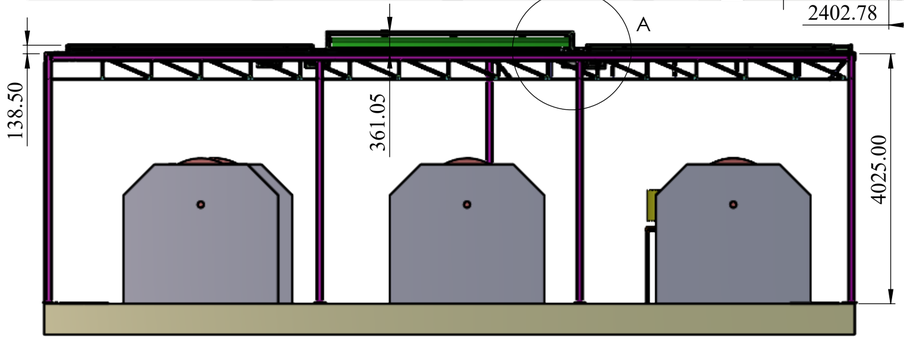

F.V

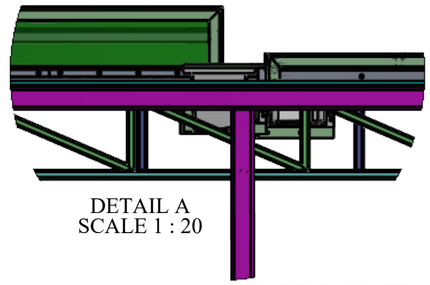

DETAIL A
SCALE 1 : 20

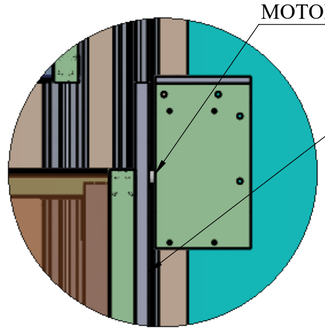


DETAIL B
SCALE 1 : 10

MIDDLE PANEL MOTOR &
RACK ARRANGMRNT

| REV DESCRIPTION | DATE | REV NO |
|---|---|---|
| 03. AIR TIGHTENING & DUST PROOF RUBBERIS ADDED | 00-00-2025 | REV 03 |
| 04. PANEL MODIFICATION | 10-07-2025 | REV 04 |
| 05. SAME UNIT ANTHOER THREE PANEL MODIFICATION | 15-07-2025 | REV 05 |

NOTE :

SPECIAL INSTRUCTION'S :

TITLE - ROOF AUTOMATION

DWG NO - NTPL-244-PM-001-00-00-00

NIHVA Technologies Pvt. Ltd.

NIHVA TECHNOLOGIES PVT.LTD.PUNE
Website - www.nihva.com

| | NAME | SIGNATURE | DATE |
|---|---|---|---|
| DRAWN | V.W. | | 14-07-2025 |
| CHK'D | S.W. | | 15-07-2025 |
| APPV'D | V.T. | | 15-07-2025 |

PRODUCT - RETRACTABLE ROOF

PROJECT NO - NTPL-244-PM | REVISION - 05

SITE LOCATION -AHMADABAD | WEIGHT -

MATRIAL - | QTY - 1

If any queries contact - design.nihva@gmail.com

ALL DIMENSION ARE IN mm | A2


PROJECTION METHOD:


SCALE :

SHEET 1 OF 16

DRAWING

| REV DESCRIPTION | DATE | REV NO |
|---|---|---|
| | 15-07-2025 | REV 05 |
| 1. | | |

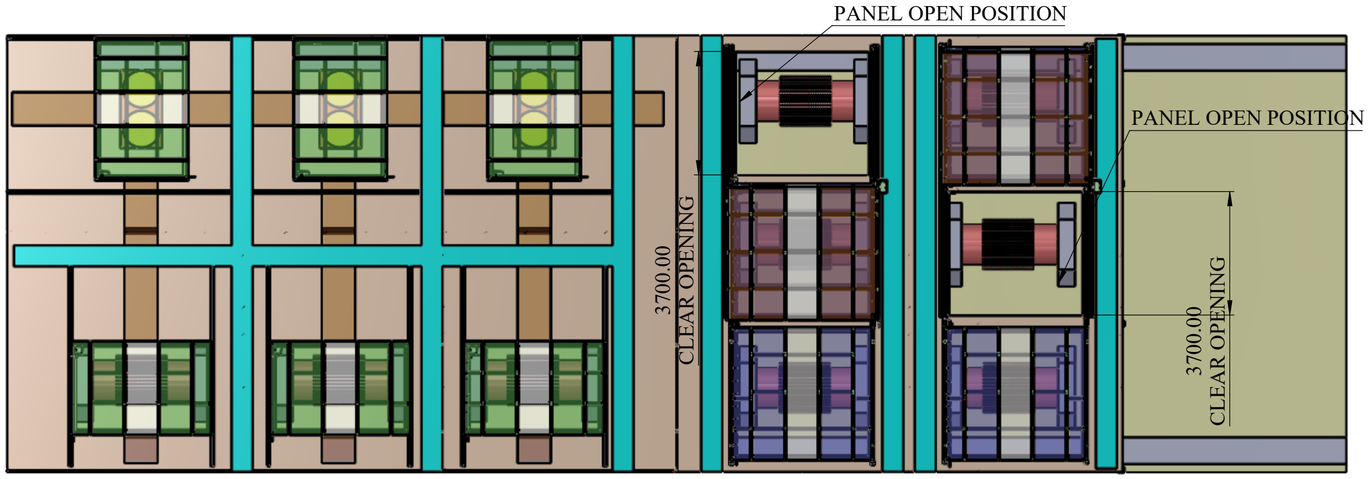

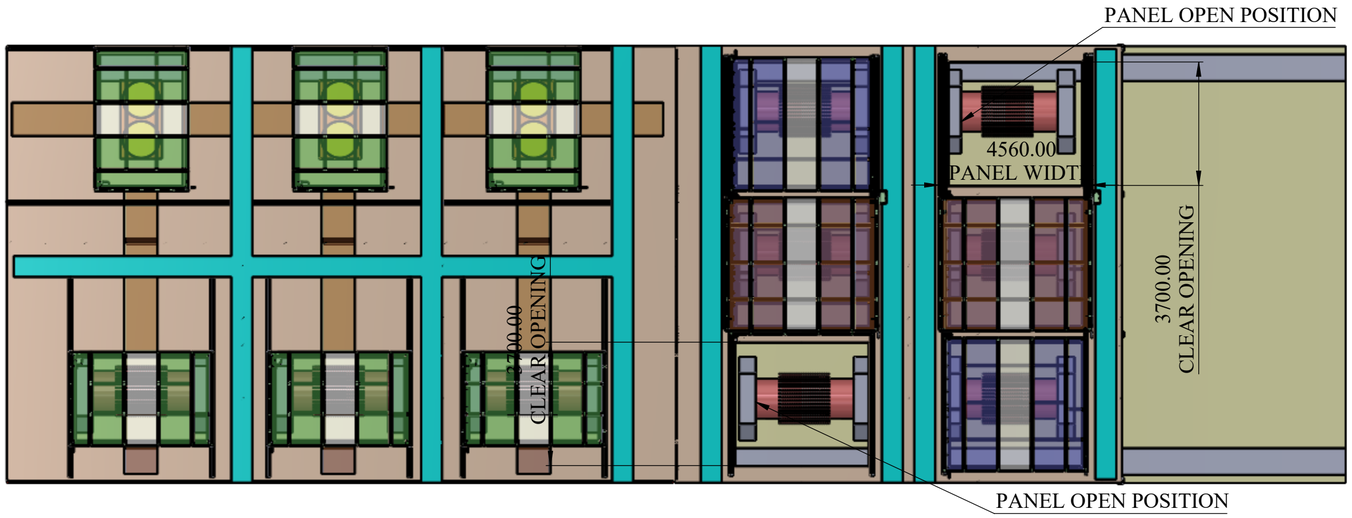
NOTE :

SPECIAL INSTRUCTION'S :

TITLE - ROOF AUTOMATION

DWG NO - NTPL-244-PM-001-00-00-00

NIHVA TECHNOLOGIES PVT.LTD.PUNE
Website - www.nihva.com

| | NAME | SIGNATURE | DATE |
|---|---|---|---|
| DRAWN | V.W. | | 14-07-2025 |
| CHK'D | S.W. | | 15-07-2025 |
| APPV'D | V.T. | | 15-07-2025 |

PRODUCT - RETRACTABLE ROOF

PROJECT NO - NTPL-244-PM | REVISION - 05

SITE LOCATION - | WEIGHT -

MATRIAL - | QTY - 1


If any queries contact - design.nihva@gmail.com


ALL DIMENSION ARE IN mm | A2


PROJECTION METHOD:

SCALE :

DRAWING

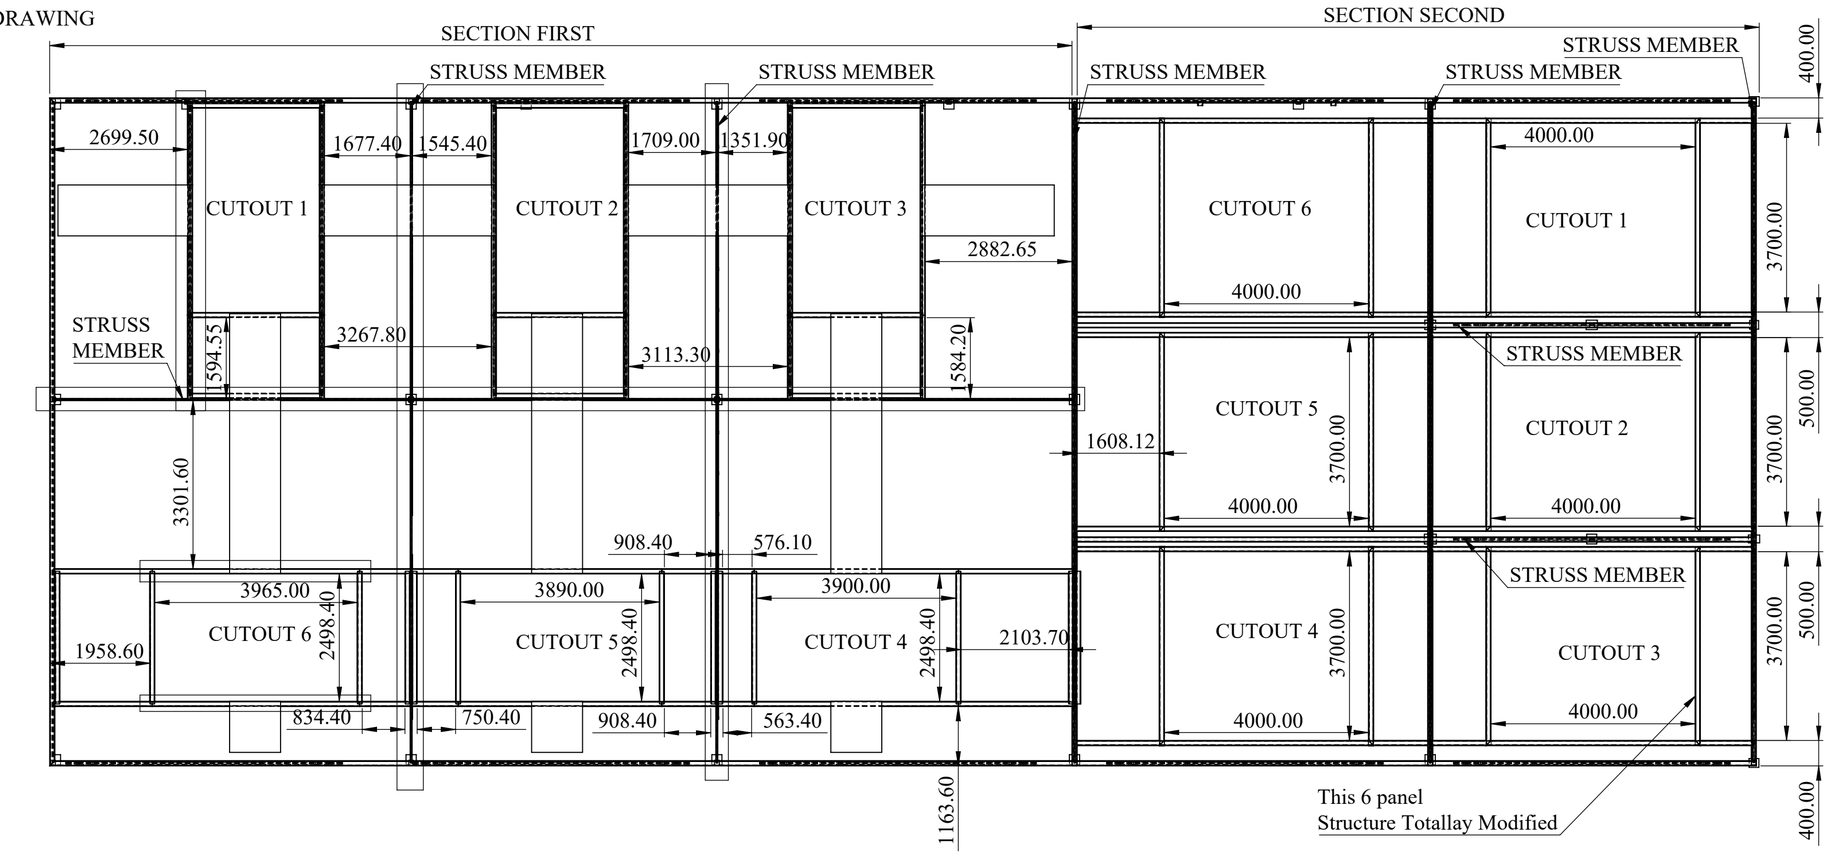

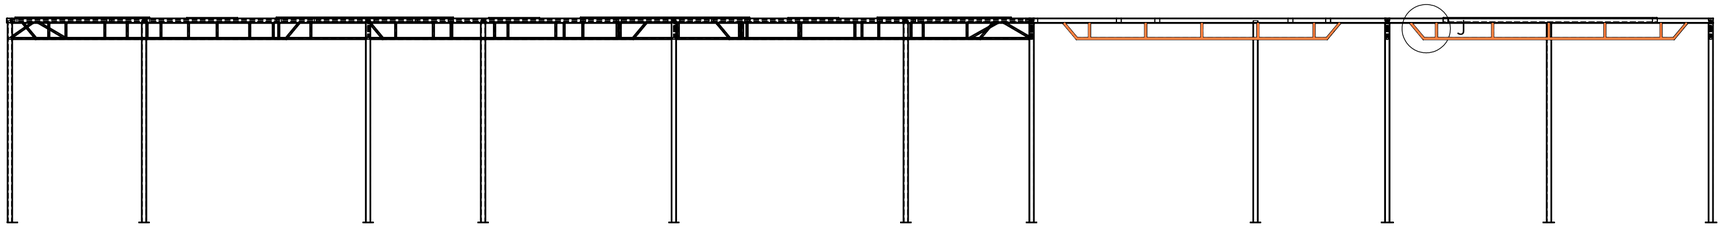
DETAIL J
SCALE 1 : 10
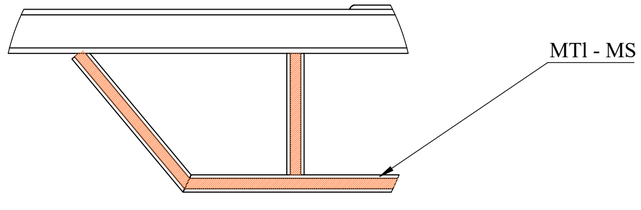
| REV DESCRIPTION | DATE | REV NO |
|---|---|---|
| | 04-07-2025 | REV 00 |
| REV_05_A :<br>DIMENSION MENTIONED FROM STRUSS MEMBER | 21-07-2025 | REV_05_A |

xyz

NOTE :

All Struss Member & Strengthning Member material - MS

SPECIAL INSTRUCTION'S :

| | | | |
|---|---|---|---|
| TITLE - ROOF AUTOMATION | | | |
| DWG NO - NTPL-244-PM-001-00-00-00 | | | |
| NIHVA Technologies Pvt. Ltd. | | | NIHVA TECHNOLOGIES PVT.LTD.PUNE<br>Website - www.nihva.com |
| | NAME | SIGNATURE | DATE |
| DRAWN | V.W. | | 21-07-2025 |
| CHK'D | S.W. | | 22-07-2025 |
| APPV'D | V.T. | | 22-07-2025 |
| PRODUCT - RETRACTABLE ROOF | | | |
| PROJECT NO - NTPL-000-PM | | | REVISION - 05 A |
| SITE LOCATION - | | | WEIGHT - |
| MATRIAL - | | | QTY - 1 |
| If any queries contact - design.nihva@gmail.com | | | SCALE : |
| ALL DIMENSION ARE IN mm | A2 | | PROJECTION METHOD: |
| SHEET 3 OF 16 | | | |