

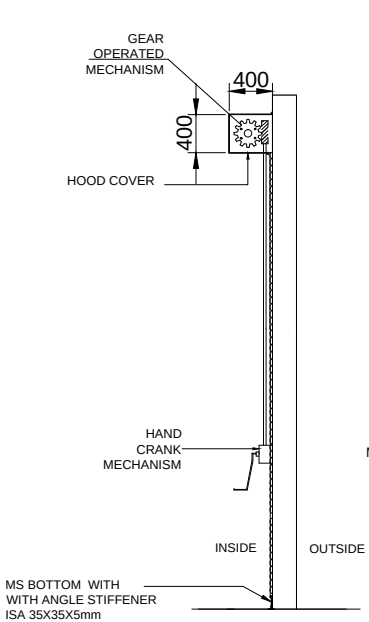



SIDE VIEW

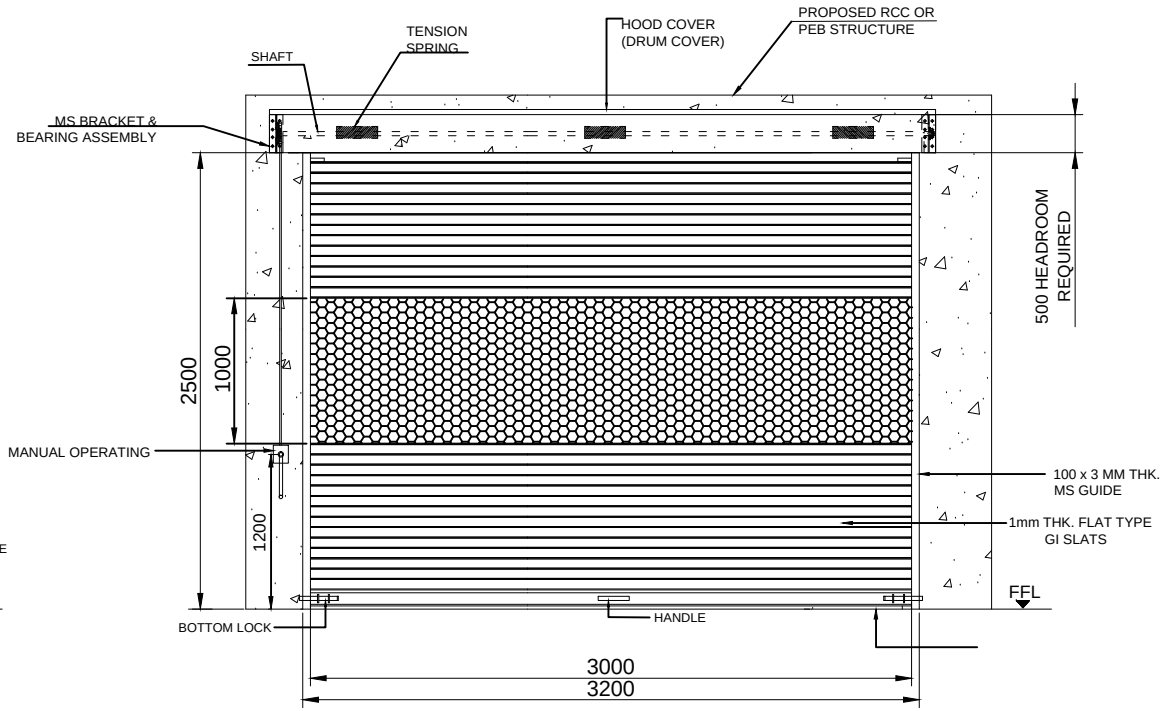


INSIDE ELEVATION

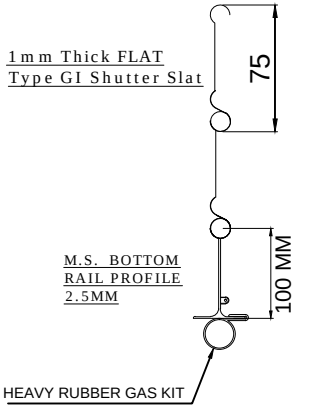


M.S. BOTTOM RAIL PROFILE 2.5MM

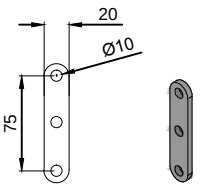


MS BOTTOM WITH ANGLE STIFFNER WITH RUBBER SAFTEY EDGE

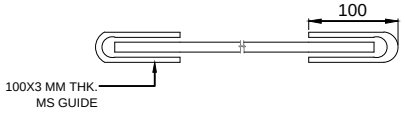

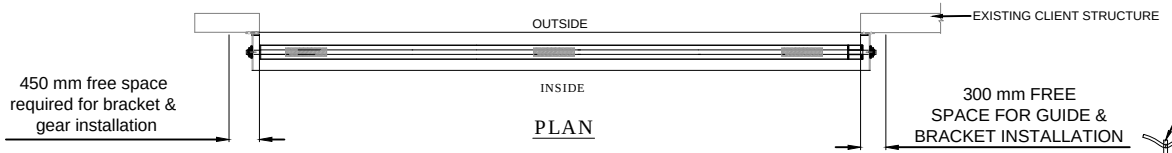

PLAN

5 mm THK. LINK

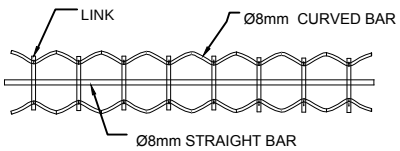

S.NO	FEATURE	EQUIPMENT DETAILS
01	SLATS MODEL	GALVANISE STEEL(GI) SLATS 1mm THK.
02	GUIDE RAIL	100 X 3mm THK MILD STEEL(MS).
03	BOTTOM RAIL	2.5mm THK MILD STEEL (M.S.).
04	HOOD COVER	0.9mm THK GALVANISE STEEL (GI).
05	RAL COLOR	RAL 9002 (WHITE GRAY)

SR.NO.	SIZE	QUANTITY
01	3000(W)X2500(H)	01 NO

NOTE-
1. ALL REQ. CIVIL WORK & M.S STRUCTURE WILL BE IN CLIENT'S SCOPE.

TOLERANCE - ±10mm

This drawing & design is the property of NIHVA TECHNOLOGIES. Not to be sold or copied to any other concern.

TITLE			
GEAR OPERATED ROLLING SHUTTER			
	NAME	SIGN	DATE
DRAWN	P.V.A		20.03.19
CHECK	V.M.T		20.03.19
APPRD.			

NIHVA TECHNOLOGIES PVT. LTD.
NIHVA TECHNOLOGIES PVT. LTD. PUNE
Tel : 020 66304033
Website:- www.nihva.com
Email:- info@nihva.com

CLIENT - SYNERGY

PROJECT-EMBASSY INDUSTRIAL PARKS PVT. LTD.

SITE LOCATION - CHAKAN

If any queries contact : design@nihva.com

DWG. NO. : NIHVA/18-19/0295 | REV- 00

ALL DIMENSION ARE IN mm | SCALE: NTS | WT: | SHEET: 01 OF 01