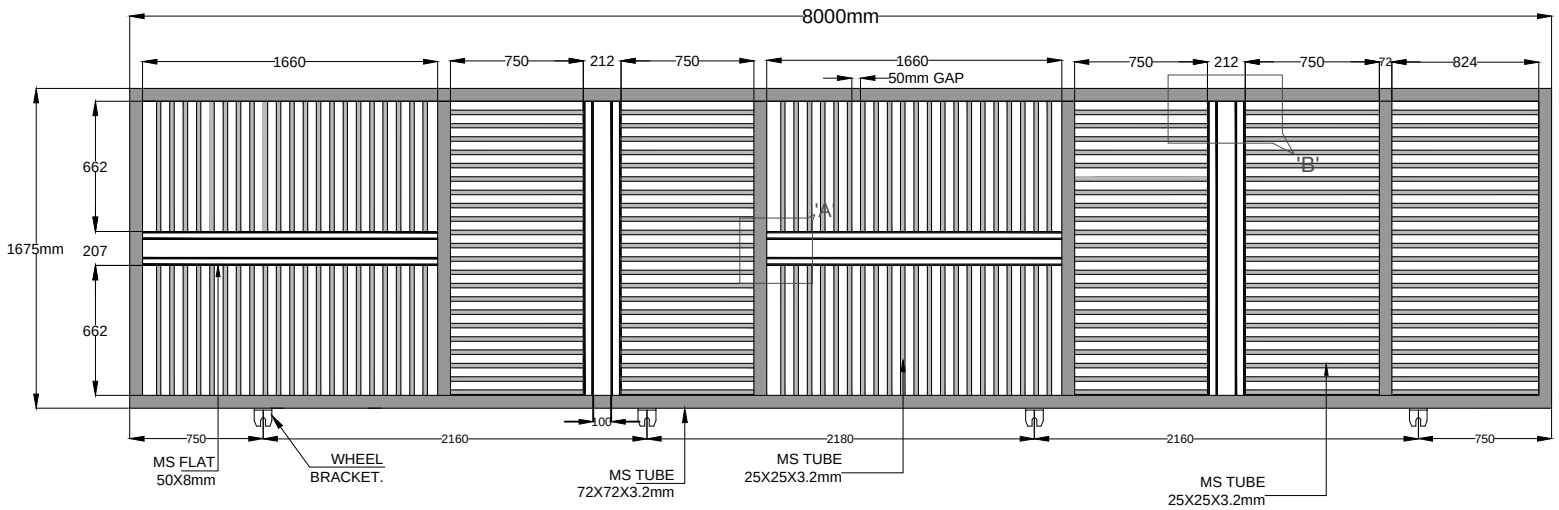

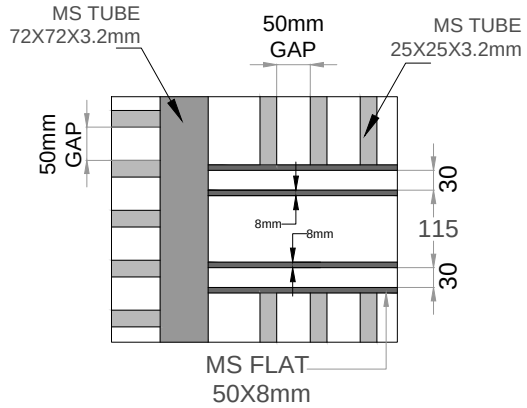

DETAIL VIEW OF 'A'.

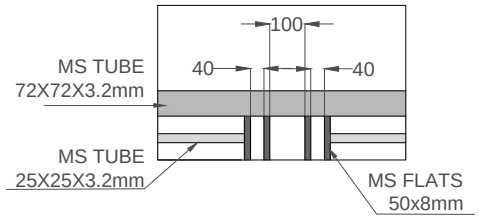

DETAIL VIEW 'D'

NOTE:-WHEEL BRACKET PROFILE ONLY LASER CUTTING.

REV02:-A).GATE HEIGHT HEIGHT CHANGED.
REV01:-A).IN INTERMEDIATE PORTIONS FLATS REPLACED TUBE.

SR NO	CLEAR WIDTH	CLEAR HEIGHT	QTY.
1	8000mm	1800mm	01 NOS

This drawing & design is the property of NIHVA TECHNOLOGIES. Not to be sold or copied to any other concern.

TITLE
SLIDING GATE LEAF 01

NIHVA
NIHVA TECHNOLOGIES PVT. LTD.

NIHVA TECHNOLOGIES
PVT. LTD. PUNE
Tel : 020 66304033
Email:- info@nihva.com
Website:- www.nihva.com

	NAME	SIGN	DATE
DRAWN	SURAJ		03-04-2018
CHECK	OMKAR		03-04-2018
APPRD.	SHEKHAR		03-04-2018

CLIENT -
PROJECT -
SITE LOCATION -
If any queries contact : design@nihva.com
DWG. NO. : NIHVA/17-18/ VDR/0270/R02. REV- 02
ALL DIMENSION ARE IN mm
SCALE: NTS WT: SHEET: 01 OF 01