
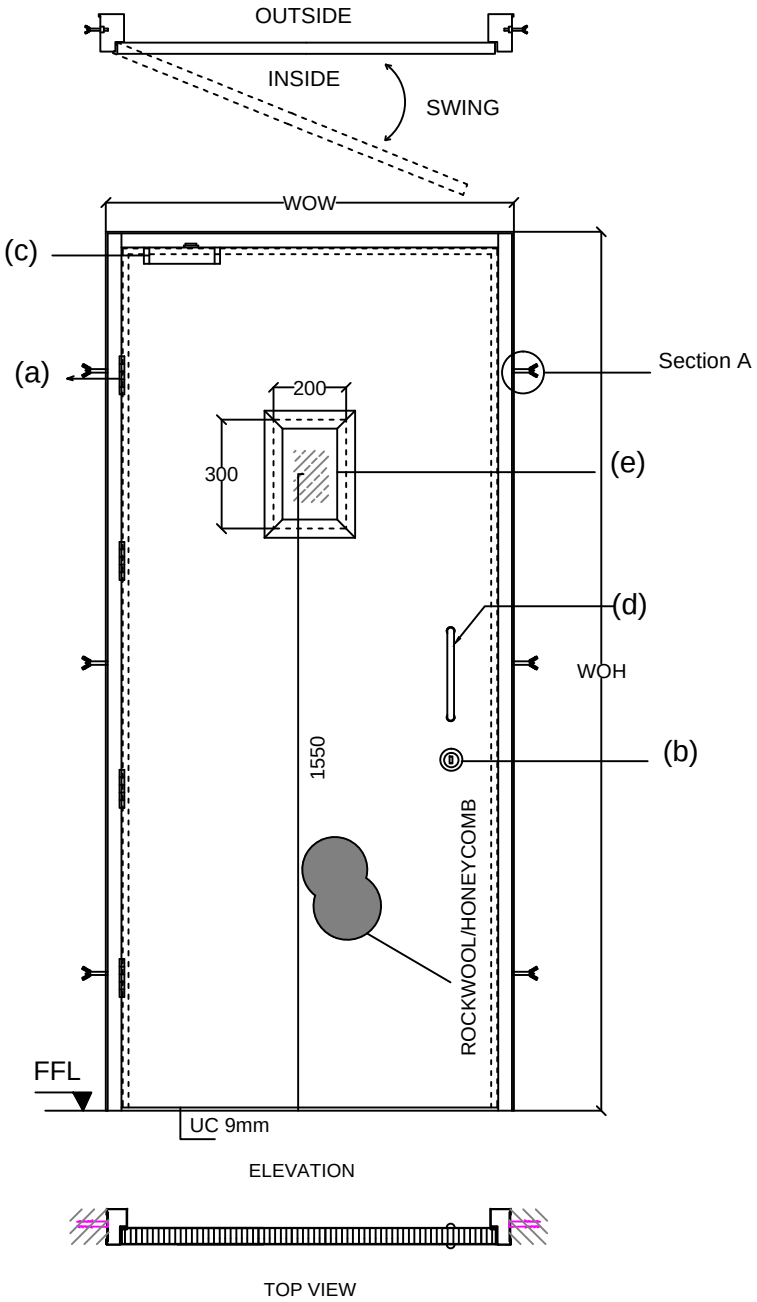


ELEVATION

TOP VIEW

Abbrevation's:
WOW-Wall Opening Width
WOH-Wall Opening Height
UC-Under Cut
FFL-Finished Floor Level

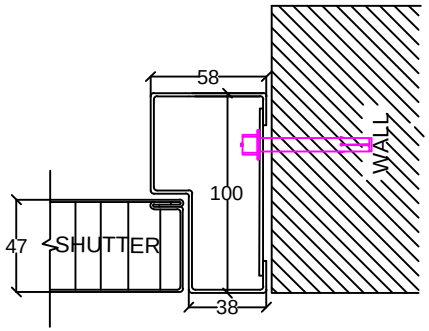

Section A

ASSESORIES DETALES

(a) HINGES: SS Ball bearing butt hinges size 100x75x3mm

(b) LOCK : Mortise Dead lock,Cylinder(Both side key) with Escutcheon

(c) DOOR CLOSER :

(d) HANDLE : SS D HANDLE

(e) VISION PANEL : 5 mm THK. VISION GLASS 200(W) X 300(H)mm

Shutter thickness : 47 mm
Frame Sheet thick : 1.20mm
Shutter sheet thick : 0.80mm
Fixing : On Soliid Brick plasterd wall with Anchors

NOTE:- *All Dimensions are in mm.
*Tolerance:-All Linear Dimensions ±3mm,Others ±0.5mm.
*The Drawing Is For Location of Hardware only. Drawing Does Not Represent The Hardware For More Clarity, Please Go Through Hardware Broucher.

Steel door size

WOW	WOH	TYPE 1	TYPE 2	TYPE 3	TYPE 4	QUANTITY
985	2205			1		1
995	2150			1		1
990	2145	1				1
1000	2165				1	1
705	2065		1			1

NOTE- 1.CLIENT SHOULD MENTION COLOR FOR DOOR.
2.CLIENT SHOULD CHECK DOOR ORIENTATION & APPROVE THE SAME.

REVISION 1- DIMENSIONS OF ALL DOOR REVISED AS PER SITE DIMENSION.

COLOR
1.TRAFFIC WHITE (RAL 9016)
2.LIGHT GREY (RAL 7035)
3.GENTION BLUE (RAL 5010)
4.SIGNAL RED (RAL 3001)

This drawing & designing is the property of NIHVA TECHNOLOGIES. Not be sold or copy to any other concern.

FIRE RATED STEEL DOOR (SINGLE LEAF)

CLIENT APPROVAL

ALL DIMENSION ARE IN mm

	NAME	DATE	SIGN.
DRAWN BY	SURAJ	13/03/17	
CHECK BY	SAGAR P.	13/03/17	
REV.			
APPROVED BY	R.K.	13/03/17	
MFG			

NIHVA TECHNOLOGIES PVT. LTD.
NIHVA TECHNOLOGIES PVT. LTD. PUNE
Tel : 020 66304033
Email:- info@nihva.com
Website:-www.nihva.com

CLIENT - MUKUND CONSTRUCTION
PROJECT - ECOMAX
SITE -RANJANGAON
DWG. NO. - NIHVA/16-17/169/R01
SCALE: NTS | WT: | SHEET: 01 OF 01
If any queries contact : projects@nihva.com